



[illegible]

A

## B

C

## D

# E

DO NOT  
SCALE

F

## ANTENNA MOUNTS

TYPE: EXISTING & PROPOSED TELSTRA  
STEEL PIPES  
COLOUR: GALVANISED FINISH  
REFERENCE DRAWING: SHEETS T3-4  
TO T3-12 & T8-7

## GENERAL NOTES

"DURING BUILD WORKS, THE ELECTRICIAN SHALL CAPTURE AC POWER-RELATED INFORMATION FROM THE SITE AND COMPLETE THE PVA REPORT, PROVIDE AC POWER PHOTOS, AND A SINGLE-LINE DIAGRAM SO THAT AN E2 SHEET CAN BE PRODUCED AS PART OF THE HOP PACK TO TELSTRA"

1. ALL DIMENSIONS ARE IN MILLIMETRES UNLESS SPECIFIED OTHERWISE.
2. BIRD PROOFING CABLES AND ALL ACCESS POINTS ON THE STRUCTURE MUST BE BIRD PROOFED IN ACCORDANCE WITH THE METHODS SPECIFIED IN DOCUMENT NO. 003615  
EXTERNAL PLANT STANDARDS FOR MOBILE BASE STATIONS, SECTION 6.3.3.
3. SERVICES, WHERE SHOWN ARE INDICATIVELY ONLY.  
LOCATION OF ALL RELEVANT EXISTING SERVICES SHALL BE IDENTIFIED AND CONFIRMED PRIOR TO COMMENCING WORK.  
THE CONTRACTOR TO LIAISE WITH RELEVANT AUTHORITIES FOR DIRECTIONS AND PERMITS REQUIRED.  
DIAL BEFORE YOU DIG 1100.
4. FEEDER CONNECTION DETAILS, ELECTRICAL AND MECHANICAL TILTS ARE TO BE OBTAINED FROM CANRAD REPORTS.
5. CONSTRUCTORS ARE TO BE AWARE OF TELSTRA DOCUMENT 007338-C8-11 AND IN PARTICULAR CLAUSE 7.3 & 10.3 WHICH DESCRIBES REQUIREMENTS PERSONNEL MUST UNDERTAKE IN RESPECT TO ASBESTOS MANAGEMENT AT TELSTRA FACILITIES.

## SITE ACCESS

VIA 9 MISSENDEN RD, CAMPERDOWN, NSW 2050  
REFER TO SHEET S1 FOR DETAILS

## SITE SIGNAGE

ALL EME SIGNAGE IS REFERENCED ON  
DRAWINGS S1, S1-1, S3, S3-1 & S3-2.  
REFER TO DOCUMENT 005486 FOR DETAILS.

A

B

## C

D

E


 DENOTES PROPOSED TELSTRA ANTENNA SECTOR  
 AS SHOWN ON SHEET S1-1

**UNAPPROVED  
DRAWING**

|                         |                          |
|-------------------------|--------------------------|
| <b>COMPLIANCE BOX</b>   |                          |
| COMPLETED AS PER DESIGN | <input type="checkbox"/> |
| ALTERATIONS IN RED      | <input type="checkbox"/> |
| NAME (PRINT)            |                          |
| SIGNATURE               | DATE                     |

NOTE: THIS DRAWING TO BE READ IN CONJUNCTION WITH SHEETS S0-1 & S0-2

| ORDER      | DRWN | CHKD | AMENDMENT                                             | EXAM | APPD | DATE     | ISS |
|------------|------|------|-------------------------------------------------------|------|------|----------|-----|
| NA15095.01 | SB   | SB   | AS BUILT 7267045 W0001 LTE700                         | SB   | BB   | 21.11.14 | 3   |
| NA17236.01 | MS   | LY   | AS BUILT - 30060257W0071ERIC - RRU AND LTE2600 UPDATE | KSK  | CF   | 09.05.17 | 4   |
| NA21231.01 | SH   | JG   | FOR CONSTRUCTION 30084274 WO267 5G NR3600             | MWM  | MWM  | 30.04.20 | 5   |
| NA21231.01 | UH   | RM   | AS BUILT - 30084274 WO315 - NR3600                    | DEG  | DEG  | 11.08.20 | 6   |
| NA23527.01 | LB   | WR   | AS BUILT - 30092852WO195ERIC - M700/NR850/DSS26       | PD   | DEG  | 09.02.22 | 7   |
| NA25797.01 | RS   | RT   | FOR CONSTRUCTION - 80005689WO540CYI - LTE2100         | MB   | MB   | 21.05.26 | 8   |

© Telstra Limited ACN 086 174 781 All rights reserved.

|            |        |            |    |
|------------|--------|------------|----|
| DWG<br>NO. | N26167 | SHT<br>NO. | S0 |
|------------|--------|------------|----|



**MOBILE NETWORK SITE 40893**  
**CAMPERDOWN RYDGES MISSENDEN RD**  
 SITE SPECIFIC NOTES - SHEET 1 OF 3  
 9 MISSENDEN RD, CAMPERDOWN, NSW 2050

N26167

|          |    |
|----------|----|
| SHOT NO. | S0 |
|----------|----|

**CYIENT**  
Level-14, 3 Parramatta Square, 153 Macquarie St, Parramatta, NSW 2150, Australia  
T +61 2 8896 6160 | [www.cyient.com](http://www.cyient.com)

1

2

3

4

5

6

A

B

C

D

E

F

EQUIPMENT NOTES - PROJECT NO. NA25797.01

| ITEM | EQUIPMENT                                                        | EQUIPMENT DETAILS                               | EXISTING  | PROPOSED  | TOTAL | REFERENCE DWG                |
|------|------------------------------------------------------------------|-------------------------------------------------|-----------|-----------|-------|------------------------------|
| 1    | 45RU PATHFINDER RACK                                             | 530 x 530 x 2200mm (W,D,H)                      | 1         | 0         | 1     | SHEETS E1 & E5               |
| 2    | DECON RGL-091 RACK                                               | -                                               | 1         | 0         | 1     | SHEETS E1 & E5               |
| 3    | FILTER RACK                                                      | -                                               | 1 (SPARE) | 0         | 0     | SHEET E1                     |
| 4    | HALLAM RACK                                                      | 600 x 800 x 1860mm (W,D,H)                      | 1         | 0         | 1     | SHEET E1                     |
| 5    | ELTEK SP22-HC (PSU)                                              | 600 x 600 x 2200mm (W,D,H)                      | 1         | 0         | 1     | SHEET E4                     |
| 6    | ELTEK SP22-HC RECTIFIERS                                         | FP HE, 2kW                                      | 8         | 0         | 8     | SHEET E4                     |
| 7    | ELTEK SP22-HC DC-DC CONVERTERS                                   | 48V FP2, 1.35kW                                 | 8         | 0         | 8     | SHEET E1                     |
| 8    | ELTEK SP22-HC BATTERY STRINGS                                    | SBS190F EON                                     | 3         | 0         | 3     | SHEET E1                     |
| 9    | ENATEL DC/DC CONVERTERS                                          | CM1748-48                                       | 3         | 0         | 3     | SHEET E1                     |
| 10   | ENATEL DC-DC CONVERTER SUB RACK                                  | -                                               | 1         | 0         | 1     | SHEET E1                     |
| 11   | ERICSSON DCDU                                                    | TO BE INSTALLED IN PATHFINDER RACK AT RT/1/1    | 0         | 1         | 1     | SHEET E5                     |
| 12   | KEREM A100 PDP                                                   | INSTALLED IN DECON RGL-091 RACK AT RT/2/3       | 1         | 0         | 1     | SHEET E5                     |
| 13   | ERICSSON RBS3206 (WCDMA850)                                      | 600(W) x 470(D) x 1850(H) NATURAL COLOUR        | 1 (SPARE) | 0         | 1     | SHEET E1                     |
| 14   | ERICSSON RBS6202                                                 | 500 x 525 x 568mm (W,D,H) SUPPORT TYPE 19" RACK | 1         | 1 (SPARE) | 1     | SHEET E5                     |
| 15   | ERICSSON BB6630                                                  | INSTALLED IN PATHFINDER RACK AT RT/1/1          | 3         | -3        | 0     | SHEET E5                     |
| 16   | ERICSSON RP6672 (LTE700/NR850/LTE1800/LTE2100/NR/LTE2600/NR3600) | TO BE INSTALLED IN PATHFINDER RACK AT RT/1/1    | 0         | 1         | 1     | SHEET E5                     |
| 17   | ERICSSON DUW 30 01                                               | INSTALLED IN PATHFINDER RACK AT RT/1/1          | 1         | -1        | 0     | SHEET E5                     |
| 18   | ERICSSON RUS 02 (B28B)                                           | INSTALLED IN RBS6202 AT RT/1/1                  | 6         | 6 (SPARE) | 6     | SHEETS E1 & E5               |
| 19   | ERICSSON R503                                                    | INSTALLED IN PATHFINDER RACK AT RT/1/1          | 2         | -2        | 0     | SHEETS E1 & E5               |
| 20   | ERICSSON R6675 ROUTER                                            | TO BE RELOCATED IN PATHFINDER RACK RT/1/1       | 1         | 0         | 1     | SHEETS E1 & E5               |
| 21   | FIBRE PATCH PANEL                                                | TO BE INSTALLED IN PATHFINDER RACK RT/1/1       | 1         | 0         | 1     | SHEET E5                     |
| 22   | SLIDE OUT FIBRE MANAGEMENT TRAYS                                 | TO BE INSTALLED IN PATHFINDER RACK RT/1/1       | 1         | 1         | 2     | SHEET E5                     |
| 23   | FIBRE MANAGEMENT TRAYS                                           | -                                               | 2         | -1        | 1     | SHEETS E1 & E5               |
| 24   | HYBRID CABLE MANAGEMENT TRAYS                                    | TO BE INSTALLED IN PATHFINDER RACK RT/1/1       | 0         | 3         | 3     | SHEET E5                     |
| 25   | 4490 ADAPTOR SHELFs                                              | TO BE INSTALLED IN DECON RGL-091 RACK AT RT/2/3 | 0         | 3         | 3     | SHEET E5                     |
| 26   | ERICSSON SITE INTEGRATION UNIT (SIU)                             | 482 x 350 x 45mm (W,D,H)                        | 1         | 1 (SPARE) | 1     | SHEET E1                     |
| 27   | ERICSSON SITE CONTROLLER (ESC)                                   | INSTALLED IN RT/2/4 RACK                        | 1         | 0         | 1     | SHEET E1                     |
| 28   | VERTIV EXTERNAL SURGE PROTECTION DEVICE (12.3 WAY)               | IN WEATHER PROOF ENCLOSURE/WALL MOUNTED         | 1         | 0         | 1     | SHEET E1                     |
| 29   | SPD MODIFICATION KIT 101                                         | -                                               | 1         | 0         | 1     | -                            |
| 30   | W&B RRU INTERFACE JUNCTION BOX (4P16F)                           | TC4039MOBILE02                                  | 3         | 0         | 3     | SHEETS S1-1, S3, S3-1 & S3-2 |

SITE DESIGN BRIEF (LTE2100) (NA25797.01)  
ISSUE 01 DATED 12/09/2025

NOTE: THIS DRAWING TO BE READ IN CONJUNCTION WITH SHEETS S0 & S0-2

CYIENT

Level-14, 3 Parramatta Square, 153 Macquarie St, Parramatta, NSW 2150, Australia  
T +61 2 8896 6160 | www.cyient.com

| ORDER       | DRWN | CHKD | AMENDMENT                                             | EXAM | APPD | DATE     | ISS |
|-------------|------|------|-------------------------------------------------------|------|------|----------|-----|
| XMJUNWCF.01 | KM   | SK   | XMJ - 30053116W0286TELSTRA - LTE700                   | LY   | BB   | 01.07.16 | 4   |
| NA17236.01  | MS   | LY   | AS BUILT - 30060257W0071ERIC - RRU AND LTE2600 UPDATE | KSK  | CF   | 09.05.17 | 5   |
| NA21231.01  | SH   | JG   | FOR CONSTRUCTION 30084274 WO267 5G NR3600             | MWM  | MWM  | 30.04.20 | 6   |
| NA21231.01  | UH   | RM   | AS BUILT - 30084274 WO315 - NR3600                    | DEG  | DEG  | 11.08.20 | 7   |
| NA23527.01  | LB   | WR   | AS BUILT - 30092852WO195ERIC - M700/NR850/DSS26       | PD   | DEG  | 09.02.22 | 8   |
| NA25797.01  | RS   | RT   | FOR CONSTRUCTION - 800056889WO540CYI - LTE2100        | MB   | MB   | 21.05.26 | 9   |

© Telstra Limited ACN 086 174 781 All rights reserved.

UNAPPROVED  
DRAWING

COMPLIANCE BOX

COMPLETED AS PER DESIGN

ALTERATIONS IN RED

NAME (PRINT)

SIGNATURE

DATE

FOR CONSTRUCTION

Telstra

MOBILE NETWORK SITE 40893  
CAMPERDOWN RYDGES MISSENDEN RD  
SITE SPECIFIC NOTES - SHEET 2 OF 3  
9 MISSENDEN RD, CAMPERDOWN, NSW 2050

DWG NO.

N26167

SHT NO.

S0-1

DO NOT SCALE

F

1

2

3

4



5

6

A3




|   |                                          |                                                             |                                                      |              |           |       |                                |                              |
|---|------------------------------------------|-------------------------------------------------------------|------------------------------------------------------|--------------|-----------|-------|--------------------------------|------------------------------|
|   | 1                                        | 2                                                           | 3                                                    | 4            | 5         | 6     |                                |                              |
| A   | EQUIPMENT NOTES - PROJECT NO. NA25797.01 |                                                             |                                                      |              |           |       | A                              |                              |
|   | ITEM                                     | EQUIPMENT                                                   | EQUIPMENT DETAILS                                    | EXISTING     | PROPOSED  | TOTAL |                                | REFERENCE DWG                |
|   | 31                                       | ERICSSON RRUS 32 B3 (LTE1800)                               | 431 (W) x 182 (D) x 500mm (H) NATURAL COLOUR         | 3            | -3        | 0     |                                | SHEETS S1-1, S3, S3-1 & S3-2 |
|   | 32                                       | ERICSSON RRUS 32 B7 (NR/LTE2600)                            | 431 (W) x 182 (D) x 500mm (H) NATURAL COLOUR         | 3            | -3        | 0     |                                | SHEETS S1-1, S3, S3-1 & S3-2 |
|   | 33                                       | ERICSSON RADIO 4480 (B5/B28) (WCDMA850/LTE700/NR850)        | 400 x 145 x 550mm (W,D,H) NATURAL COLOUR             | 3            | -3        | 0     |                                | SHEET E5                     |
|   | 34                                       | ERICSSON RADIO 4485 (B3/B1/B7) (LTE1800/LTE2100/NR/LTE2600) | 398 x 145 x 533mm (W,D,H) NATURAL COLOUR             | 0            | 3         | 3     |                                | SHEETS S1-1, S3, S3-1 & S3-2 |
|   | 35                                       | ERICSSON RADIO 4490HP (B28/B26) (LTE700/NR850)              | 397 x 165 x 522mm (W,D,H) NATURAL COLOUR             | 0            | 3         | 3     |                                | SHEET E5                     |
| B   | 36                                       | ERICSSON DUAL DUPLEX FILTER (WCDMA850)                      | KRF 102 268/1                                        | 3 (SPARE)    | 0         | 3     | SHEET E5                       |                              |
|   | 37                                       | TRIASX DUAL DUPLEX FILTER (WCDMA850)                        | DDF0022                                              | 3 (SPARE)    | 0         | 3     | SHEET E5                       |                              |
|   | 38                                       | KAELUS TWIN BANDSTOP FILTER                                 | BSF0020F1V2                                          | 6            | -6        | 0     | SHEET E5                       |                              |
|   | 39                                       | KAELUS QUAD FILTERS (LTE700/NR850)                          | KA-6035                                              | 0            | 3         | 3     | SHEET E5                       |                              |
|   | 40                                       | KAELUS TWIN COMBINER                                        | DBC0086F1V1-1 INSTALLED IN PATHFINDER RACK AT RT/1/1 | 3            | 3 (SPARE) | 3     | SHEET E5                       |                              |
|   | 41                                       | TRIASX DUAL DUPLEX FILTER (WCDMA850)                        | DDF0022F1V1                                          | 6 (SPARE)    | 0         | 6     | SHEET E1                       |                              |
|   | 42                                       | KAELUS TWIN TMA (LTE700/WCDMA850/NR850)                     | TMA21058F01V2-1E                                     | 6            | -6        | 0     | SHEETS S1-1, S3, S3-1 & S3-2   |                              |
|   | 43                                       | KAELUS TMA (LTE700/NR850)                                   | KA-1031 TMA                                          | 0            | 6         | 6     | SHEETS S1-1, S3, S3-1 & S3-2   |                              |
|   | 44                                       | ANDREW LDF5-50                                              | 30m LENGTH                                           | 6, 4 (SPARE) | 6 (SPARE) | 10    | SHEETS S1-1, S3, S3-1 & S3-2   |                              |
|   | 45                                       | RFS LCF78-50JA                                              | 38m LENGTH                                           | 3            | 0         | 3     | SHEETS S1-1, S3, S3-1 & S3-2   |                              |
|   | 46                                       | RFS LCF78-50J                                               | 38m LENGTH                                           | 3            | 0         | 3     | SHEETS S1-1, S3, S3-1 & S3-2   |                              |
|   | 47                                       | RFS LCF78-50JA                                              | 27m LENGTH                                           | 2            | 0         | 2     | SHEETS S1-1, S3, S3-1 & S3-2   |                              |
|   | 48                                       | RFS LCF78-50J                                               | 27m LENGTH                                           | 2            | 0         | 2     | SHEETS S1-1, S3, S3-1 & S3-2   |                              |
| C   | 49                                       | RFS LCF78-50JA                                              | 13m LENGTH                                           | 1            | 0         | 1     | SHEETS S1-1, S3, S3-1 & S3-2   |                              |
|   | 50                                       | RFS LCF78-50J                                               | 13m LENGTH                                           | 1            | 0         | 1     | SHEETS S1-1, S3, S3-1 & S3-2   |                              |
|   | 51                                       | W&B HYBRID CABLE 7/8"                                       | 30m LENGTH                                           | 1            | 0         | 1     | SHEETS S1-1, S3, S3-1 & S3-2   |                              |
|   | 52                                       | W&B HYBRID CABLE 7/8"                                       | 40m LENGTH                                           | 2            | 0         | 2     | SHEETS S1-1, S3, S3-1 & S3-2   |                              |
|   | 53                                       | GPS SPLITTER                                                | INSTALLED IN 45RU PATHFINDER RACK AT RT/1/1          | 1            | 1 (SPARE) | 1     | SHEET E5                       |                              |
|   | 54                                       | GPS RECEIVER                                                | INSTALLED IN 45RU PATHFINDER RACK AT RT/1/1          | 2            | -2        | 0     | SHEET E5                       |                              |
|   | 55                                       | GPS RECEIVER UNIT                                           | ERICSSION GRU 05 01 RECEIVER NCD90189/1              | 0            | 1         | 1     | SHEET E5                       |                              |
|   | 56                                       | GPS ANTENNA (LTE)                                           | GPS KRE 101 2082 1 OMNI                              | 1            | -1        | 0     | SHEETS S1, S3, S3-1, S3-2 & E1 |                              |
|   | 57                                       | KAELUS, DUAL BAND GNSS GPS ACTIVE ANT                       | KNAA-7005-1110                                       | 0            | 1         | 1     | SHEETS S1, S3, S3-1 & S3-2     |                              |
|   | 58                                       | RF JUMPER 1_5M N F TO SMA M                                 | TSR951339/1500                                       | 0            | 1         | 1     | -                              |                              |
| D   | 59                                       | GPS WBT TOD CABLE                                           | WBT R6000 TOD CABLE - 3M                             | 0            | 1         | 1     | -                              |                              |
|   | 60                                       | GPS SYNC CABLE                                              | RPM1136127/2000                                      | 0            | 1         | 1     | -                              |                              |
|   | 61                                       | LENMIC L600P2 AIR CONDITIONER                               | WALL MOUNTED RAC TYPE                                | 2            | 0         | 2     | SHEET E1                       |                              |
|   | 62                                       | COOLING FAN                                                 | L355D                                                | 1            | 0         | 1     | SHEET E1                       |                              |
|   | 63                                       | COOLING FAN FILTER                                          | -                                                    | 1            | -1        | 0     | SHEET E1                       |                              |
|   | 64                                       | COOLING FAN FILTER                                          | VAK00019                                             | 0            | 1         | 1     | SHEET E1                       |                              |
| E   |                                          |                                                             |                                                      |              |           |       | E                              |                              |
|   |                                          |                                                             |                                                      |              |           |       |                                |                              |
| DO NOT SCALE   |                                          |                                                             |                                                      |              |           |       |                                |                              |
| DIMS IN   |                                          |                                                             |                                                      |              |           |       |                                |                              |
|   |                                          |                                                             |                                                      |              |           |       |                                |                              |
| <div><div><div>UNAPPROVED<br/>DRAWING</div><div><div>COMPLIANCE BOX</div><div>COMPLETED AS PER DESIGN <input type="checkbox"/></div><div>ALTERATIONS IN RED <input type="checkbox"/></div><div>NAME (PRINT) <input type="text"/></div><div>SIGNATURE <input type="text"/></div><div>DATE <input type="text"/></div></div><div>FOR CONSTRUCTION</div></div></div>   |                                          |                                                             |                                                      |              |           |       |                                |                              |
| <div><div><div><div><div>NOTE: THIS DRAWING TO BE READ IN CONJUNCTION WITH SHEETS S0 &amp; S0-1</div></div><div><div><div>ORDER</div><div>DRWN</div><div>CHKD</div><div>AMENDMENT</div><div>EXAM</div><div>APPD</div><div>DATE</div><div>ISS</div></div><div><div>NA25797.01</div><div>RS</div><div>RT</div><div>FOR CONSTRUCTION - 80005689W0540CYI - LTE2100</div><div>MB</div><div>MB</div><div>21.05.26</div><div>1</div></div></div><div><div><div><div><div>CYIENT</div><div>Level-14, 3 Parramatta Square, 153 Macquarie St,<br/>Parramatta, NSW 2150, Australia<br/>T +61 2 8896 6160   www.cyient.com</div></div><div><div>© Telstra Limited</div><div>ACN 086 174 781</div><div>All rights reserved.</div></div></div><div><div><div><div>Telstra</div><div>MOBILE NETWORK SITE 40893<br/>CAMPERDOWN RYDGES MISSENDEN RD<br/>SITE SPECIFIC NOTES - SHEET 3 OF 3<br/>9 MISSENDEN RD, CAMPERDOWN, NSW 2050</div></div><div><div>DWG NO.</div><div>N26167</div><div>SHT NO.</div><div>S0-2</div></div></div></div></div></div></div></div></div> |                                          |                                                             |                                                      |              |           |       |                                |                              |
| <div><div>1</div><div>2</div><div>3</div><div>4</div><div>5</div><div>6</div><div>A3V</div></div>   |                                          |                                                             |                                                      |              |           |       |                                |                              |

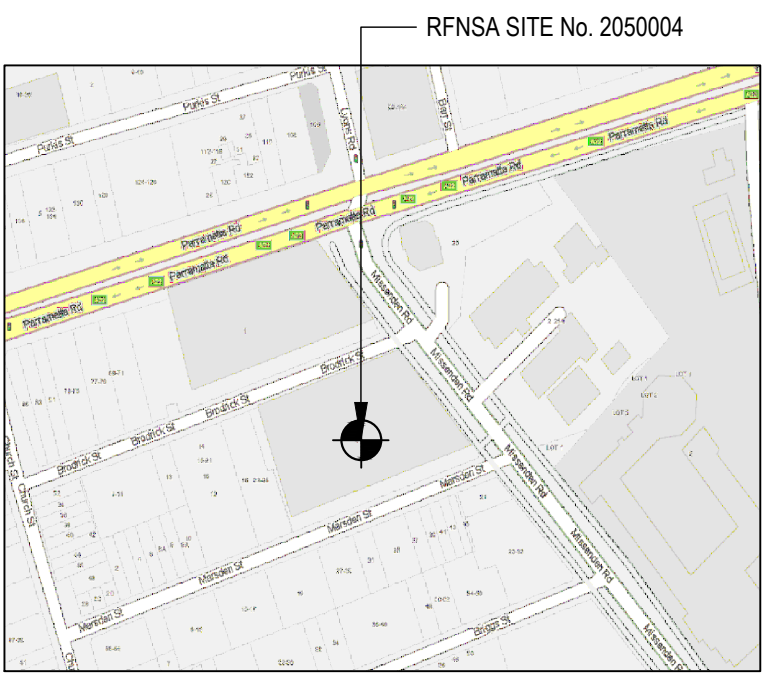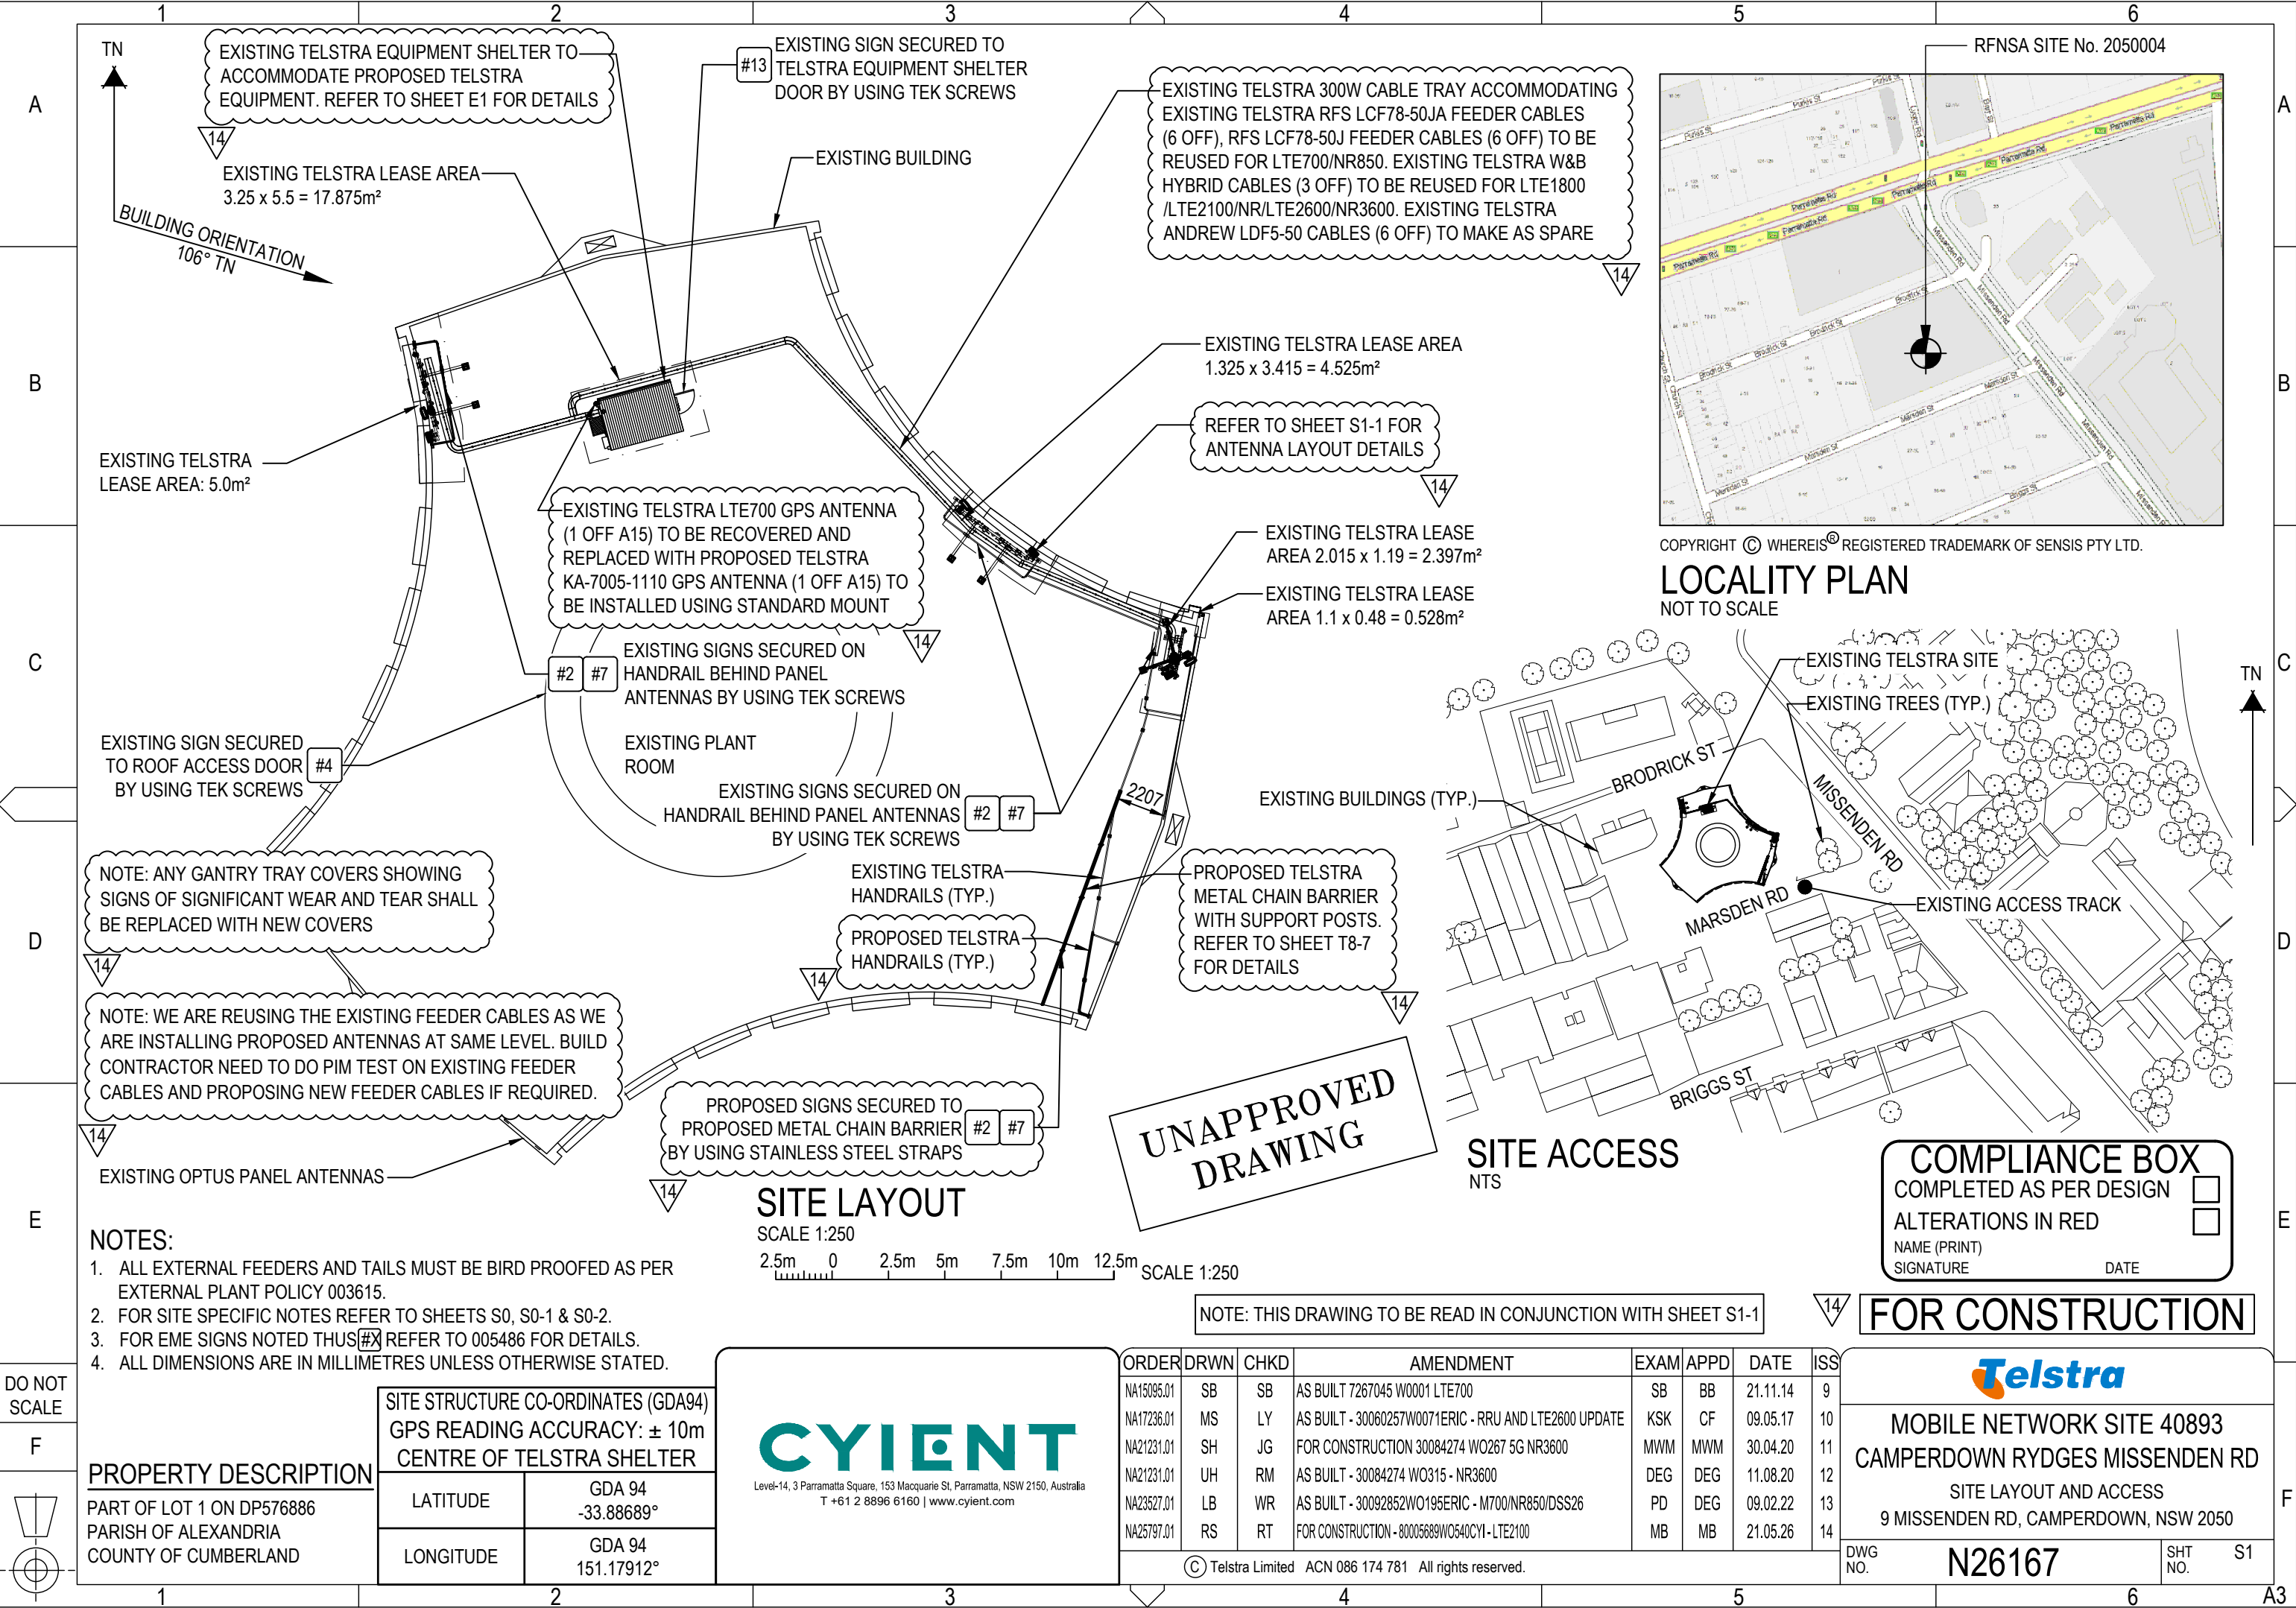

COPYRIGHT © WHEREIS® REGISTERED TRADEMARK OF SENSIS PTY LTD.

LOCALITY PLAN  
NOT TO SCALE

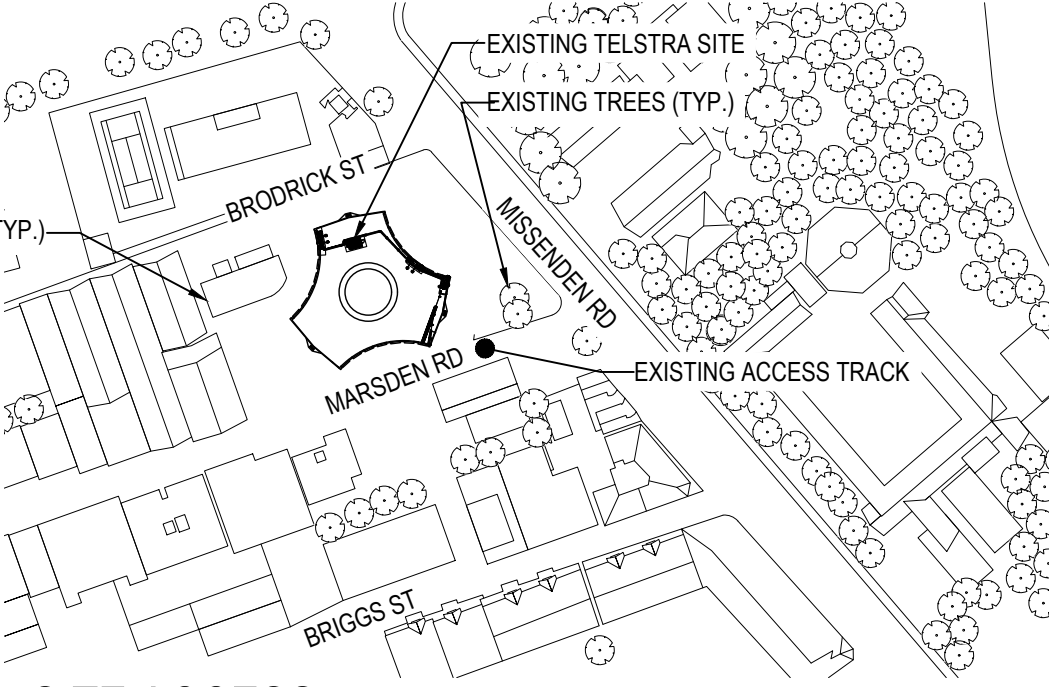

SITE ACCESS  
NTS

COMPLIANCE BOX

COMPLETED AS PER DESIGN

ALTERATIONS IN RED

NAME (PRINT)

SIGNATURE

DATE

- NOTES:
1. ALL EXTERNAL FEEDERS AND TAILS MUST BE BIRD PROOFED AS PER EXTERNAL PLANT POLICY 003615.
  2. FOR SITE SPECIFIC NOTES REFER TO SHEETS S0, S0-1 & S0-2.
  3. FOR EME SIGNS NOTED THUS#X REFER TO 005486 FOR DETAILS.
  4. ALL DIMENSIONS ARE IN MILLIMETRES UNLESS OTHERWISE STATED.

PROPERTY DESCRIPTION

PART OF LOT 1 ON DP576886  
PARISH OF ALEXANDRIA  
COUNTY OF CUMBERLAND

SITE STRUCTURE CO-ORDINATES (GDA94)  
GPS READING ACCURACY: ± 10m  
CENTRE OF TELSTRA SHELTER

|           |                      |
|-----------|----------------------|
| LATITUDE  | GDA 94<br>-33.88689° |
| LONGITUDE | GDA 94<br>151.17912° |

CYIENT

Level-14, 3 Parramatta Square, 153 Macquarie St, Parramatta, NSW 2150, Australia  
T +61 2 8896 6160 | www.cyient.com

| ORDER      | DRWN | CHKD | AMENDMENT                                             | EXAM | APPD | DATE     | ISS |
|------------|------|------|-------------------------------------------------------|------|------|----------|-----|
| NA15095.01 | SB   | SB   | AS BUILT 7267045 W0001 LTE700                         | SB   | BB   | 21.11.14 | 9   |
| NA17236.01 | MS   | LY   | AS BUILT - 30060257W0071ERIC - RRU AND LTE2600 UPDATE | KSK  | CF   | 09.05.17 | 10  |
| NA21231.01 | SH   | JG   | FOR CONSTRUCTION 30084274 W0267 5G NR3600             | MWM  | MWM  | 30.04.20 | 11  |
| NA21231.01 | UH   | RM   | AS BUILT - 30084274 W0315 - NR3600                    | DEG  | DEG  | 11.08.20 | 12  |
| NA23527.01 | LB   | WR   | AS BUILT - 30092852W0195ERIC - M700/NR850/DSS26       | PD   | DEG  | 09.02.22 | 13  |
| NA25797.01 | RS   | RT   | FOR CONSTRUCTION - 80005689W0540CYI - LTE2100         | MB   | MB   | 21.05.26 | 14  |

© Telstra Limited ACN 086 174 781 All rights reserved.


FOR CONSTRUCTION



MOBILE NETWORK SITE 40893  
CAMPERDOWN RYDGES MISSENDEN RD  
SITE LAYOUT AND ACCESS  
9 MISSENDEN RD, CAMPERDOWN, NSW 2050

DWG NO. N26167 SHT NO. S1



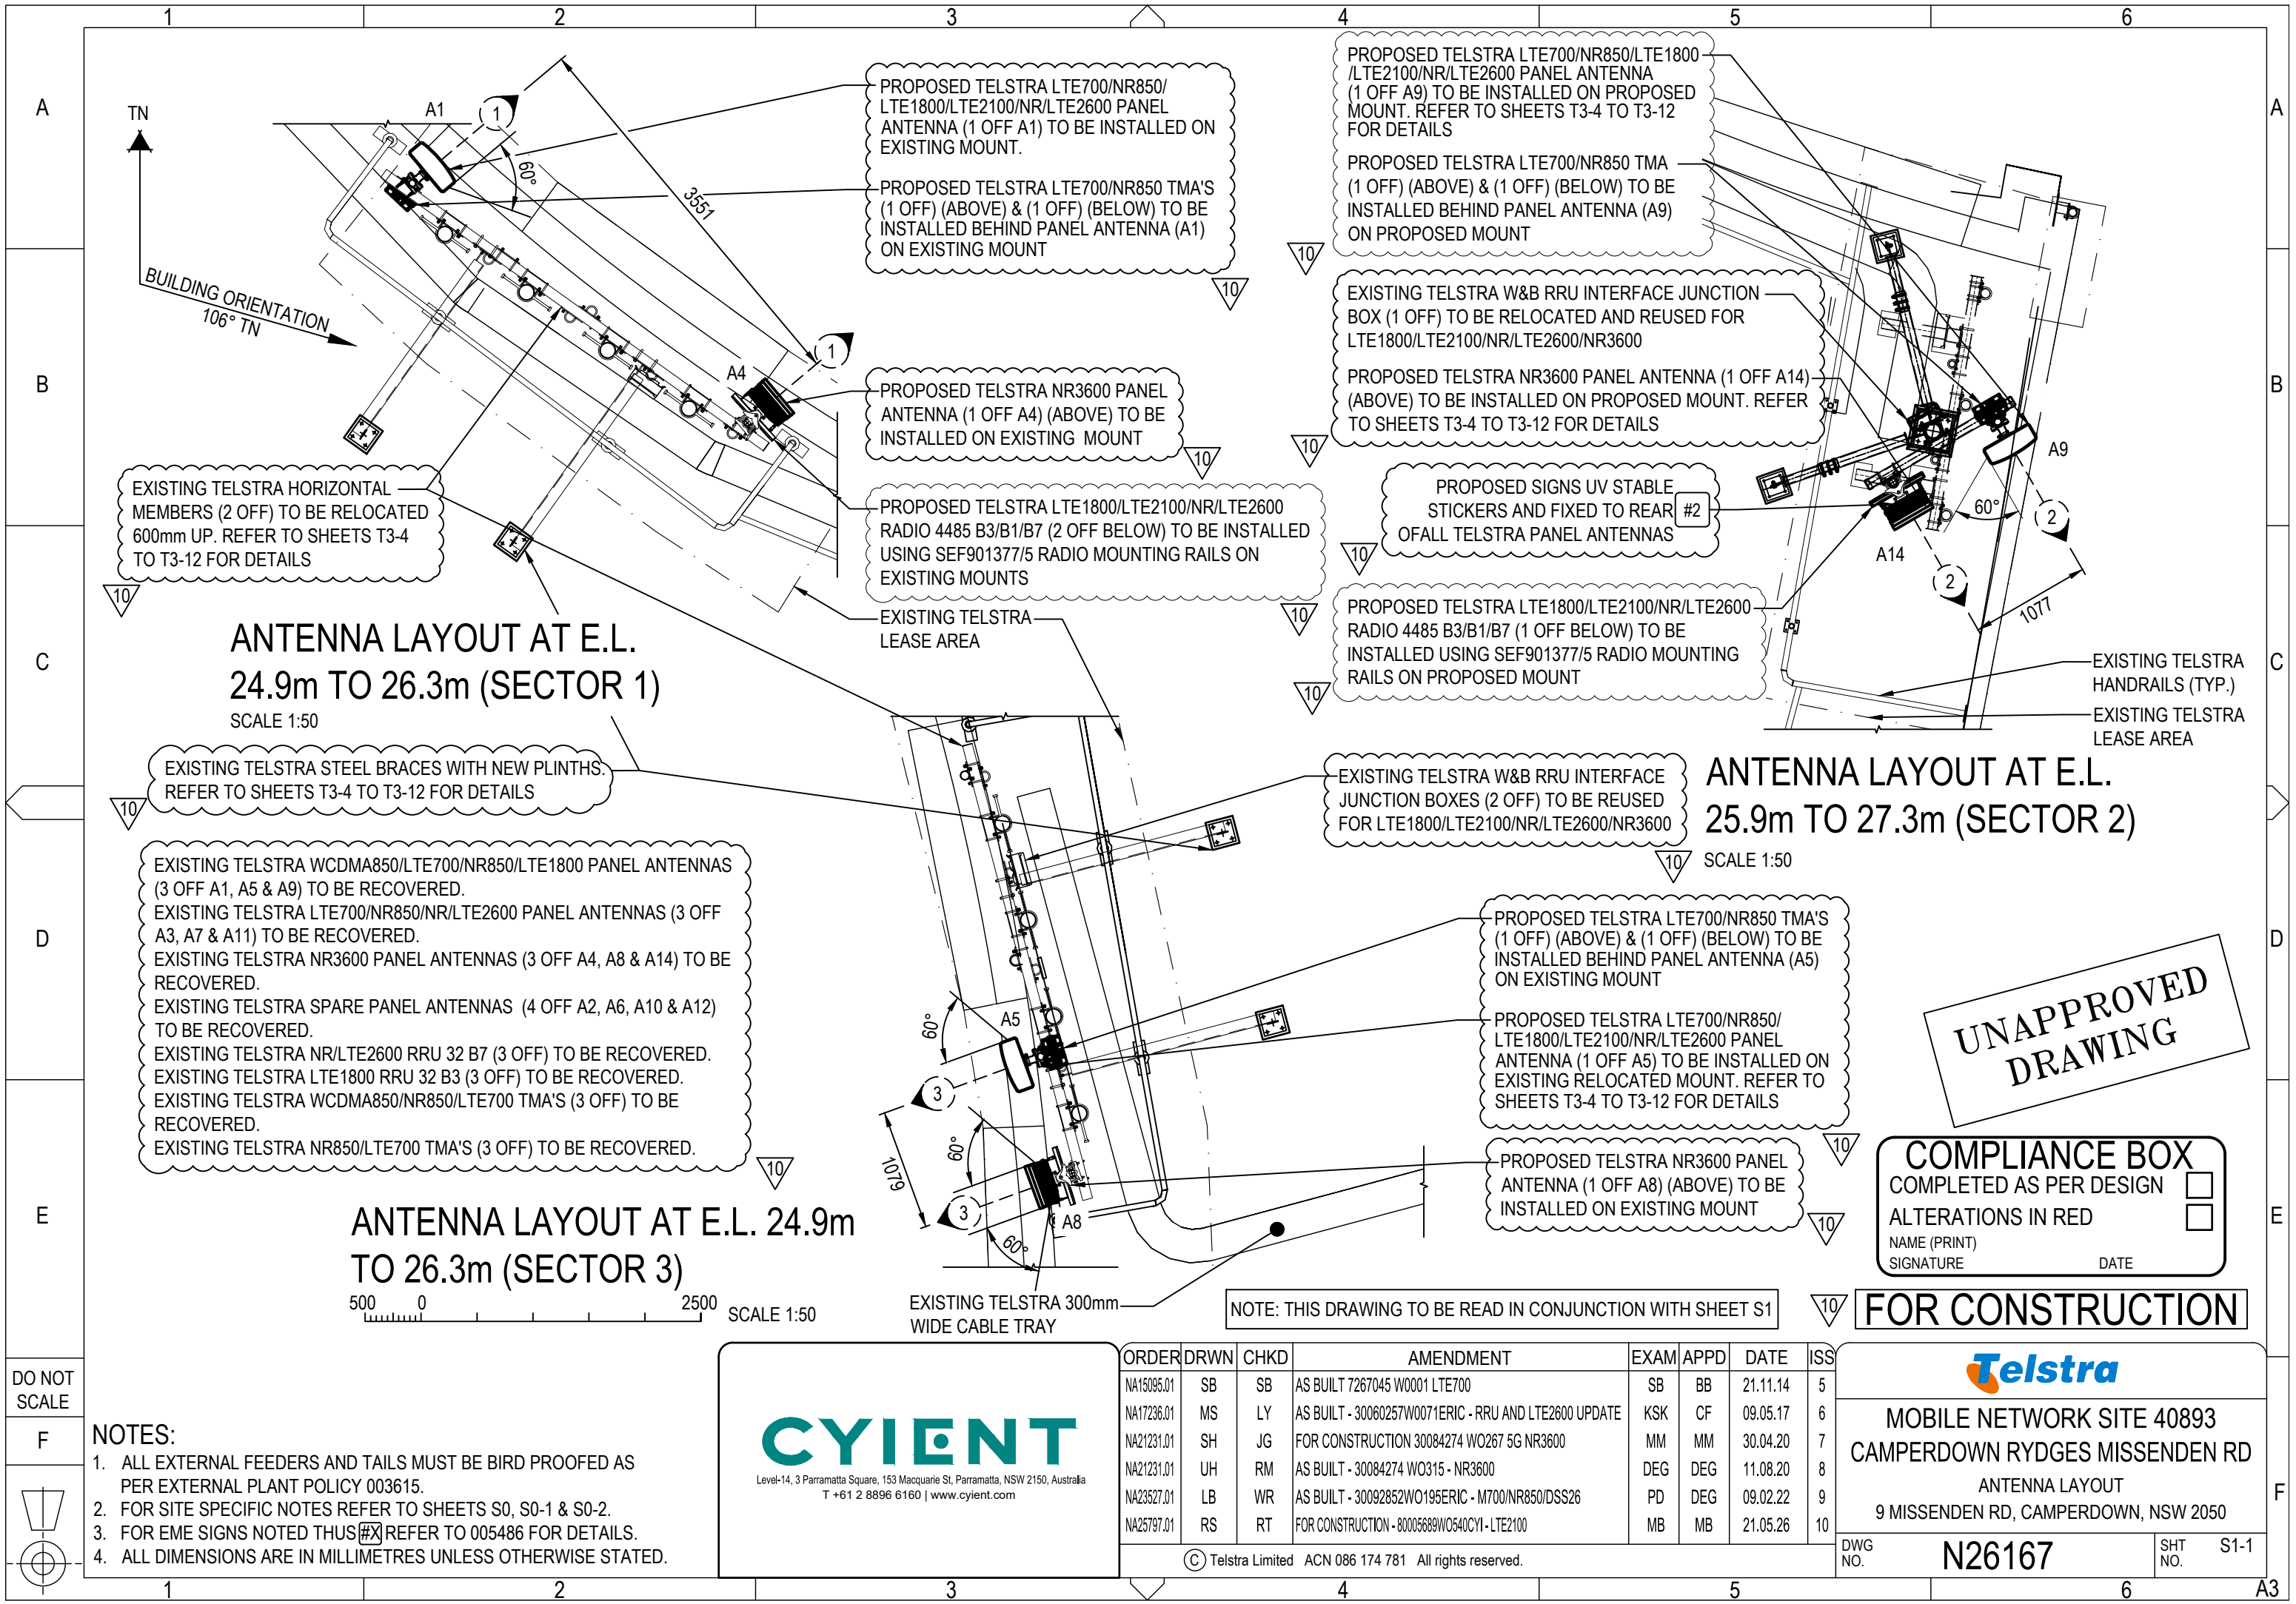

ANTENNA LAYOUT AT E.L.  
24.9m TO 26.3m (SECTOR 1)

SCALE 1:50

ANTENNA LAYOUT AT E.L.  
25.9m TO 27.3m (SECTOR 2)

SCALE 1:50

ANTENNA LAYOUT AT E.L. 24.9m  
TO 26.3m (SECTOR 3)

SCALE 1:50

UNAPPROVED  
DRAWING

COMPLIANCE BOX  
COMPLETED AS PER DESIGN ☐  
ALTERATIONS IN RED ☐  
NAME (PRINT) \_\_\_\_\_  
SIGNATURE \_\_\_\_\_ DATE \_\_\_\_\_

FOR CONSTRUCTION

| ORDER      | DRWN | CHKD | AMENDMENT                                             | EXAM | APPD | DATE     | ISS |
|------------|------|------|-------------------------------------------------------|------|------|----------|-----|
| NA15095.01 | SB   | SB   | AS BUILT 7267045 W0001 LTE700                         | SB   | BB   | 21.11.14 | 5   |
| NA17236.01 | MS   | LY   | AS BUILT - 30060257W0071ERIC - RRU AND LTE2600 UPDATE | KSK  | CF   | 09.05.17 | 6   |
| NA21231.01 | SH   | JG   | FOR CONSTRUCTION 30084274 W0267 5G NR3600             | MM   | MM   | 30.04.20 | 7   |
| NA21231.01 | UH   | RM   | AS BUILT - 30084274 W0315 - NR3600                    | DEG  | DEG  | 11.08.20 | 8   |
| NA23527.01 | LB   | WR   | AS BUILT - 30092852W0195ERIC - M700/NR850/DSS26       | PD   | DEG  | 09.02.22 | 9   |
| NA25797.01 | RS   | RT   | FOR CONSTRUCTION - 80005689W0540CYI - LTE2100         | MB   | MB   | 21.05.26 | 10  |

© Telstra Limited ACN 086 174 781 All rights reserved.



MOBILE NETWORK SITE 40893  
CAMPERDOWN RYDGES MISSENDEN RD  
ANTENNA LAYOUT  
9 MISSENDEN RD, CAMPERDOWN, NSW 2050

DWG  
NO.

N26167

SHT  
NO.

S1-1

- NOTES:
- ALL EXTERNAL FEEDERS AND TAILS MUST BE BIRD PROOFED AS PER EXTERNAL PLANT POLICY 003615.
  - FOR SITE SPECIFIC NOTES REFER TO SHEETS S0, S0-1 & S0-2.
  - FOR EME SIGNS NOTED THUS (#X) REFER TO 005486 FOR DETAILS.
  - ALL DIMENSIONS ARE IN MILLIMETRES UNLESS OTHERWISE STATED.

CYIENT

Level-14, 3 Parramatta Square, 153 Macquarie St, Parramatta, NSW 2150, Australia  
T +61 2 8896 6160 | www.cyient.com

**WEST ELEVATION**

SCALE 1:150

1.5m 0 1.5m 3m 4.5m 6m 7.5m SCALE 1:150

**UNAPPROVED DRAWING**

**COMPLIANCE BOX**  
COMPLETED AS PER DESIGN ☐  
ALTERATIONS IN RED ☐  
NAME (PRINT) \_\_\_\_\_  
SIGNATURE \_\_\_\_\_ DATE \_\_\_\_\_

**FOR CONSTRUCTION**

NOTE: THIS DRAWING TO BE READ IN CONJUNCTION WITH SHEETS S3-1, S3-2 & S3-3

| ORDER      | DRWN | CHKD | AMENDMENT                                             | EXAM | APPD | DATE     | ISS |
|------------|------|------|-------------------------------------------------------|------|------|----------|-----|
| NA15095.01 | SB   | SB   | AS BUILT 7267045 W0001 LTE700                         | SB   | BB   | 21.11.14 | 13  |
| NA17236.01 | MS   | LY   | AS BUILT - 30060257W0071ERIC - RRU AND LTE2600 UPDATE | KSK  | CF   | 09.05.17 | 14  |
| NA21231.01 | SH   | JG   | FOR CONSTRUCTION 30084274 W0267 5G NR3600             | MM   | MM   | 30.04.20 | 15  |
| NA21231.01 | UH   | RM   | AS BUILT - 30084274 W0315 - NR3600                    | DEG  | DEG  | 11.08.20 | 16  |
| NA23527.01 | LB   | WR   | AS BUILT - 30092852W0195ERIC - M700/NR850/DSS26       | PD   | DEG  | 09.02.22 | 17  |
| NA25797.01 | RS   | RT   | FOR CONSTRUCTION - 80005689W0540CYI - LTE2100         | MB   | MB   | 21.05.26 | 18  |

© Telstra Limited ACN 086 174 781 All rights reserved.

**CYIENT**  
Level-14, 3 Parramatta Square, 153 Macquarie St. Parramatta, NSW 2150, Australia  
T +61 2 8896 6160 | www.cyient.com


**Telstra**  
MOBILE NETWORK SITE 40893  
CAMPERDOWN RYDGES MISSENDEN RD  
WEST ELEVATION  
9 MISSENDEN RD, CAMPERDOWN, NSW 2050

DWG NO. **N26167** SHT NO. **S3**

**NOTES:**

- ALL EXTERNAL FEEDERS AND TAILS MUST BE BIRD PROOFED AS PER EXTERNAL PLANT POLICY 003615.
- FOR SITE SPECIFIC NOTES REFER TO SHEETS S0, S0-1 & S0-2.
- FOR EME SIGNS NOTED THUS (#X) REFER TO 005486 FOR DETAILS.
- ALL DIMENSIONS ARE IN MILLIMETRES UNLESS OTHERWISE STATED.



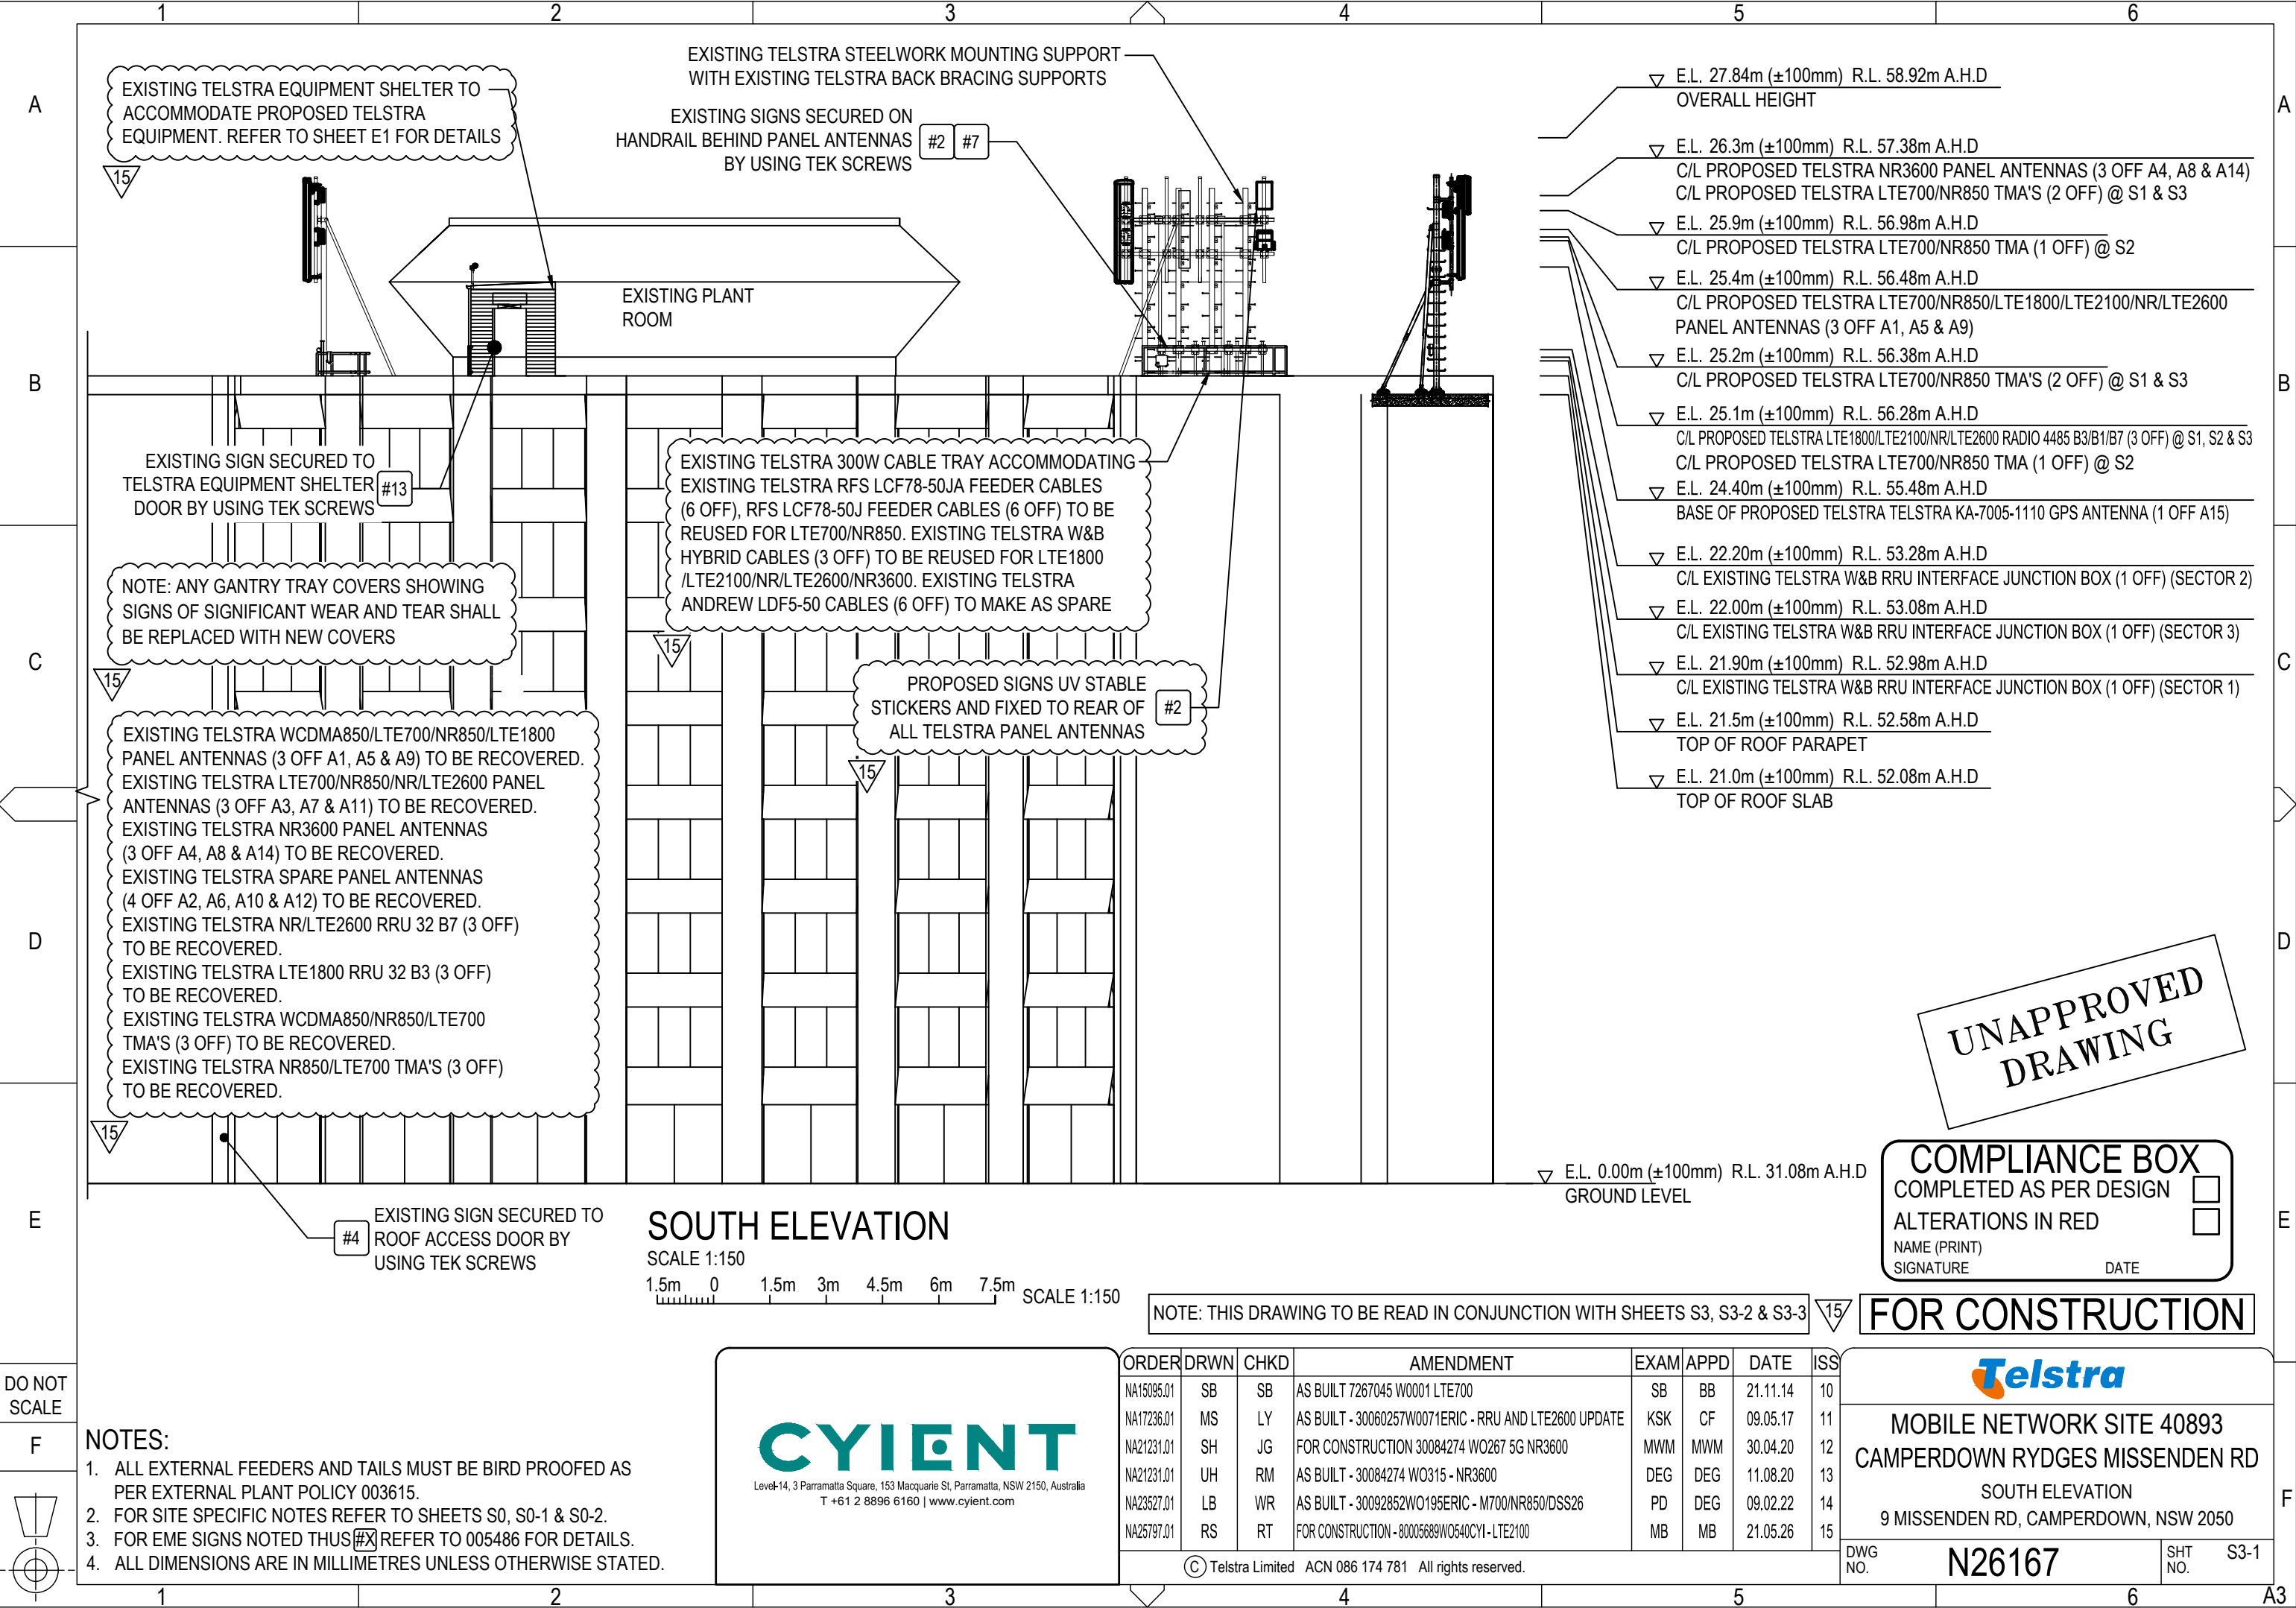

EXISTING TELSTRA EQUIPMENT SHELTER TO ACCOMMODATE PROPOSED TELSTRA EQUIPMENT. REFER TO SHEET E1 FOR DETAILS

EXISTING TELSTRA STEELWORK MOUNTING SUPPORT WITH EXISTING TELSTRA BACK BRACING SUPPORTS  
EXISTING SIGNS SECURED ON HANDRAIL BEHIND PANEL ANTENNAS BY USING TEK SCREWS

EXISTING SIGN SECURED TO TELSTRA EQUIPMENT SHELTER DOOR BY USING TEK SCREWS

NOTE: ANY GANTRY TRAY COVERS SHOWING SIGNS OF SIGNIFICANT WEAR AND TEAR SHALL BE REPLACED WITH NEW COVERS

EXISTING TELSTRA WCDMA850/LTE700/NR850/LTE1800 PANEL ANTENNAS (3 OFF A1, A5 & A9) TO BE RECOVERED.  
EXISTING TELSTRA LTE700/NR850/NR/LTE2600 PANEL ANTENNAS (3 OFF A3, A7 & A11) TO BE RECOVERED.  
EXISTING TELSTRA NR3600 PANEL ANTENNAS (3 OFF A4, A8 & A14) TO BE RECOVERED.  
EXISTING TELSTRA SPARE PANEL ANTENNAS (4 OFF A2, A6, A10 & A12) TO BE RECOVERED.  
EXISTING TELSTRA NR/LTE2600 RRU 32 B7 (3 OFF) TO BE RECOVERED.  
EXISTING TELSTRA LTE1800 RRU 32 B3 (3 OFF) TO BE RECOVERED.  
EXISTING TELSTRA WCDMA850/NR850/LTE700 TMA'S (3 OFF) TO BE RECOVERED.  
EXISTING TELSTRA NR850/LTE700 TMA'S (3 OFF) TO BE RECOVERED.

EXISTING TELSTRA 300W CABLE TRAY ACCOMMODATING EXISTING TELSTRA RFS LCF78-50JA FEEDER CABLES (6 OFF), RFS LCF78-50J FEEDER CABLES (6 OFF) TO BE REUSED FOR LTE700/NR850. EXISTING TELSTRA W&B HYBRID CABLES (3 OFF) TO BE REUSED FOR LTE1800 /LTE2100/NR/LTE2600/NR3600. EXISTING TELSTRA ANDREW LDF5-50 CABLES (6 OFF) TO MAKE AS SPARE

PROPOSED SIGNS UV STABLE STICKERS AND FIXED TO REAR OF ALL TELSTRA PANEL ANTENNAS

- E.L. 27.84m (±100mm) R.L. 58.92m A.H.D  
OVERALL HEIGHT
- E.L. 26.3m (±100mm) R.L. 57.38m A.H.D  
C/L PROPOSED TELSTRA NR3600 PANEL ANTENNAS (3 OFF A4, A8 & A14)  
C/L PROPOSED TELSTRA LTE700/NR850 TMA'S (2 OFF) @ S1 & S3
- E.L. 25.9m (±100mm) R.L. 56.98m A.H.D  
C/L PROPOSED TELSTRA LTE700/NR850 TMA (1 OFF) @ S2
- E.L. 25.4m (±100mm) R.L. 56.48m A.H.D  
C/L PROPOSED TELSTRA LTE700/NR850/LTE1800/LTE2100/NR/LTE2600 PANEL ANTENNAS (3 OFF A1, A5 & A9)
- E.L. 25.2m (±100mm) R.L. 56.38m A.H.D  
C/L PROPOSED TELSTRA LTE700/NR850 TMA'S (2 OFF) @ S1 & S3
- E.L. 25.1m (±100mm) R.L. 56.28m A.H.D  
C/L PROPOSED TELSTRA LTE1800/LTE2100/NR/LTE2600 RADIO 4485 B3/B1/B7 (3 OFF) @ S1, S2 & S3  
C/L PROPOSED TELSTRA LTE700/NR850 TMA (1 OFF) @ S2
- E.L. 24.40m (±100mm) R.L. 55.48m A.H.D  
BASE OF PROPOSED TELSTRA TELSTRA KA-7005-1110 GPS ANTENNA (1 OFF A15)
- E.L. 22.20m (±100mm) R.L. 53.28m A.H.D  
C/L EXISTING TELSTRA W&B RRU INTERFACE JUNCTION BOX (1 OFF) (SECTOR 2)
- E.L. 22.00m (±100mm) R.L. 53.08m A.H.D  
C/L EXISTING TELSTRA W&B RRU INTERFACE JUNCTION BOX (1 OFF) (SECTOR 3)
- E.L. 21.90m (±100mm) R.L. 52.98m A.H.D  
C/L EXISTING TELSTRA W&B RRU INTERFACE JUNCTION BOX (1 OFF) (SECTOR 1)
- E.L. 21.5m (±100mm) R.L. 52.58m A.H.D  
TOP OF ROOF PARAPET
- E.L. 21.0m (±100mm) R.L. 52.08m A.H.D  
TOP OF ROOF SLAB

UNAPPROVED  
DRAWING

COMPLIANCE BOX  
COMPLETED AS PER DESIGN  
ALTERATIONS IN RED  
NAME (PRINT)  
SIGNATURE  
DATE

SOUTH ELEVATION


SCALE 1:150  
1.5m 0 1.5m 3m 4.5m 6m 7.5m SCALE 1:150

NOTE: THIS DRAWING TO BE READ IN CONJUNCTION WITH SHEETS S3, S3-2 & S3-3

FOR CONSTRUCTION

DO NOT  
SCALE

F

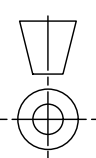

- NOTES:
- ALL EXTERNAL FEEDERS AND TAILS MUST BE BIRD PROOFED AS PER EXTERNAL PLANT POLICY 003615.
  - FOR SITE SPECIFIC NOTES REFER TO SHEETS S0, S0-1 & S0-2.
  - FOR EME SIGNS NOTED THUS (#X) REFER TO 005486 FOR DETAILS.
  - ALL DIMENSIONS ARE IN MILLIMETRES UNLESS OTHERWISE STATED.




| ORDER      | DRWN | CHKD | AMENDMENT                                             | EXAM | APPD | DATE     | ISS |
|------------|------|------|-------------------------------------------------------|------|------|----------|-----|
| NA15095.01 | SB   | SB   | AS BUILT 7267045 W0001 LTE700                         | SB   | BB   | 21.11.14 | 10  |
| NA17236.01 | MS   | LY   | AS BUILT - 30060257W0071ERIC - RRU AND LTE2600 UPDATE | KSK  | CF   | 09.05.17 | 11  |
| NA21231.01 | SH   | JG   | FOR CONSTRUCTION 30084274 W0267 5G NR3600             | MWM  | MWM  | 30.04.20 | 12  |
| NA21231.01 | UH   | RM   | AS BUILT - 30084274 W0315 - NR3600                    | DEG  | DEG  | 11.08.20 | 13  |
| NA23527.01 | LB   | WR   | AS BUILT - 30092852W0195ERIC - M700/NR850/DSS26       | PD   | DEG  | 09.02.22 | 14  |
| NA25797.01 | RS   | RT   | FOR CONSTRUCTION - 80005689W0540CYI - LTE2100         | MB   | MB   | 21.05.26 | 15  |

© Telstra Limited ACN 086 174 781 All rights reserved.



MOBILE NETWORK SITE 40893  
CAMPERDOWN RYDGES MISSENDEN RD  
SOUTH ELEVATION  
9 MISSENDEN RD, CAMPERDOWN, NSW 2050

DWG NO. N26167 SHT NO. S3-1

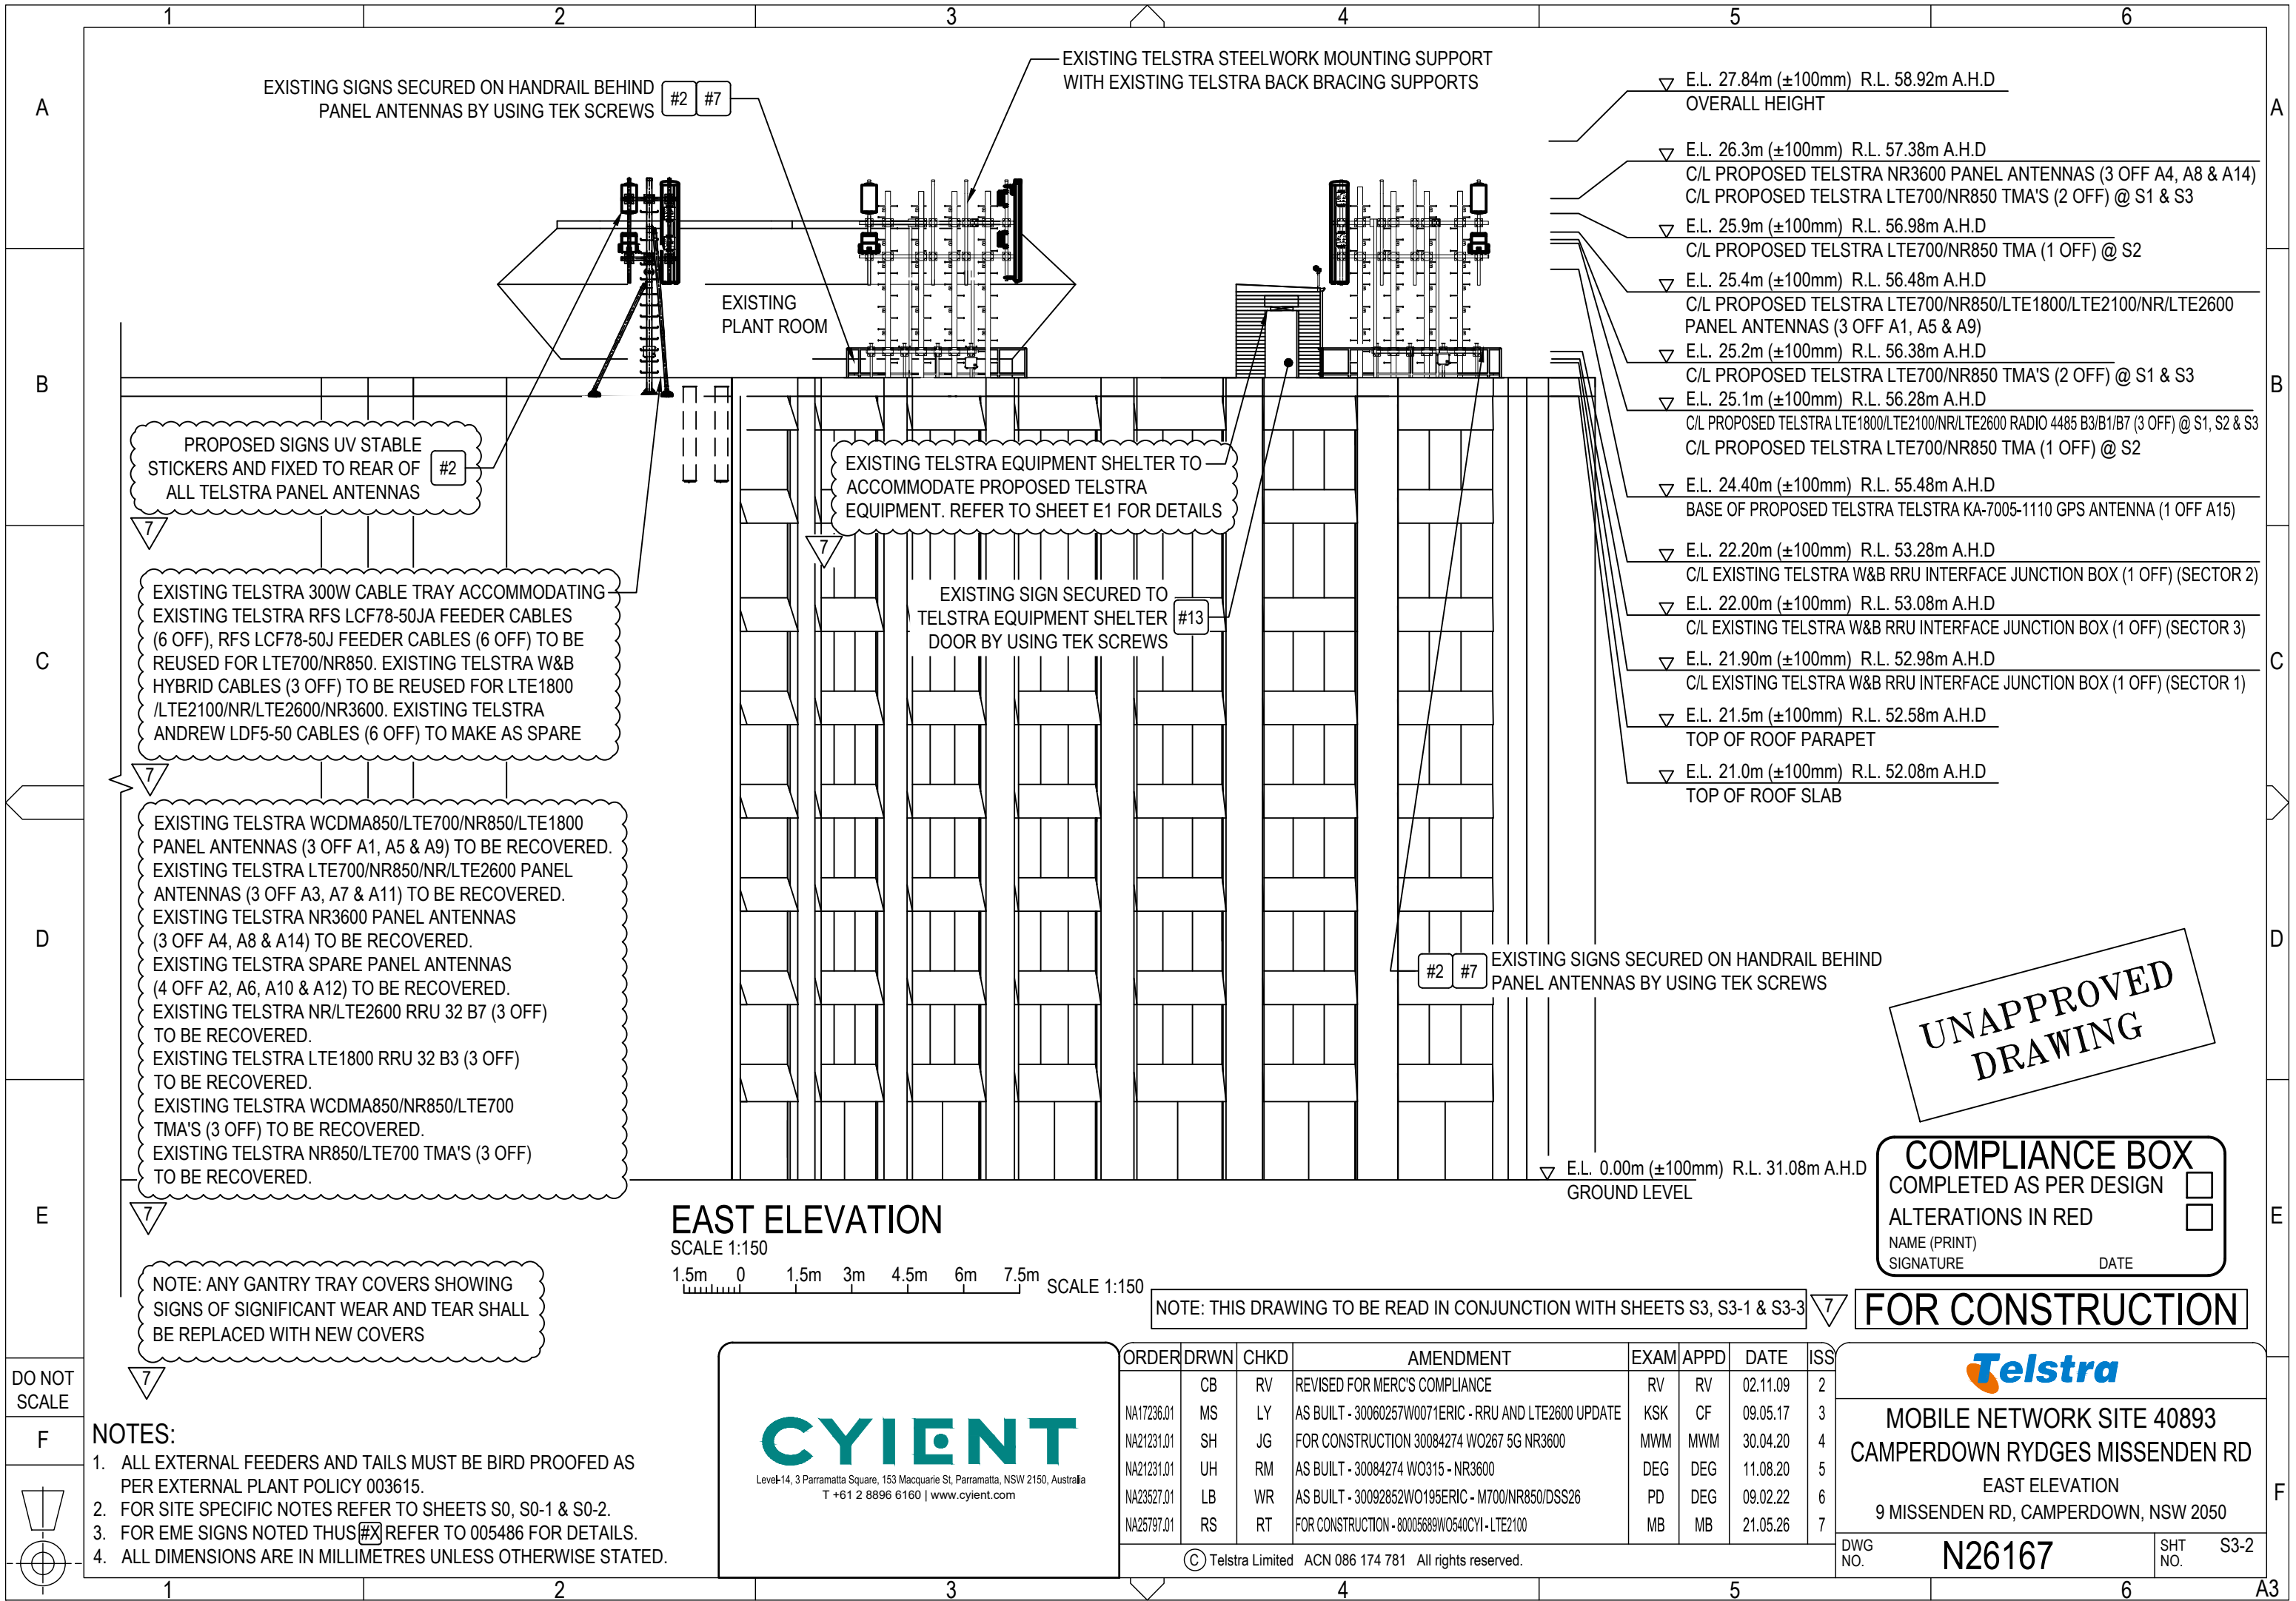

EXISTING SIGNS SECURED ON HANDRAIL BEHIND  
PANEL ANTENNAS BY USING TEK SCREWS

EXISTING TELSTRA STEELWORK MOUNTING SUPPORT  
WITH EXISTING TELSTRA BACK BRACING SUPPORTS

EXISTING  
PLANT ROOM

PROPOSED SIGNS UV STABLE  
STICKERS AND FIXED TO REAR OF  
ALL TELSTRA PANEL ANTENNAS

EXISTING TELSTRA EQUIPMENT SHELTER TO  
ACCOMMODATE PROPOSED TELSTRA  
EQUIPMENT. REFER TO SHEET E1 FOR DETAILS

EXISTING TELSTRA 300W CABLE TRAY ACCOMMODATING  
EXISTING TELSTRA RFS LCF78-50JA FEEDER CABLES  
(6 OFF), RFS LCF78-50J FEEDER CABLES (6 OFF) TO BE  
REUSED FOR LTE700/NR850. EXISTING TELSTRA W&B  
HYBRID CABLES (3 OFF) TO BE REUSED FOR LTE1800  
/LTE2100/NR/LTE2600/NR3600. EXISTING TELSTRA  
ANDREW LDF5-50 CABLES (6 OFF) TO MAKE AS SPARE

EXISTING TELSTRA WCDMA850/LTE700/NR850/LTE1800  
PANEL ANTENNAS (3 OFF A1, A5 & A9) TO BE RECOVERED.  
EXISTING TELSTRA LTE700/NR850/NR/LTE2600 PANEL  
ANTENNAS (3 OFF A3, A7 & A11) TO BE RECOVERED.  
EXISTING TELSTRA NR3600 PANEL ANTENNAS  
(3 OFF A4, A8 & A14) TO BE RECOVERED.  
EXISTING TELSTRA SPARE PANEL ANTENNAS  
(4 OFF A2, A6, A10 & A12) TO BE RECOVERED.  
EXISTING TELSTRA NR/LTE2600 RRU 32 B7 (3 OFF)  
TO BE RECOVERED.  
EXISTING TELSTRA LTE1800 RRU 32 B3 (3 OFF)  
TO BE RECOVERED.  
EXISTING TELSTRA WCDMA850/NR850/LTE700  
TMA'S (3 OFF) TO BE RECOVERED.  
EXISTING TELSTRA NR850/LTE700 TMA'S (3 OFF)  
TO BE RECOVERED.

NOTE: ANY GANTRY TRAY COVERS SHOWING  
SIGNS OF SIGNIFICANT WEAR AND TEAR SHALL  
BE REPLACED WITH NEW COVERS

EXISTING SIGN SECURED TO  
TELSTRA EQUIPMENT SHELTER  
DOOR BY USING TEK SCREWS

EXISTING SIGNS SECURED ON HANDRAIL BEHIND  
PANEL ANTENNAS BY USING TEK SCREWS

- ▽ E.L. 27.84m (±100mm) R.L. 58.92m A.H.D  
OVERALL HEIGHT
- ▽ E.L. 26.3m (±100mm) R.L. 57.38m A.H.D  
C/L PROPOSED TELSTRA NR3600 PANEL ANTENNAS (3 OFF A4, A8 & A14)  
C/L PROPOSED TELSTRA LTE700/NR850 TMA'S (2 OFF) @ S1 & S3
- ▽ E.L. 25.9m (±100mm) R.L. 56.98m A.H.D  
C/L PROPOSED TELSTRA LTE700/NR850 TMA (1 OFF) @ S2
- ▽ E.L. 25.4m (±100mm) R.L. 56.48m A.H.D  
C/L PROPOSED TELSTRA LTE700/NR850/LTE1800/LTE2100/NR/LTE2600  
PANEL ANTENNAS (3 OFF A1, A5 & A9)
- ▽ E.L. 25.2m (±100mm) R.L. 56.38m A.H.D  
C/L PROPOSED TELSTRA LTE700/NR850 TMA'S (2 OFF) @ S1 & S3
- ▽ E.L. 25.1m (±100mm) R.L. 56.28m A.H.D  
C/L PROPOSED TELSTRA LTE1800/LTE2100/NR/LTE2600 RADIO 4485 B3/B1/B7 (3 OFF) @ S1, S2 & S3  
C/L PROPOSED TELSTRA LTE700/NR850 TMA (1 OFF) @ S2
- ▽ E.L. 24.40m (±100mm) R.L. 55.48m A.H.D  
BASE OF PROPOSED TELSTRA TELSTRA KA-7005-1110 GPS ANTENNA (1 OFF A15)
- ▽ E.L. 22.20m (±100mm) R.L. 53.28m A.H.D  
C/L EXISTING TELSTRA W&B RRU INTERFACE JUNCTION BOX (1 OFF) (SECTOR 2)
- ▽ E.L. 22.00m (±100mm) R.L. 53.08m A.H.D  
C/L EXISTING TELSTRA W&B RRU INTERFACE JUNCTION BOX (1 OFF) (SECTOR 3)
- ▽ E.L. 21.90m (±100mm) R.L. 52.98m A.H.D  
C/L EXISTING TELSTRA W&B RRU INTERFACE JUNCTION BOX (1 OFF) (SECTOR 1)
- ▽ E.L. 21.5m (±100mm) R.L. 52.58m A.H.D  
TOP OF ROOF PARAPET
- ▽ E.L. 21.0m (±100mm) R.L. 52.08m A.H.D  
TOP OF ROOF SLAB

EAST ELEVATION

SCALE 1:150  
1.5m 0 1.5m 3m 4.5m 6m 7.5m

NOTE: THIS DRAWING TO BE READ IN CONJUNCTION WITH SHEETS S3, S3-1 & S3-3

UNAPPROVED  
DRAWING

COMPLIANCE BOX  
COMPLETED AS PER DESIGN ☐  
ALTERATIONS IN RED ☐  
NAME (PRINT) \_\_\_\_\_  
SIGNATURE \_\_\_\_\_ DATE \_\_\_\_\_

FOR CONSTRUCTION

DO NOT  
SCALE

- NOTES:
- ALL EXTERNAL FEEDERS AND TAILS MUST BE BIRD PROOFED AS PER EXTERNAL PLANT POLICY 003615.
  - FOR SITE SPECIFIC NOTES REFER TO SHEETS S0, S0-1 & S0-2.
  - FOR EME SIGNS NOTED THUS (#X) REFER TO 005486 FOR DETAILS.
  - ALL DIMENSIONS ARE IN MILLIMETRES UNLESS OTHERWISE STATED.



Level 14, 3 Parramatta Square, 153 Macquarie St, Parramatta, NSW 2150, Australia  
T +61 2 8896 6160 | www.cyient.com


| ORDER      | DRWN | CHKD | AMENDMENT                                             | EXAM | APPD | DATE     | ISS |
|------------|------|------|-------------------------------------------------------|------|------|----------|-----|
| NA17236.01 | CB   | RV   | REVISED FOR MERC'S COMPLIANCE                         | RV   | RV   | 02.11.09 | 2   |
| NA21231.01 | MS   | LY   | AS BUILT - 30060257W0071ERIC - RRU AND LTE2600 UPDATE | KSK  | CF   | 09.05.17 | 3   |
| NA21231.01 | SH   | JG   | FOR CONSTRUCTION 30084274 WO267 5G NR3600             | MWM  | MWM  | 30.04.20 | 4   |
| NA21231.01 | UH   | RM   | AS BUILT - 30084274 WO315 - NR3600                    | DEG  | DEG  | 11.08.20 | 5   |
| NA23527.01 | LB   | WR   | AS BUILT - 30092852WO195ERIC - M700/NR850/DSS26       | PD   | DEG  | 09.02.22 | 6   |
| NA25797.01 | RS   | RT   | FOR CONSTRUCTION - 80005689W0540CYI - LTE2100         | MB   | MB   | 21.05.26 | 7   |

© Telstra Limited ACN 086 174 781 All rights reserved.




MOBILE NETWORK SITE 40893  
CAMPERDOWN RYDGES MISSENDEN RD  
EAST ELEVATION  
9 MISSENDEN RD, CAMPERDOWN, NSW 2050

DWG NO. N26167 SHT NO. S3-2

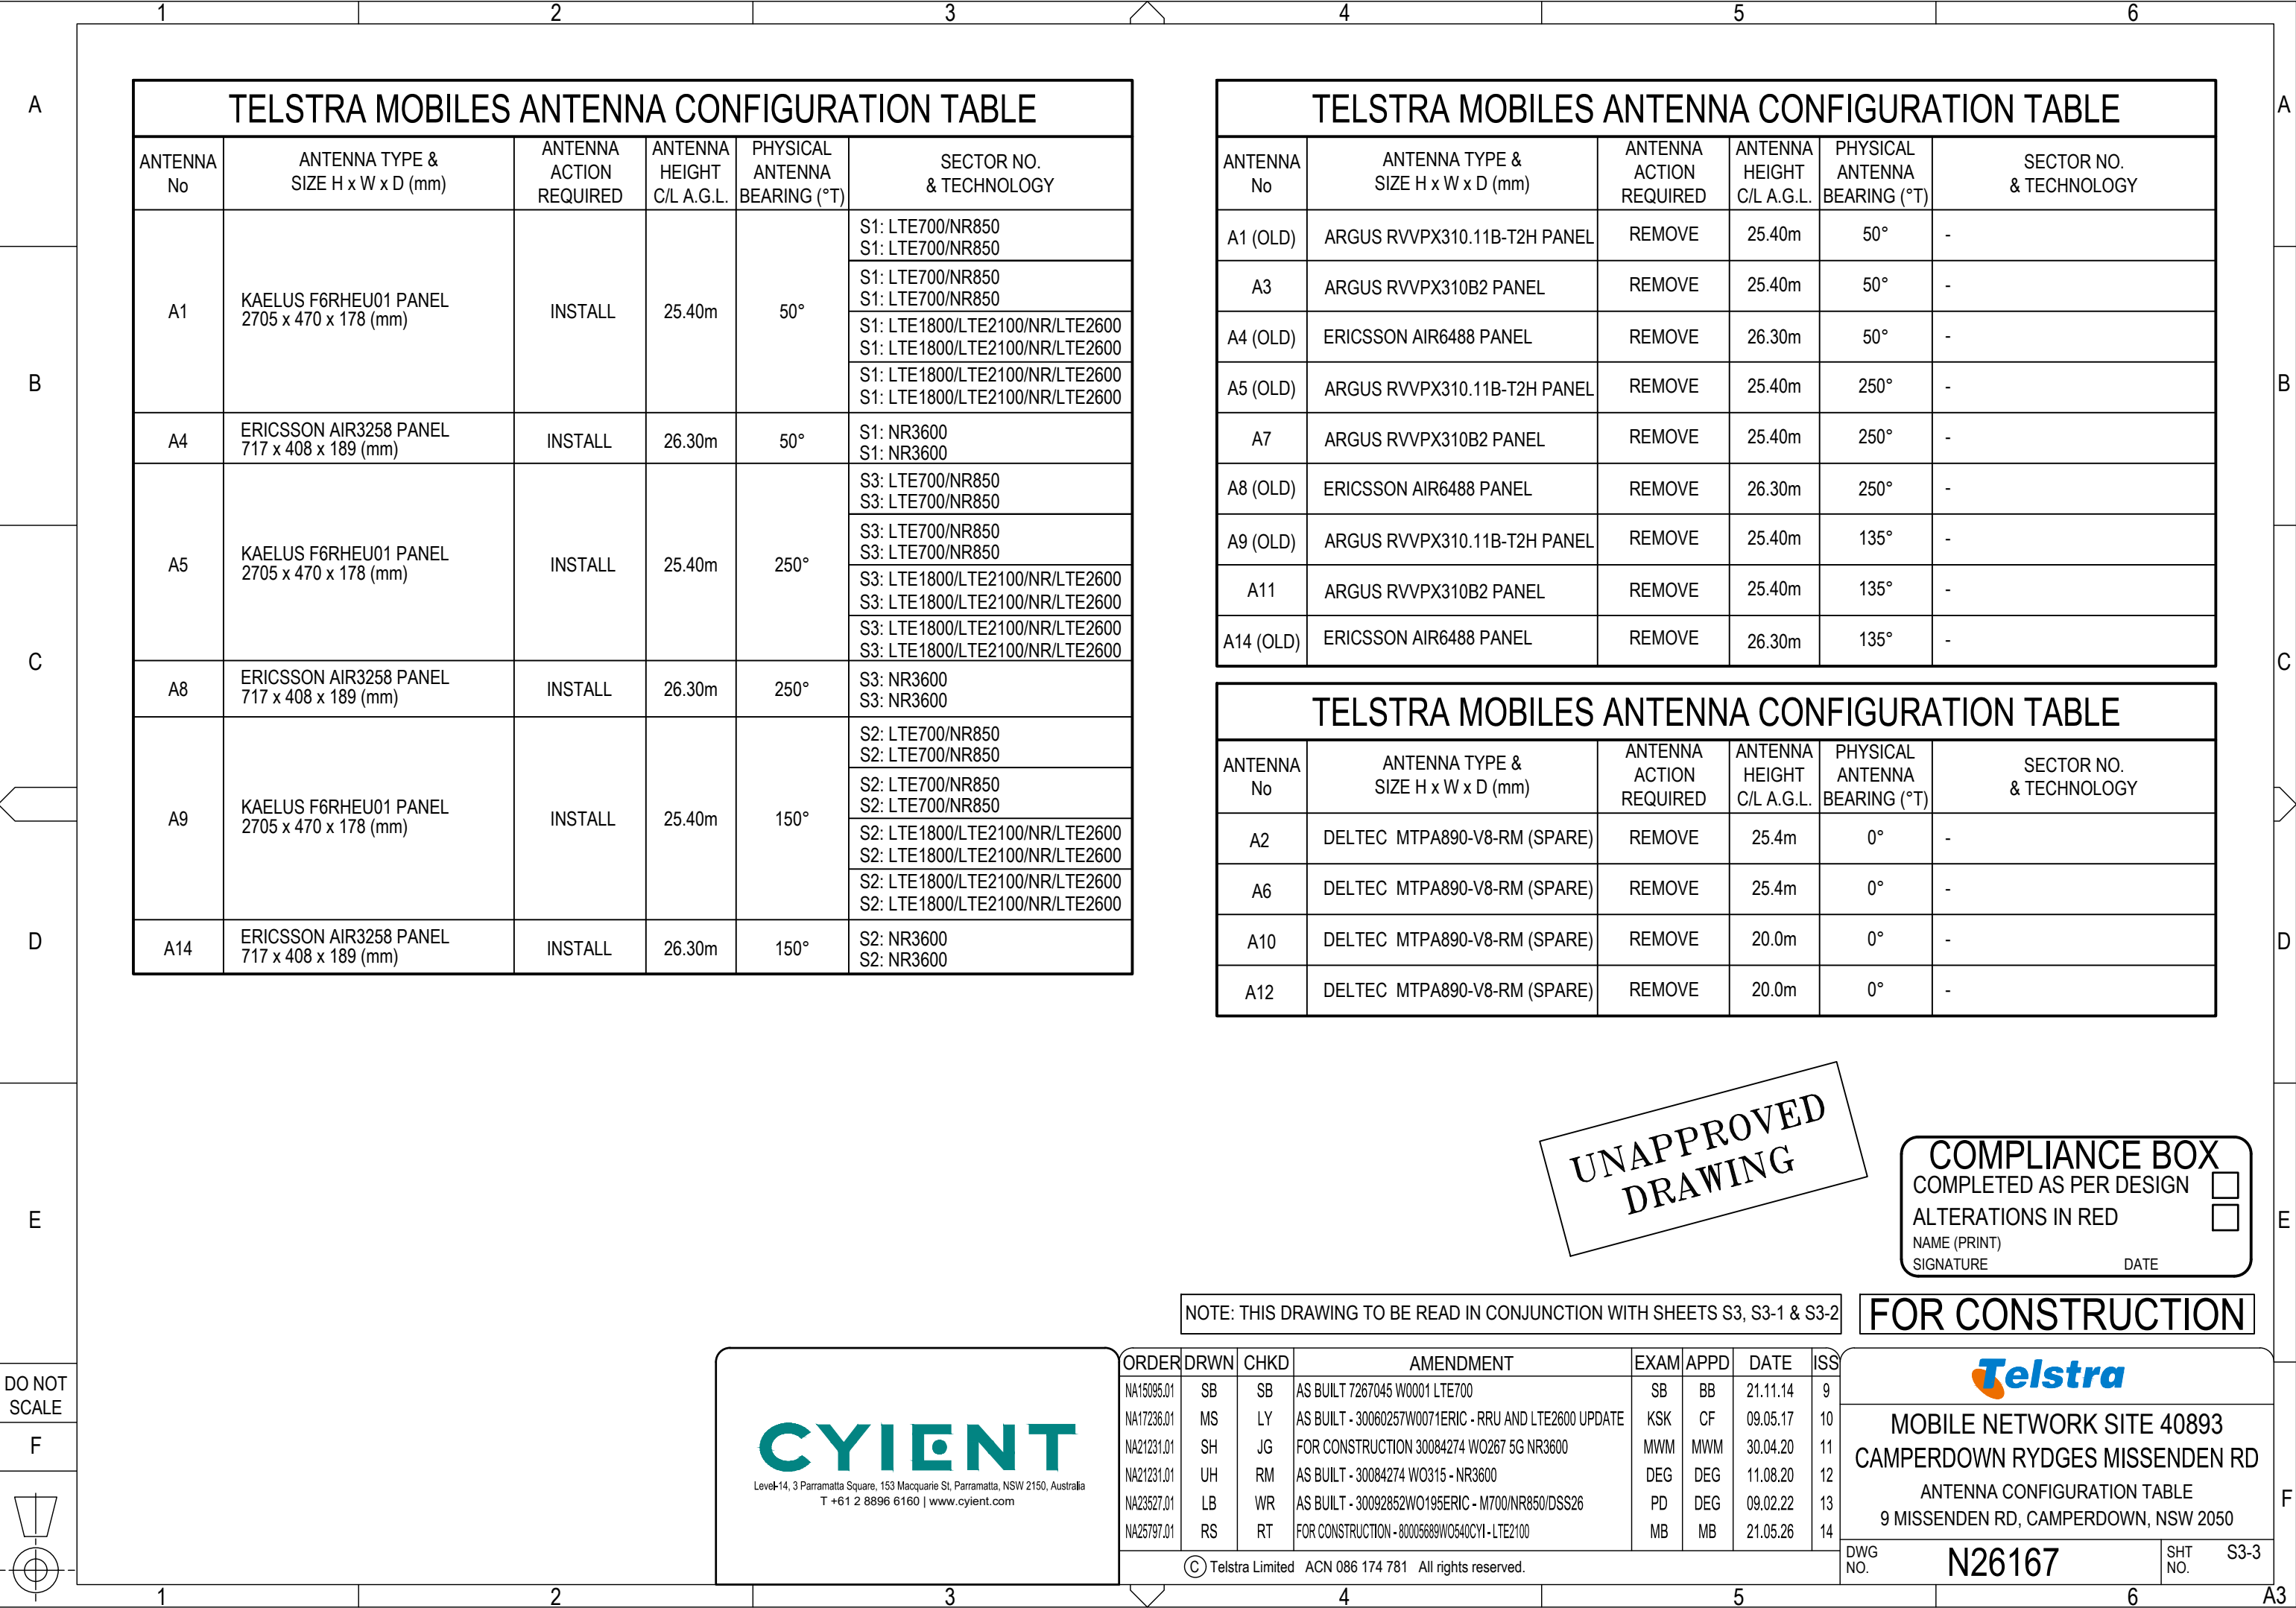



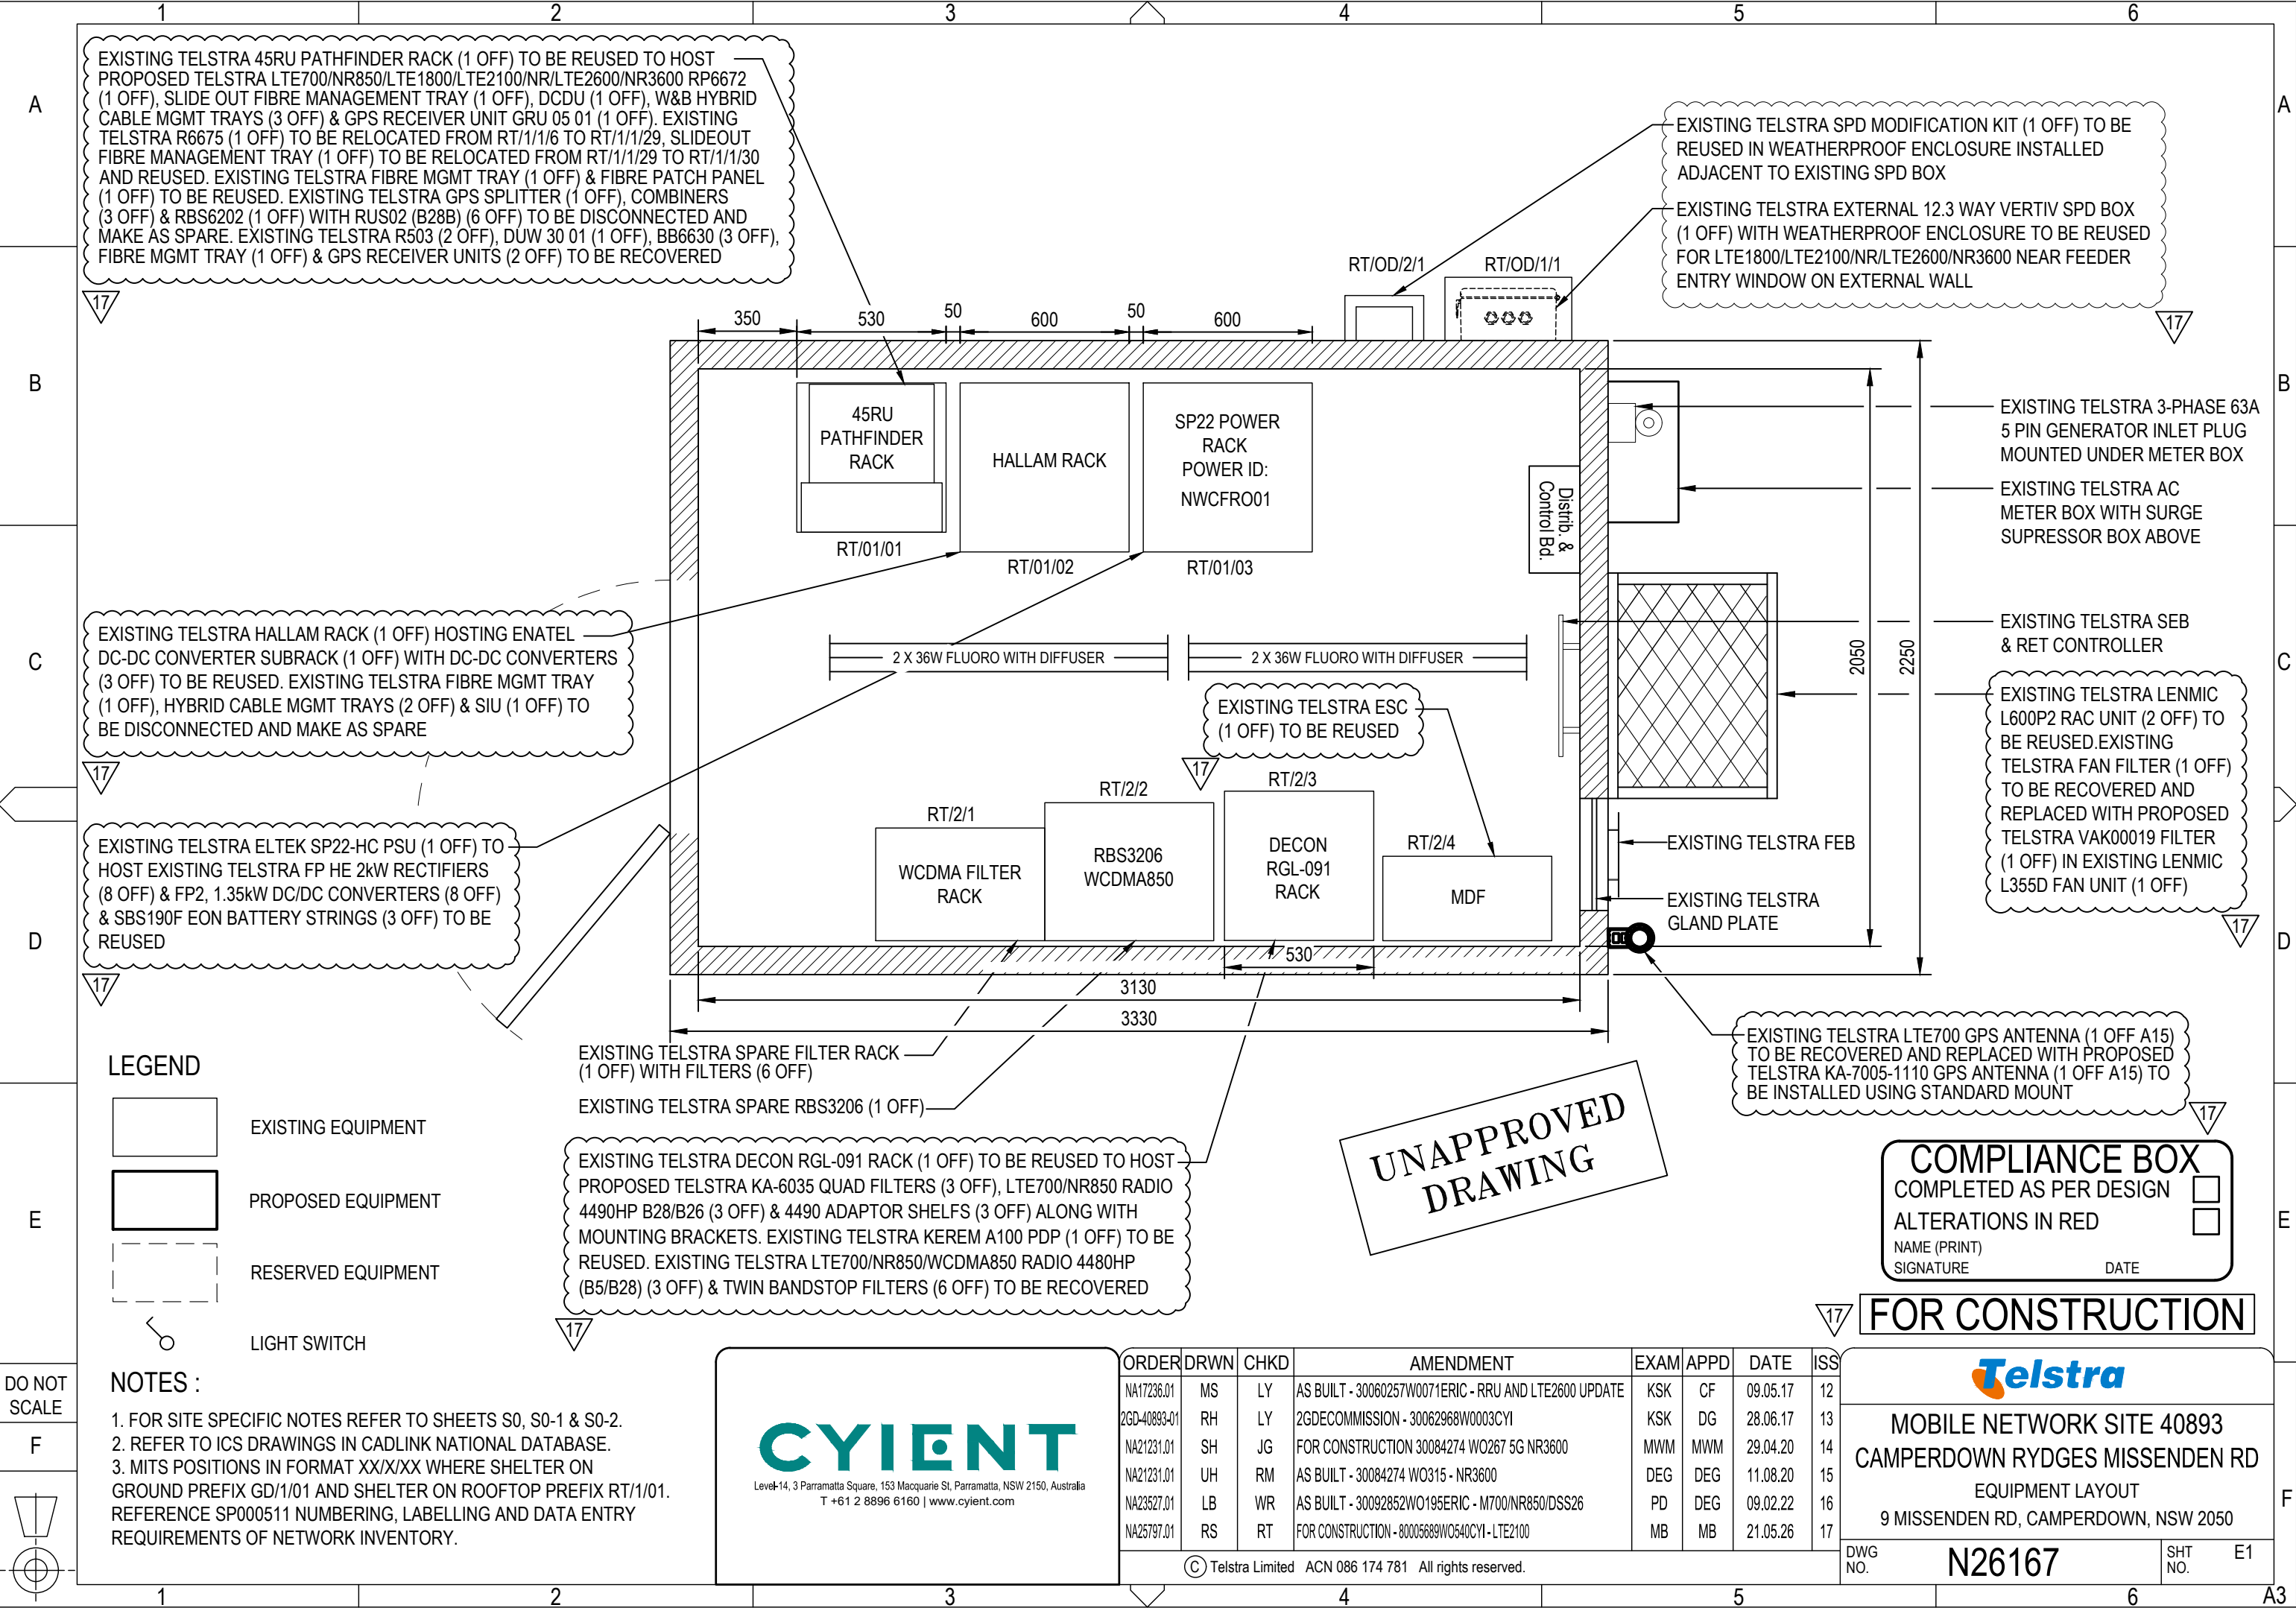

EXISTING TELSTRA 45RU PATHFINDER RACK (1 OFF) TO BE REUSED TO HOST PROPOSED TELSTRA LTE700/NR850/LTE1800/LTE2100/NR/LTE2600/NR3600 RP6672 (1 OFF), SLIDE OUT FIBRE MANAGEMENT TRAY (1 OFF), DCDU (1 OFF), W&B HYBRID CABLE MGMT TRAYS (3 OFF) & GPS RECEIVER UNIT GRU 05 01 (1 OFF). EXISTING TELSTRA R6675 (1 OFF) TO BE RELOCATED FROM RT/1/1/6 TO RT/1/1/29, SLIDEOUT FIBRE MANAGEMENT TRAY (1 OFF) TO BE RELOCATED FROM RT/1/1/29 TO RT/1/1/30 AND REUSED. EXISTING TELSTRA FIBRE MGMT TRAY (1 OFF) & FIBRE PATCH PANEL (1 OFF) TO BE REUSED. EXISTING TELSTRA GPS SPLITTER (1 OFF), COMBINERS (3 OFF) & RBS6202 (1 OFF) WITH RUS02 (B28B) (6 OFF) TO BE DISCONNECTED AND MAKE AS SPARE. EXISTING TELSTRA R503 (2 OFF), DUW 30 01 (1 OFF), BB6630 (3 OFF), FIBRE MGMT TRAY (1 OFF) & GPS RECEIVER UNITS (2 OFF) TO BE RECOVERED

EXISTING TELSTRA SPD MODIFICATION KIT (1 OFF) TO BE REUSED IN WEATHERPROOF ENCLOSURE INSTALLED ADJACENT TO EXISTING SPD BOX  
EXISTING TELSTRA EXTERNAL 12.3 WAY VERTIV SPD BOX (1 OFF) WITH WEATHERPROOF ENCLOSURE TO BE REUSED FOR LTE1800/LTE2100/NR/LTE2600/NR3600 NEAR FEEDER ENTRY WINDOW ON EXTERNAL WALL

EXISTING TELSTRA HALLAM RACK (1 OFF) HOSTING ENATEL DC-DC CONVERTER SUBRACK (1 OFF) WITH DC-DC CONVERTERS (3 OFF) TO BE REUSED. EXISTING TELSTRA FIBRE MGMT TRAY (1 OFF), HYBRID CABLE MGMT TRAYS (2 OFF) & SIU (1 OFF) TO BE DISCONNECTED AND MAKE AS SPARE

EXISTING TELSTRA ELTEK SP22-HC PSU (1 OFF) TO HOST EXISTING TELSTRA FP HE 2kW RECTIFIERS (8 OFF) & FP2, 1.35kW DC/DC CONVERTERS (8 OFF) & SBS190F EON BATTERY STRINGS (3 OFF) TO BE REUSED

EXISTING TELSTRA 3-PHASE 63A 5 PIN GENERATOR INLET PLUG MOUNTED UNDER METER BOX  
EXISTING TELSTRA AC METER BOX WITH SURGE SUPPRESSOR BOX ABOVE  
EXISTING TELSTRA SEB & RET CONTROLLER  
EXISTING TELSTRA LENMIC L600P2 RAC UNIT (2 OFF) TO BE REUSED. EXISTING TELSTRA FAN FILTER (1 OFF) TO BE RECOVERED AND REPLACED WITH PROPOSED TELSTRA VAK00019 FILTER (1 OFF) IN EXISTING LENMIC L355D FAN UNIT (1 OFF)

EXISTING TELSTRA LTE700 GPS ANTENNA (1 OFF A15) TO BE RECOVERED AND REPLACED WITH PROPOSED TELSTRA KA-7005-1110 GPS ANTENNA (1 OFF A15) TO BE INSTALLED USING STANDARD MOUNT

EXISTING TELSTRA SPARE FILTER RACK (1 OFF) WITH FILTERS (6 OFF)  
EXISTING TELSTRA SPARE RBS3206 (1 OFF)

EXISTING TELSTRA DECON RGL-091 RACK (1 OFF) TO BE REUSED TO HOST PROPOSED TELSTRA KA-6035 QUAD FILTERS (3 OFF), LTE700/NR850 RADIO 4490HP B28/B26 (3 OFF) & 4490 ADAPTOR SHELF (3 OFF) ALONG WITH MOUNTING BRACKETS. EXISTING TELSTRA KEREM A100 PDP (1 OFF) TO BE REUSED. EXISTING TELSTRA LTE700/NR850/WCDMA850 RADIO 4480HP (B5/B28) (3 OFF) & TWIN BANDSTOP FILTERS (6 OFF) TO BE RECOVERED

UNAPPROVED  
DRAWING

COMPLIANCE BOX

COMPLETED AS PER DESIGN

ALTERATIONS IN RED

NAME (PRINT)

SIGNATURE

DATE

FOR CONSTRUCTION

LEGEND

EXISTING EQUIPMENT

PROPOSED EQUIPMENT

RESERVED EQUIPMENT

LIGHT SWITCH

NOTES :

1. FOR SITE SPECIFIC NOTES REFER TO SHEETS S0, S0-1 & S0-2.

2. REFER TO ICS DRAWINGS IN CADLINK NATIONAL DATABASE.

3. MITS POSITIONS IN FORMAT XX/X/XX WHERE SHELTER ON GROUND PREFIX GD/1/01 AND SHELTER ON ROOFTOP PREFIX RT/1/01. REFERENCE SP000511 NUMBERING, LABELLING AND DATA ENTRY REQUIREMENTS OF NETWORK INVENTORY.

CYIENT

Level 14, 3 Parramatta Square, 153 Macquarie St, Parramatta, NSW 2150, Australia

T +61 2 8896 6160 | www.cyient.com

| ORDER        | DRWN | CHKD | AMENDMENT                                             | EXAM | APPD | DATE     | ISS |
|--------------|------|------|-------------------------------------------------------|------|------|----------|-----|
| NA17236.01   | MS   | LY   | AS BUILT - 30060257W0071ERIC - RRU AND LTE2600 UPDATE | KSK  | CF   | 09.05.17 | 12  |
| 2GD-40893-01 | RH   | LY   | 2GDECOMMISSION - 30062968W0003CYI                     | KSK  | DG   | 28.06.17 | 13  |
| NA21231.01   | SH   | JG   | FOR CONSTRUCTION 30084274 WO267 5G NR3600             | MWM  | MWM  | 29.04.20 | 14  |
| NA21231.01   | UH   | RM   | AS BUILT - 30084274 WO315 - NR3600                    | DEG  | DEG  | 11.08.20 | 15  |
| NA23527.01   | LB   | WR   | AS BUILT - 30092852WO195ERIC - M700/NR850/DSS26       | PD   | DEG  | 09.02.22 | 16  |
| NA25797.01   | RS   | RT   | FOR CONSTRUCTION - 800056889W0540CYI - LTE2100        | MB   | MB   | 21.05.26 | 17  |

© Telstra Limited ACN 086 174 781 All rights reserved.

Telstra

MOBILE NETWORK SITE 40893

CAMPERDOWN RYDGES MISSENDEN RD

EQUIPMENT LAYOUT


9 MISSENDEN RD, CAMPERDOWN, NSW 2050

DWG NO.


N26167

SHT NO.

E1

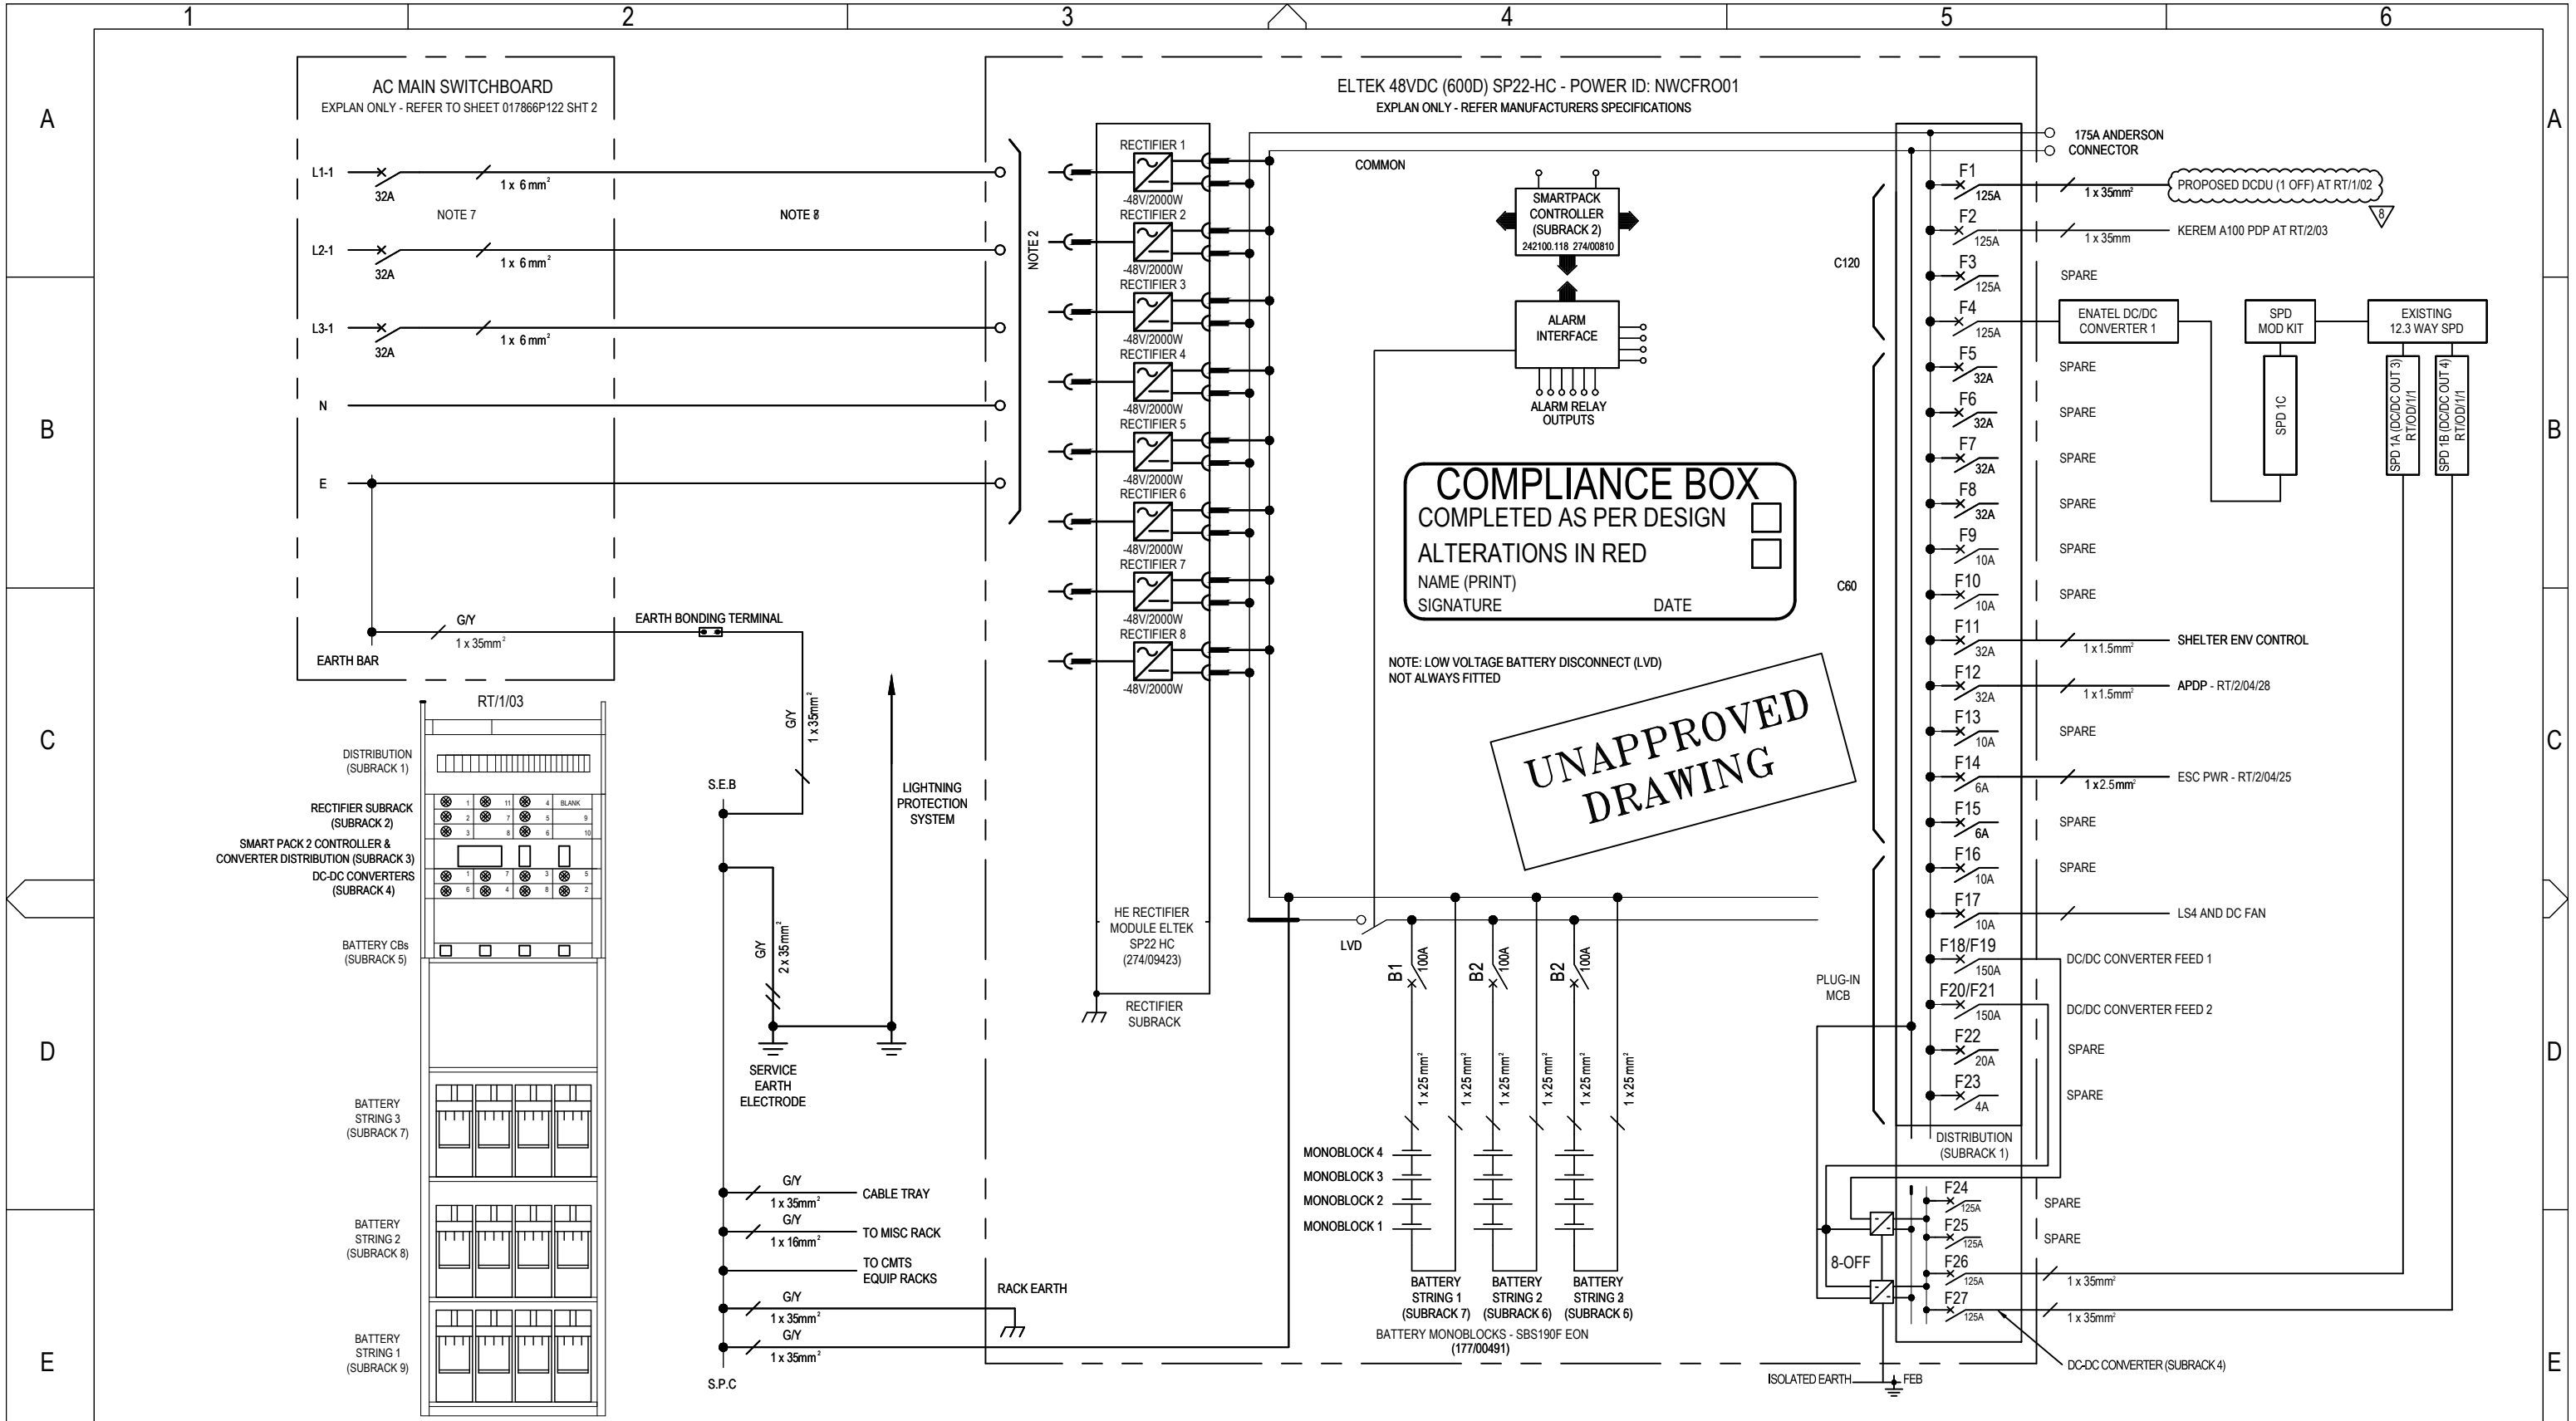

|   |  |   |  |              |  |      |      |                                                       |  |      |      |          |     |   |  |            |
|---|--|---|--|--------------|--|------|------|-------------------------------------------------------|--|------|------|----------|-----|---|--|------------|
| NOTES:   |  | RT/1/3   |  |              |  | 8    |      | FOR CONSTRUCTION                                      |  |      |      |          |     |   |  |            |
| <div>DO NOT SCALE</div> <div>F</div> <div></div> |  | <div>CYIENT</div> <div>Level 14, 3 Parramatta Square, 153 Macquarie St, Parramatta, NSW 2150, Australia</div> <div>T +61 2 8896 6160   www.cyient.com</div> |  | ORDER        |  | DRWN | CHKD | AMENDMENT                                             |  | EXAM | APPD | DATE     | ISS | <div></div> <div>MOBILE NETWORK SITE 40893</div> <div>CAMPERDOWN RYDGES MISSENDEN RD</div> <div>DC POWER LINE DIAGRAM</div> <div>9 MISSENDEN RD, CAMPERDOWN, NSW 2050</div> |  |            |
|   |  |   |  | NA17236.01   |  | MS   | LY   | AS BUILT - 30060257W0071ERIC - RRU AND LTE2600 UPDATE |  | KSK  | CF   | 09.05.17 | 3   |   |  |            |
|   |  |   |  | 2GD-40893-01 |  | RH   | LY   | 2GDECOMMISSION - 30062968W0003CYI                     |  | KSK  | DG   | 28.06.17 | 4   |   |  |            |
|   |  |   |  | NA21231.01   |  | SH   | JG   | FOR CONSTRUCTION 30084274 WO267 5G NR3600             |  | MWM  | MWM  | 30.04.20 | 5   |   |  |            |
| <div>1</div> <div>2</div> <div>3</div> <div>4</div> <div>5</div> <div>6</div> <div>A3</div>                                        |  |   |  | NA21231.01   |  | UH   | RM   | AS BUILT - 30084274 WO315 - NR3600                    |  | DEG  | DEG  | 11.08.20 | 6   | F   |  |            |
|   |  |   |  | NA23527.01   |  | LB   | WR   | AS BUILT - 30092852WO195ERIC - M700/NR850/DSS26       |  | PD   | DEG  | 09.02.22 | 7   |   |  |            |
|   |  |   |  | NA25797.01   |  | RS   | RT   | FOR CONSTRUCTION - 80005689W0540CYI - LTE2100         |  | MB   | MB   | 21.05.26 | 8   |   |  |            |
|   |  |   |  |              |  |      |      |                                                       |  |      |      |          |     |   |  |            |
|   |  |   |  |              |  |      |      |                                                       |  |      |      |          |     | DWG NO. N26167   |  | SHT NO. E4 |

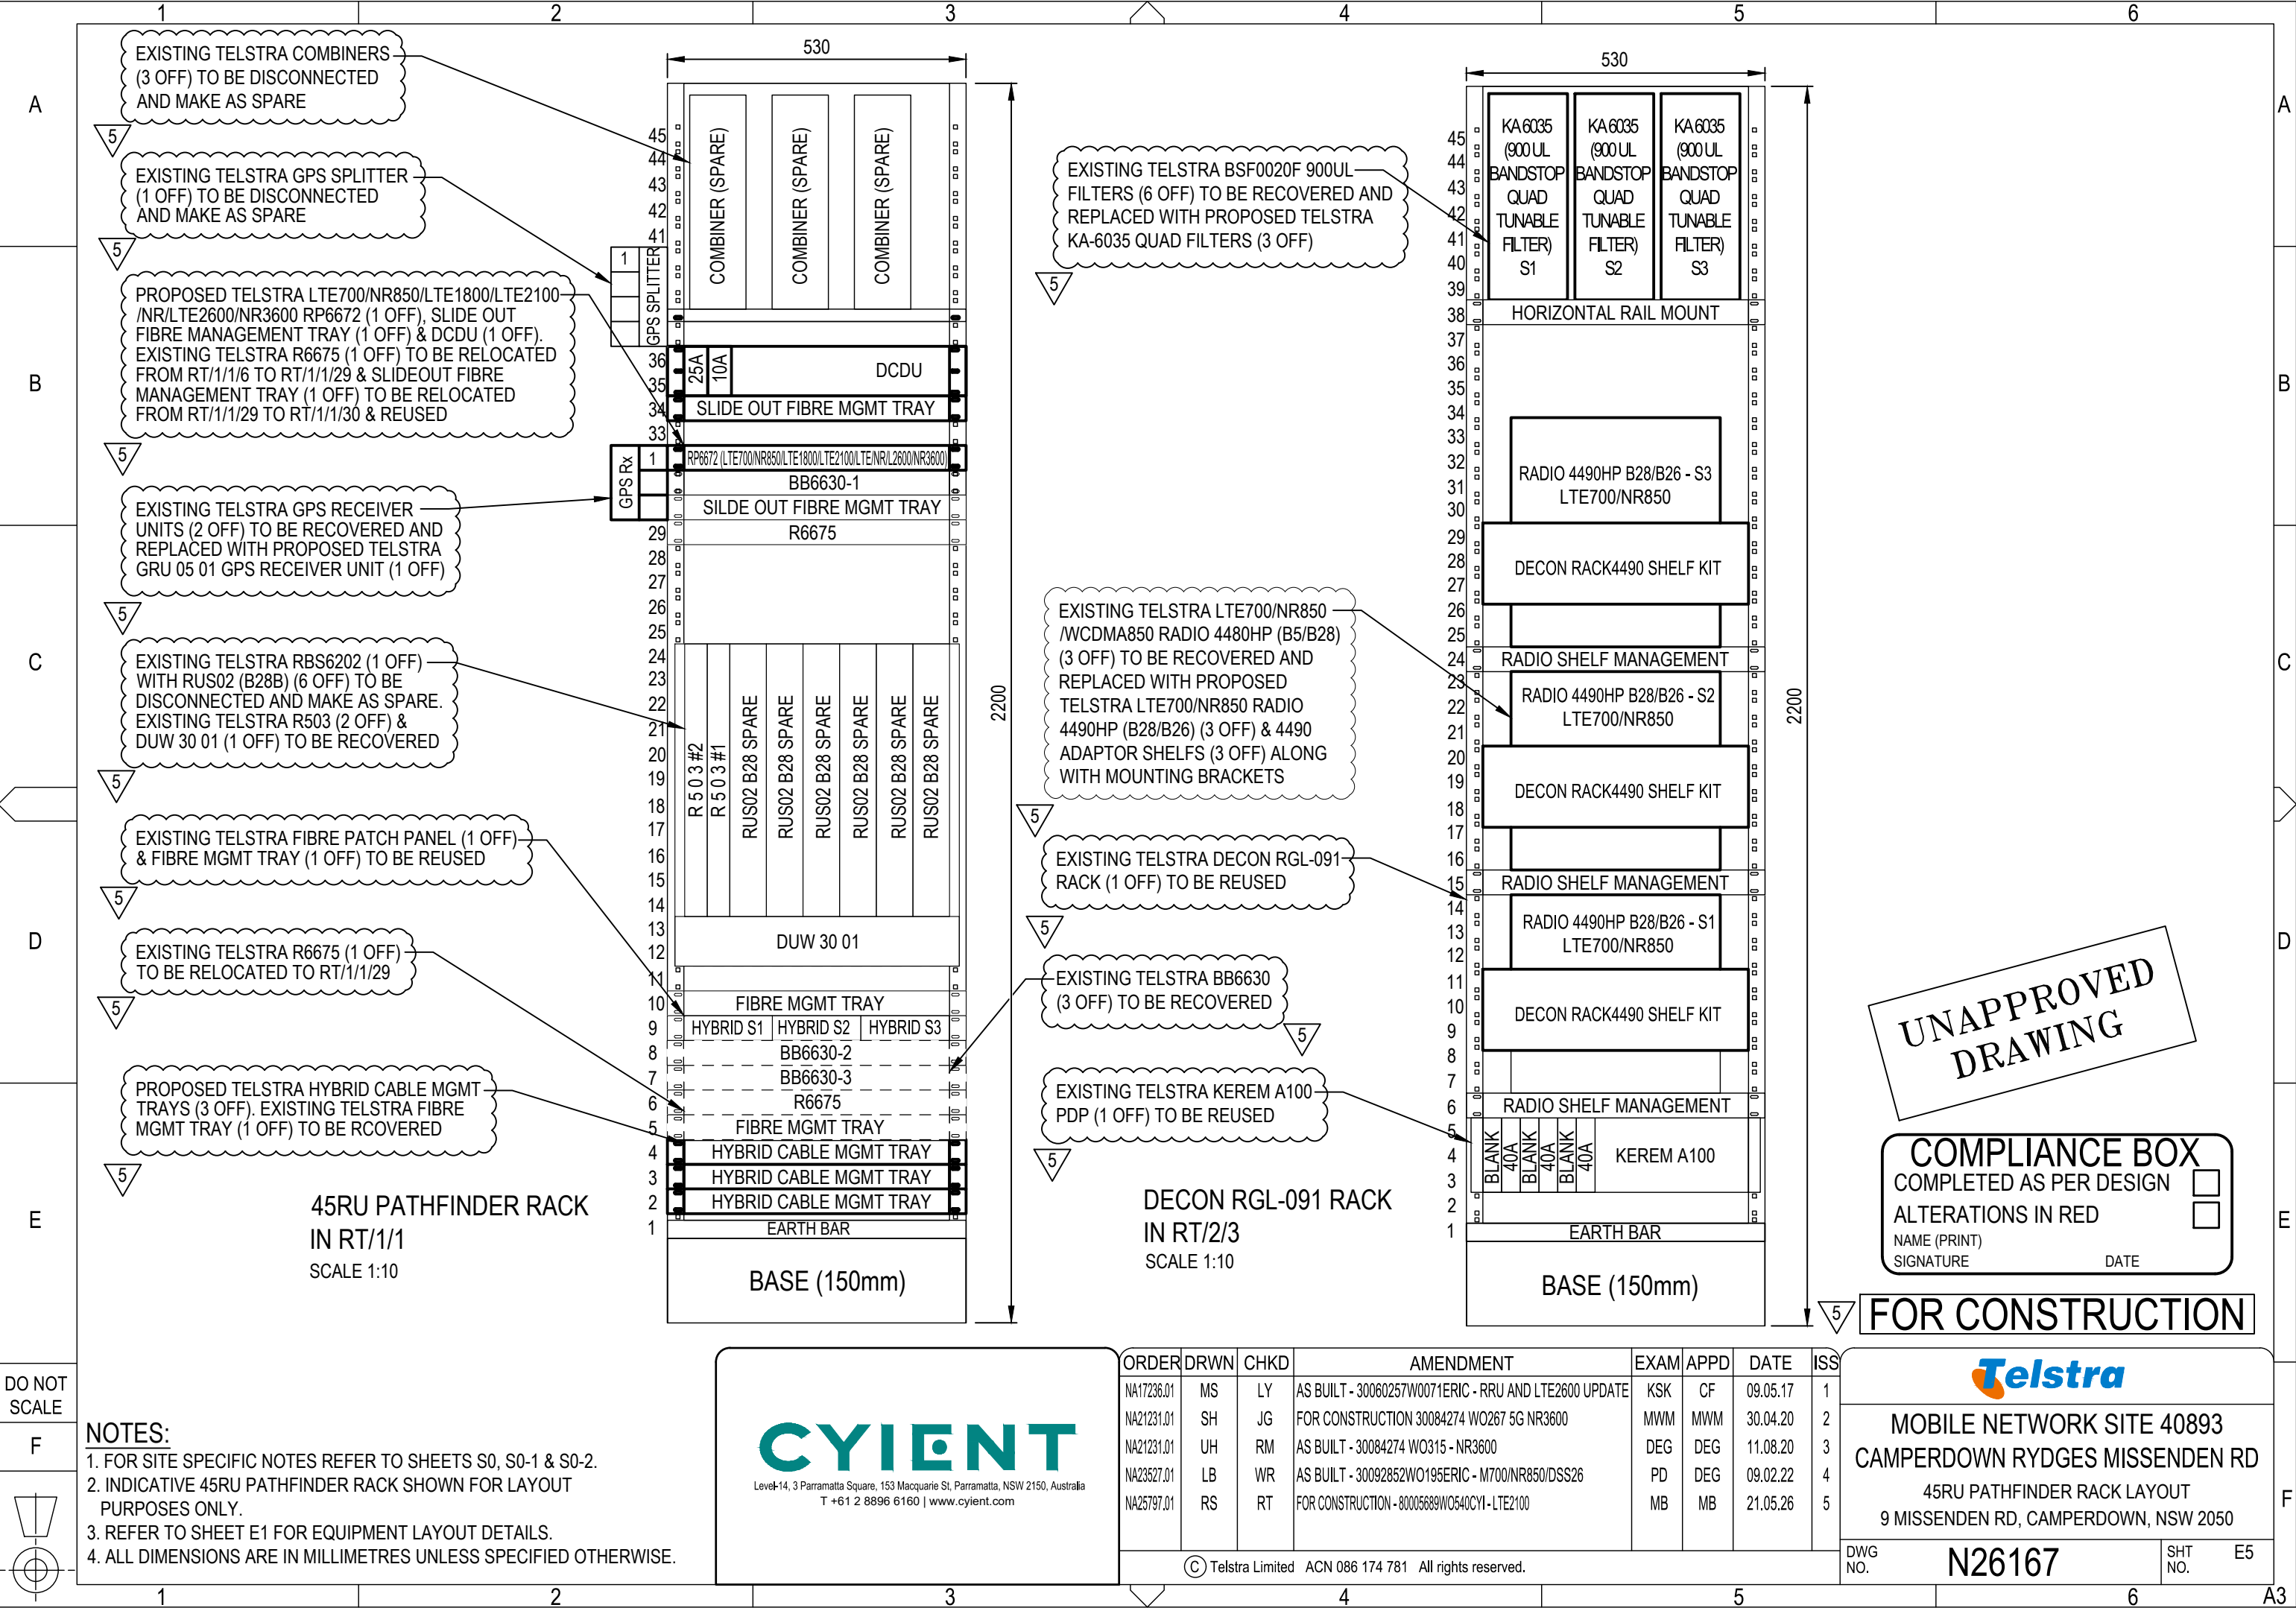

DO NOT SCALE

F

**NOTES:**

1. FOR SITE SPECIFIC NOTES REFER TO SHEETS S0, S0-1 & S0-2.

2. INDICATIVE 45RU PATHFINDER RACK SHOWN FOR LAYOUT PURPOSES ONLY.

3. REFER TO SHEET E1 FOR EQUIPMENT LAYOUT DETAILS.

4. ALL DIMENSIONS ARE IN MILLIMETRES UNLESS SPECIFIED OTHERWISE.

Level 14, 3 Parramatta Square, 153 Macquarie St, Parramatta, NSW 2150, Australia  
T +61 2 8896 6160 | www.cyient.com

| ORDER      | DRWN | CHKD | AMENDMENT                                             | EXAM | APPD | DATE     | ISS |
|------------|------|------|-------------------------------------------------------|------|------|----------|-----|
| NA17236.01 | MS   | LY   | AS BUILT - 30060257W0071ERIC - RRU AND LTE2600 UPDATE | KSK  | CF   | 09.05.17 | 1   |
| NA21231.01 | SH   | JG   | FOR CONSTRUCTION 30084274 W0267 5G NR3600             | MWM  | MWM  | 30.04.20 | 2   |
| NA21231.01 | UH   | RM   | AS BUILT - 30084274 W0315 - NR3600                    | DEG  | DEG  | 11.08.20 | 3   |
| NA23527.01 | LB   | WR   | AS BUILT - 30092852W0195ERIC - M700/NR850/DSS26       | PD   | DEG  | 09.02.22 | 4   |
| NA25797.01 | RS   | RT   | FOR CONSTRUCTION - 80005689W0540CYI - LTE2100         | MB   | MB   | 21.05.26 | 5   |



© Telstra Limited ACN 086 174 781 All rights reserved.

**MOBILE NETWORK SITE 40893**  
**CAMPERDOWN RYDGES MISSENDEN RD**  
**45RU PATHFINDER RACK LAYOUT**  
**9 MISSENDEN RD, CAMPERDOWN, NSW 2050**

DWG NO. **N26167**

SHT NO. **E5**



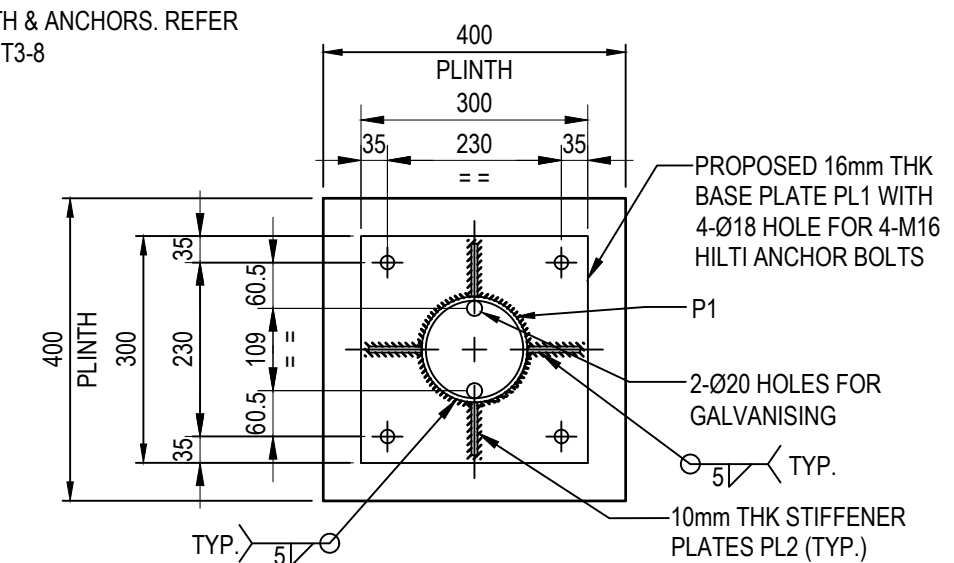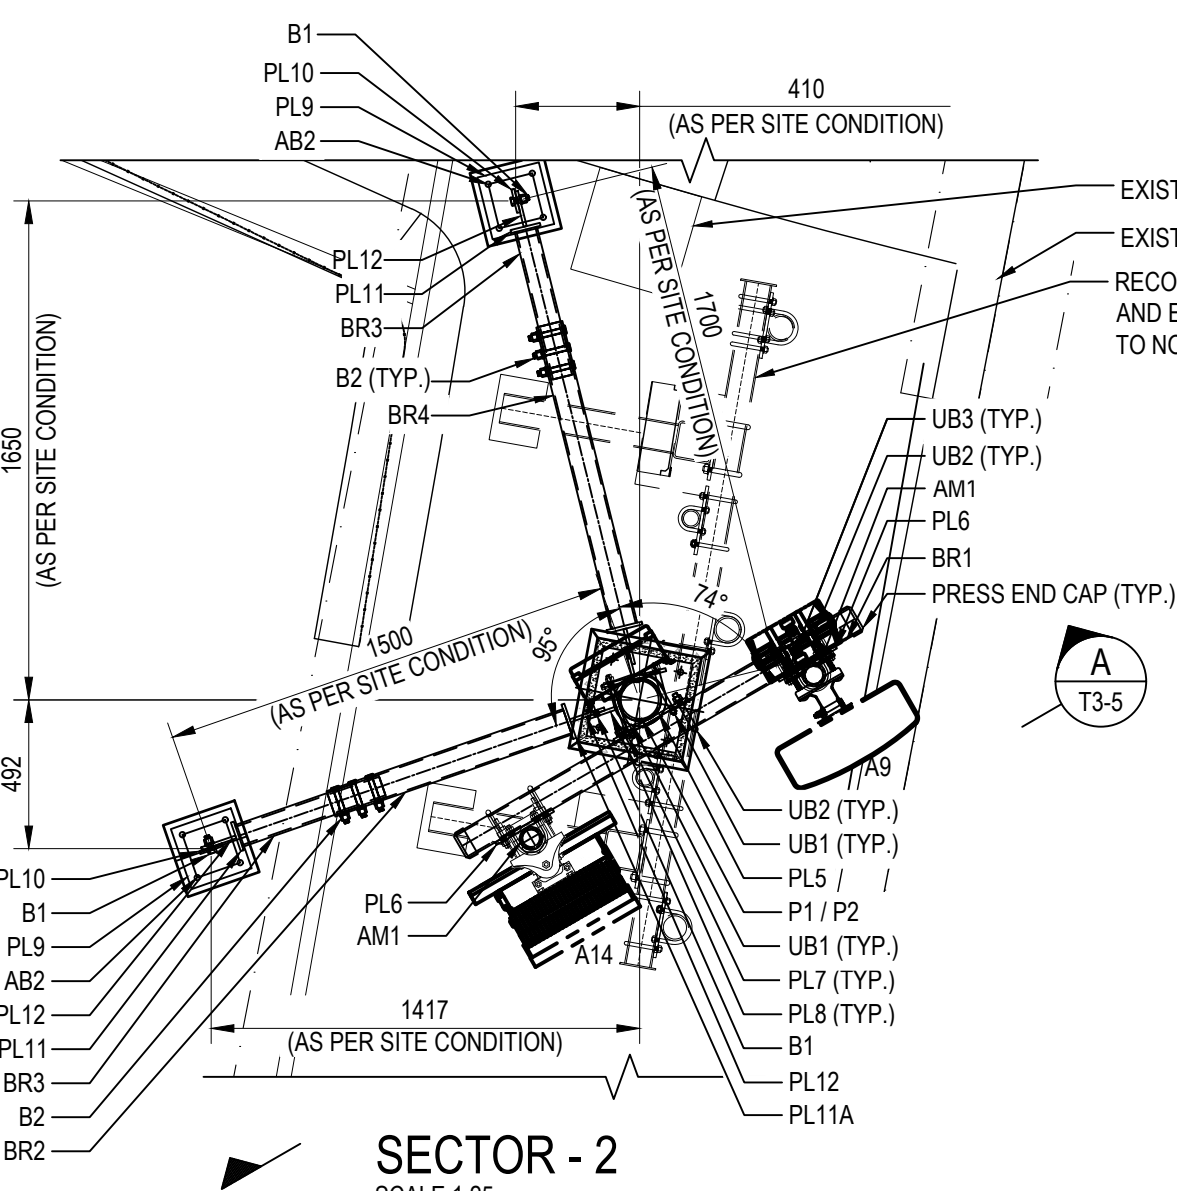

SECTOR - 2  
SCALE 1:25  
ANTENNA MOUNTING PLAN AT E.L. 25.40m & 26.30m

- NOTES:**
- 1.FOR STANDARD CONSTRUCTION NOTES REFER TO TELSTRA STANDARD DRAWING 017866P05.
  2. ALL DIMENSIONS ARE IN MILLIMETERS UNLESS SPECIFIED OTHERWISE.
  3. HIGH STRENGTH BOLTS AND ALL SPRING WASHERS TO AS 1252.1 (2016) GRADE /S U.N.O.
  4. ALL BOLTS INCLUDING U-BOLTS TO BE SUPPLIED WITH CORRESPONDING NUTS, SPRING WASHERS AND LOCKNUTS. REFER STANDARD DRAWING 017866P70 SHEET 4 ISSUE 4 FOR DETAILS.
  5. ALL HOLLOW SECTIONS TO AS 1163 (2016) GRADE C250LO U.N.O. ALL HOT ROLLED STEEL TO AS 3678 (2016) & AS 3679 (2016) GRADE 300 U.N.O.
  6. ALL STEELWORK TO BE IN ACCORDANCE WITH AS 4100 & AS 1163.
  7. ALL WELDING TO BE CATEGORY SP TO AS 1554 (2014) ALL WELDS TO BE 6mm CONTINUOUS FILLET WELDS U.N.O.
  8. ALL STEELWORK TO BE HOT DIP GALVANIZED TO AS 4680, AS 1559 & AS 1214.
  9. APPLY 2 COATS OF ZINC RICH PAINT TO ALL FRESHLY CUT, WELDED OR DRILLED STEEL ON SITE, REMOVE ALL SWARF, BURRS & SHARP EDGES.

**NOTE:**  
RECOVER EXISTING STRUCTURE AND INSTALL PROPOSED NEW POLE FOR A9 & A14 ANTENNA

**NOTE FOR MANUFACTURER & INSTALLER:**  
TRIAL ASSEMBLE PRIOR TO GALVANISING AND DELIVERY TO SITE TO ENSURE CORRECT FIT AND NUMBER OF PARTS

**CYIENT**  
Level-14, 3 Parramatta Square, 153 Macquarie St, Parramatta, NSW 2150, Australia  
T +61 2 8896 6160 | www.cyient.com

| ORDER      | DRWN | CHKD | AMENDMENT                                     | EXAM | APPD | DATE     | ISS |
|------------|------|------|-----------------------------------------------|------|------|----------|-----|
| NA25797.01 | DSS  | GNK  | FOR CONSTRUCTION - 80005689W0540CYI - LTE2100 | MB   | MB   | 21.05.26 | 1   |

© Telstra Limited ACN 086 174 781 All rights reserved.

UNAPPROVED  
DRAWING


**COMPLIANCE BOX**  
COMPLETED AS PER DESIGN ☐  
ALTERATIONS IN RED ☐  
NAME (PRINT) \_\_\_\_\_  
SIGNATURE \_\_\_\_\_ DATE \_\_\_\_\_

**FOR CONSTRUCTION**

**Telstra**

MOBILE NETWORK SITE 40893  
CAMPERDOWN RYDGES MISSENDEN RD  
ANTENNA MOUNTING DETAILS - SHEET 1 OF 9  
9 MISSENDEN RD, CAMPERDOWN, NSW 2050

DWG NO. **N26167** SHT NO. T3-4

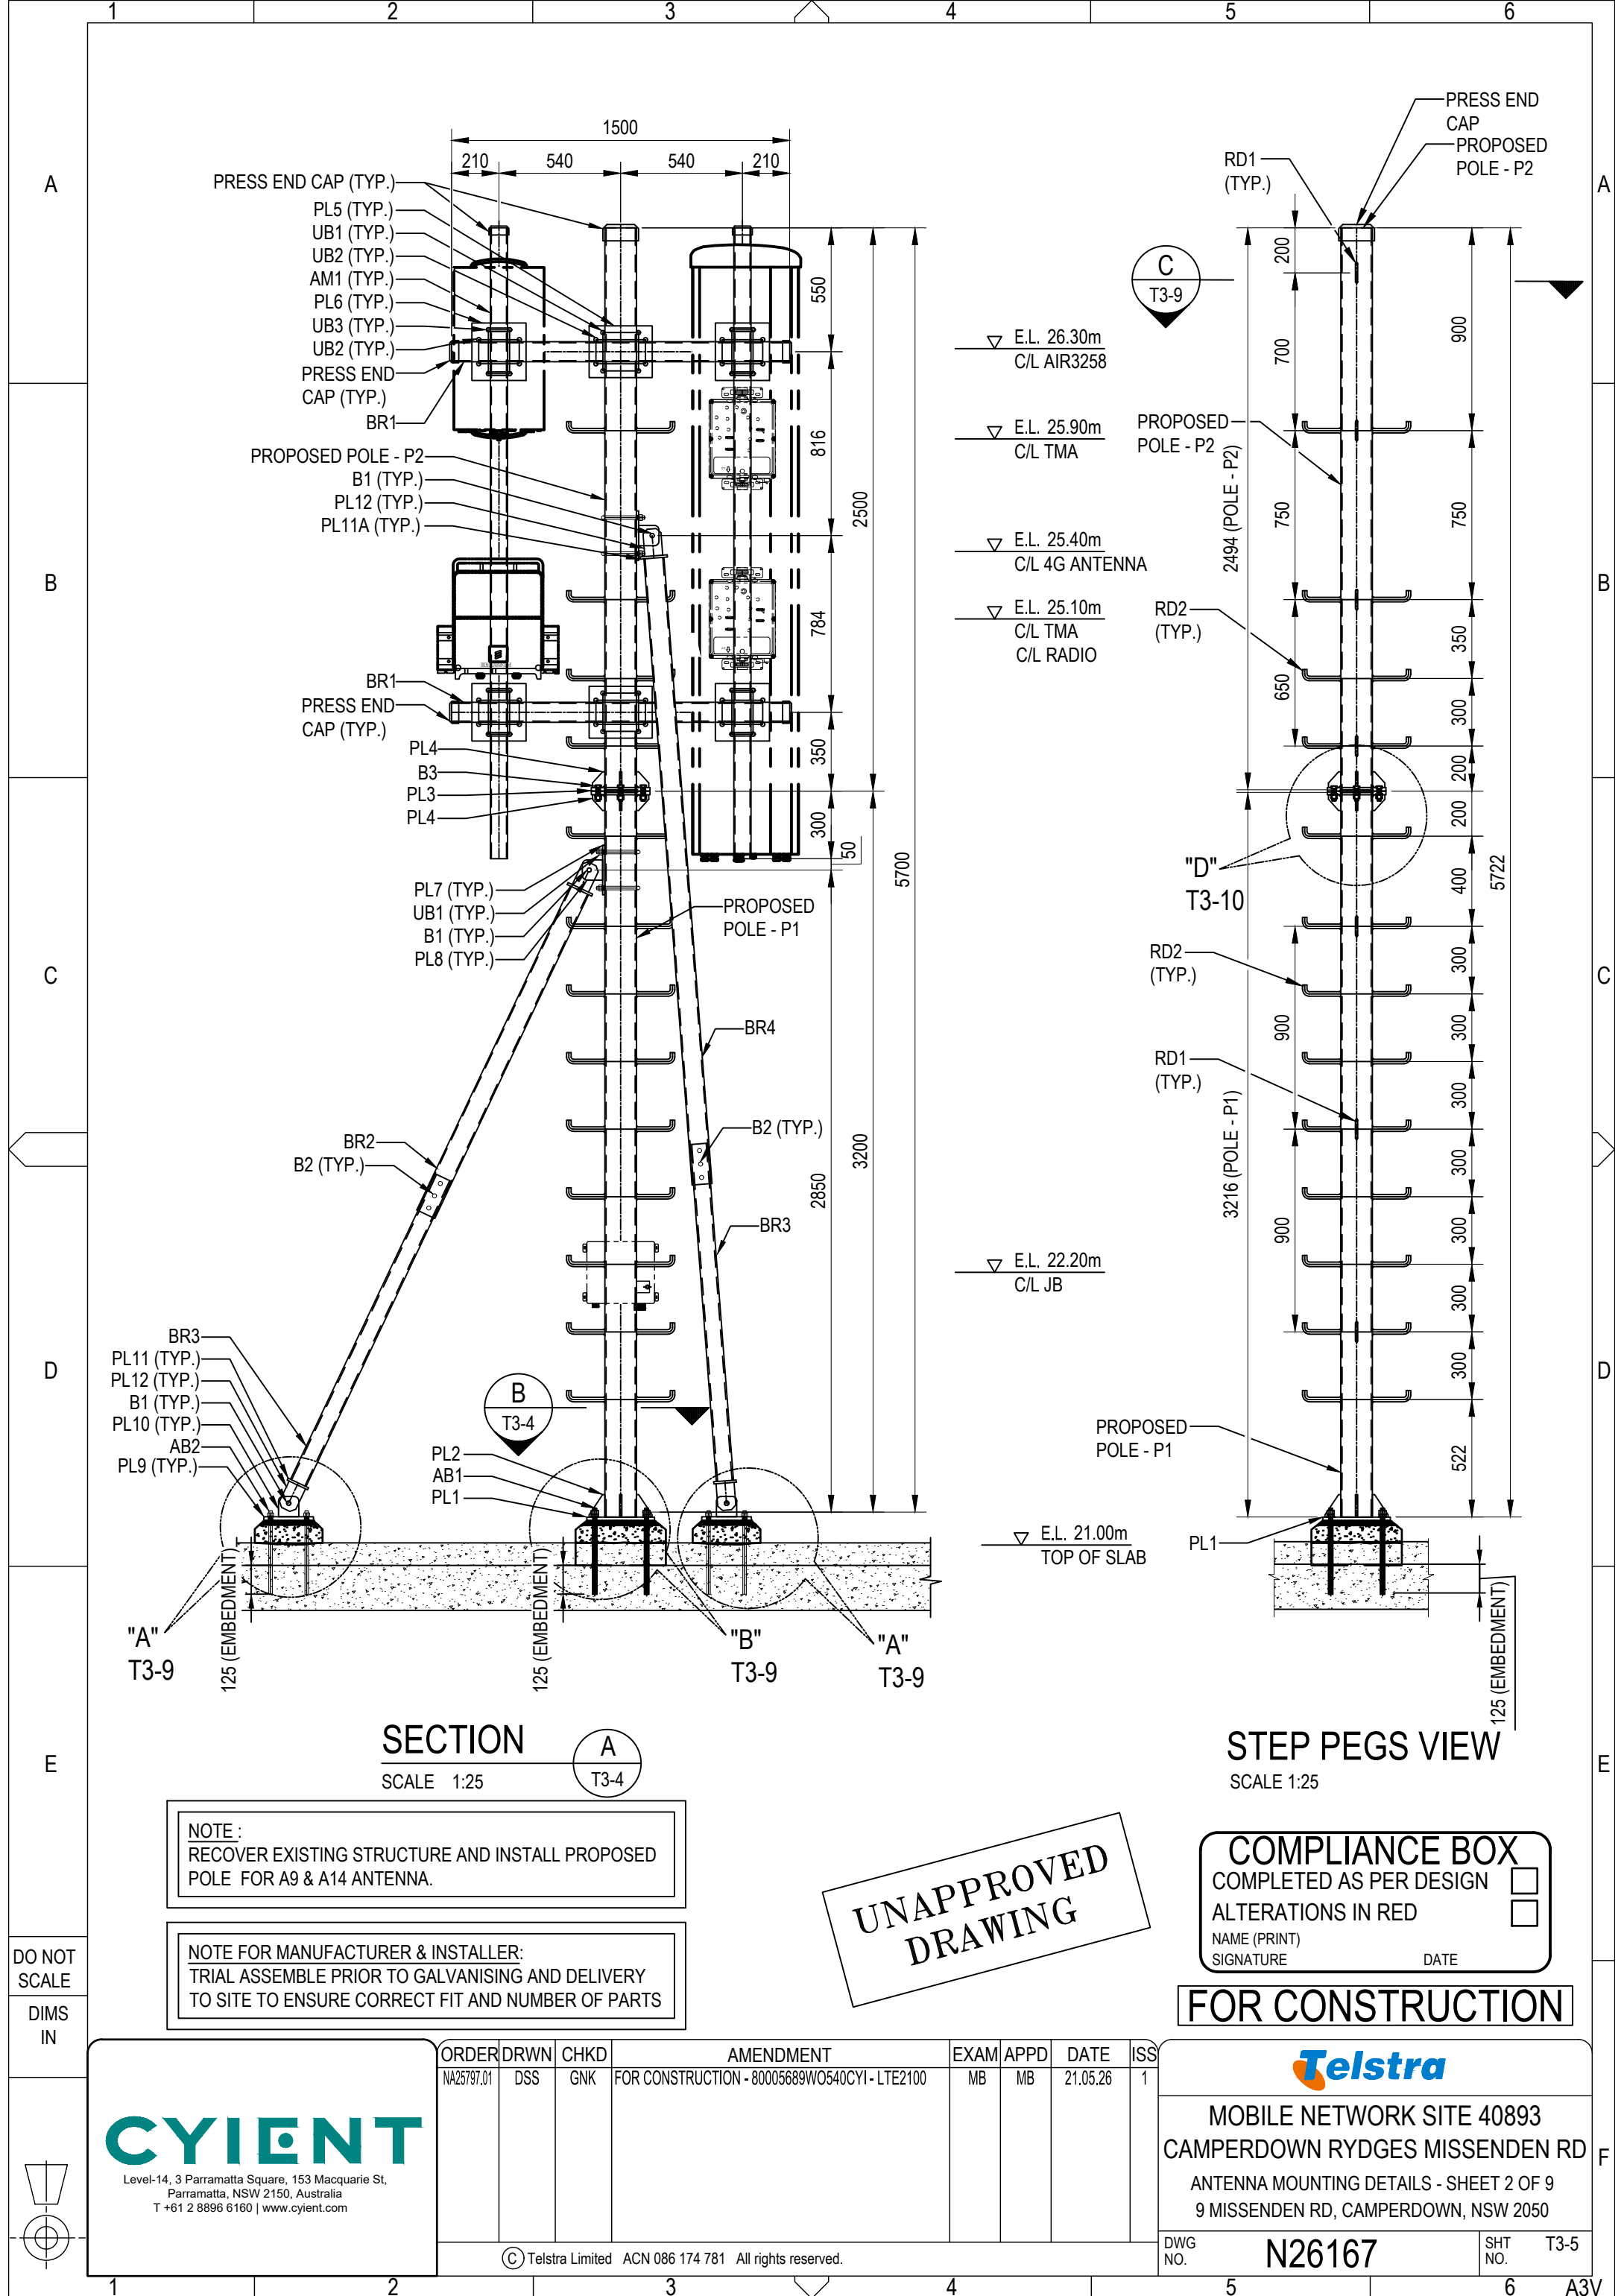

NOTE :  
RECOVER EXISTING STRUCTURE AND INSTALL PROPOSED  
POLE FOR A9 & A14 ANTENNA.

NOTE FOR MANUFACTURER & INSTALLER:  
TRIAL ASSEMBLE PRIOR TO GALVANISING AND DELIVERY  
TO SITE TO ENSURE CORRECT FIT AND NUMBER OF PARTS

**CYIENT**  
Level-14, 3 Parramatta Square, 153 Macquarie St,  
Parramatta, NSW 2150, Australia  
T +61 2 8896 6160 | www.cyient.com

| ORDER      | DRWN | CHKD | AMENDMENT                                     | EXAM | APPD | DATE     | ISS |
|------------|------|------|-----------------------------------------------|------|------|----------|-----|
| NA25797.01 | DSS  | GNK  | FOR CONSTRUCTION - 80005689WO540CYI - LTE2100 | MB   | MB   | 21.05.26 | 1   |


© Telstra Limited ACN 086 174 781 All rights reserved.

|                         |                          |
|-------------------------|--------------------------|
| <b>COMPLIANCE BOX</b>   |                          |
| COMPLETED AS PER DESIGN | <input type="checkbox"/> |
| ALTERATIONS IN RED      | <input type="checkbox"/> |
| NAME (PRINT)            |                          |
| SIGNATURE               | DATE                     |

**FOR CONSTRUCTION**

**Telstra**  
MOBILE NETWORK SITE 40893  
CAMPERDOWN RYDGES MISSENDEN RD  
ANTENNA MOUNTING DETAILS - SHEET 2 OF 9  
9 MISSENDEN RD, CAMPERDOWN, NSW 2050

|         |        |         |      |
|---------|--------|---------|------|
| DWG NO. | N26167 | SHT NO. | T3-5 |
|---------|--------|---------|------|

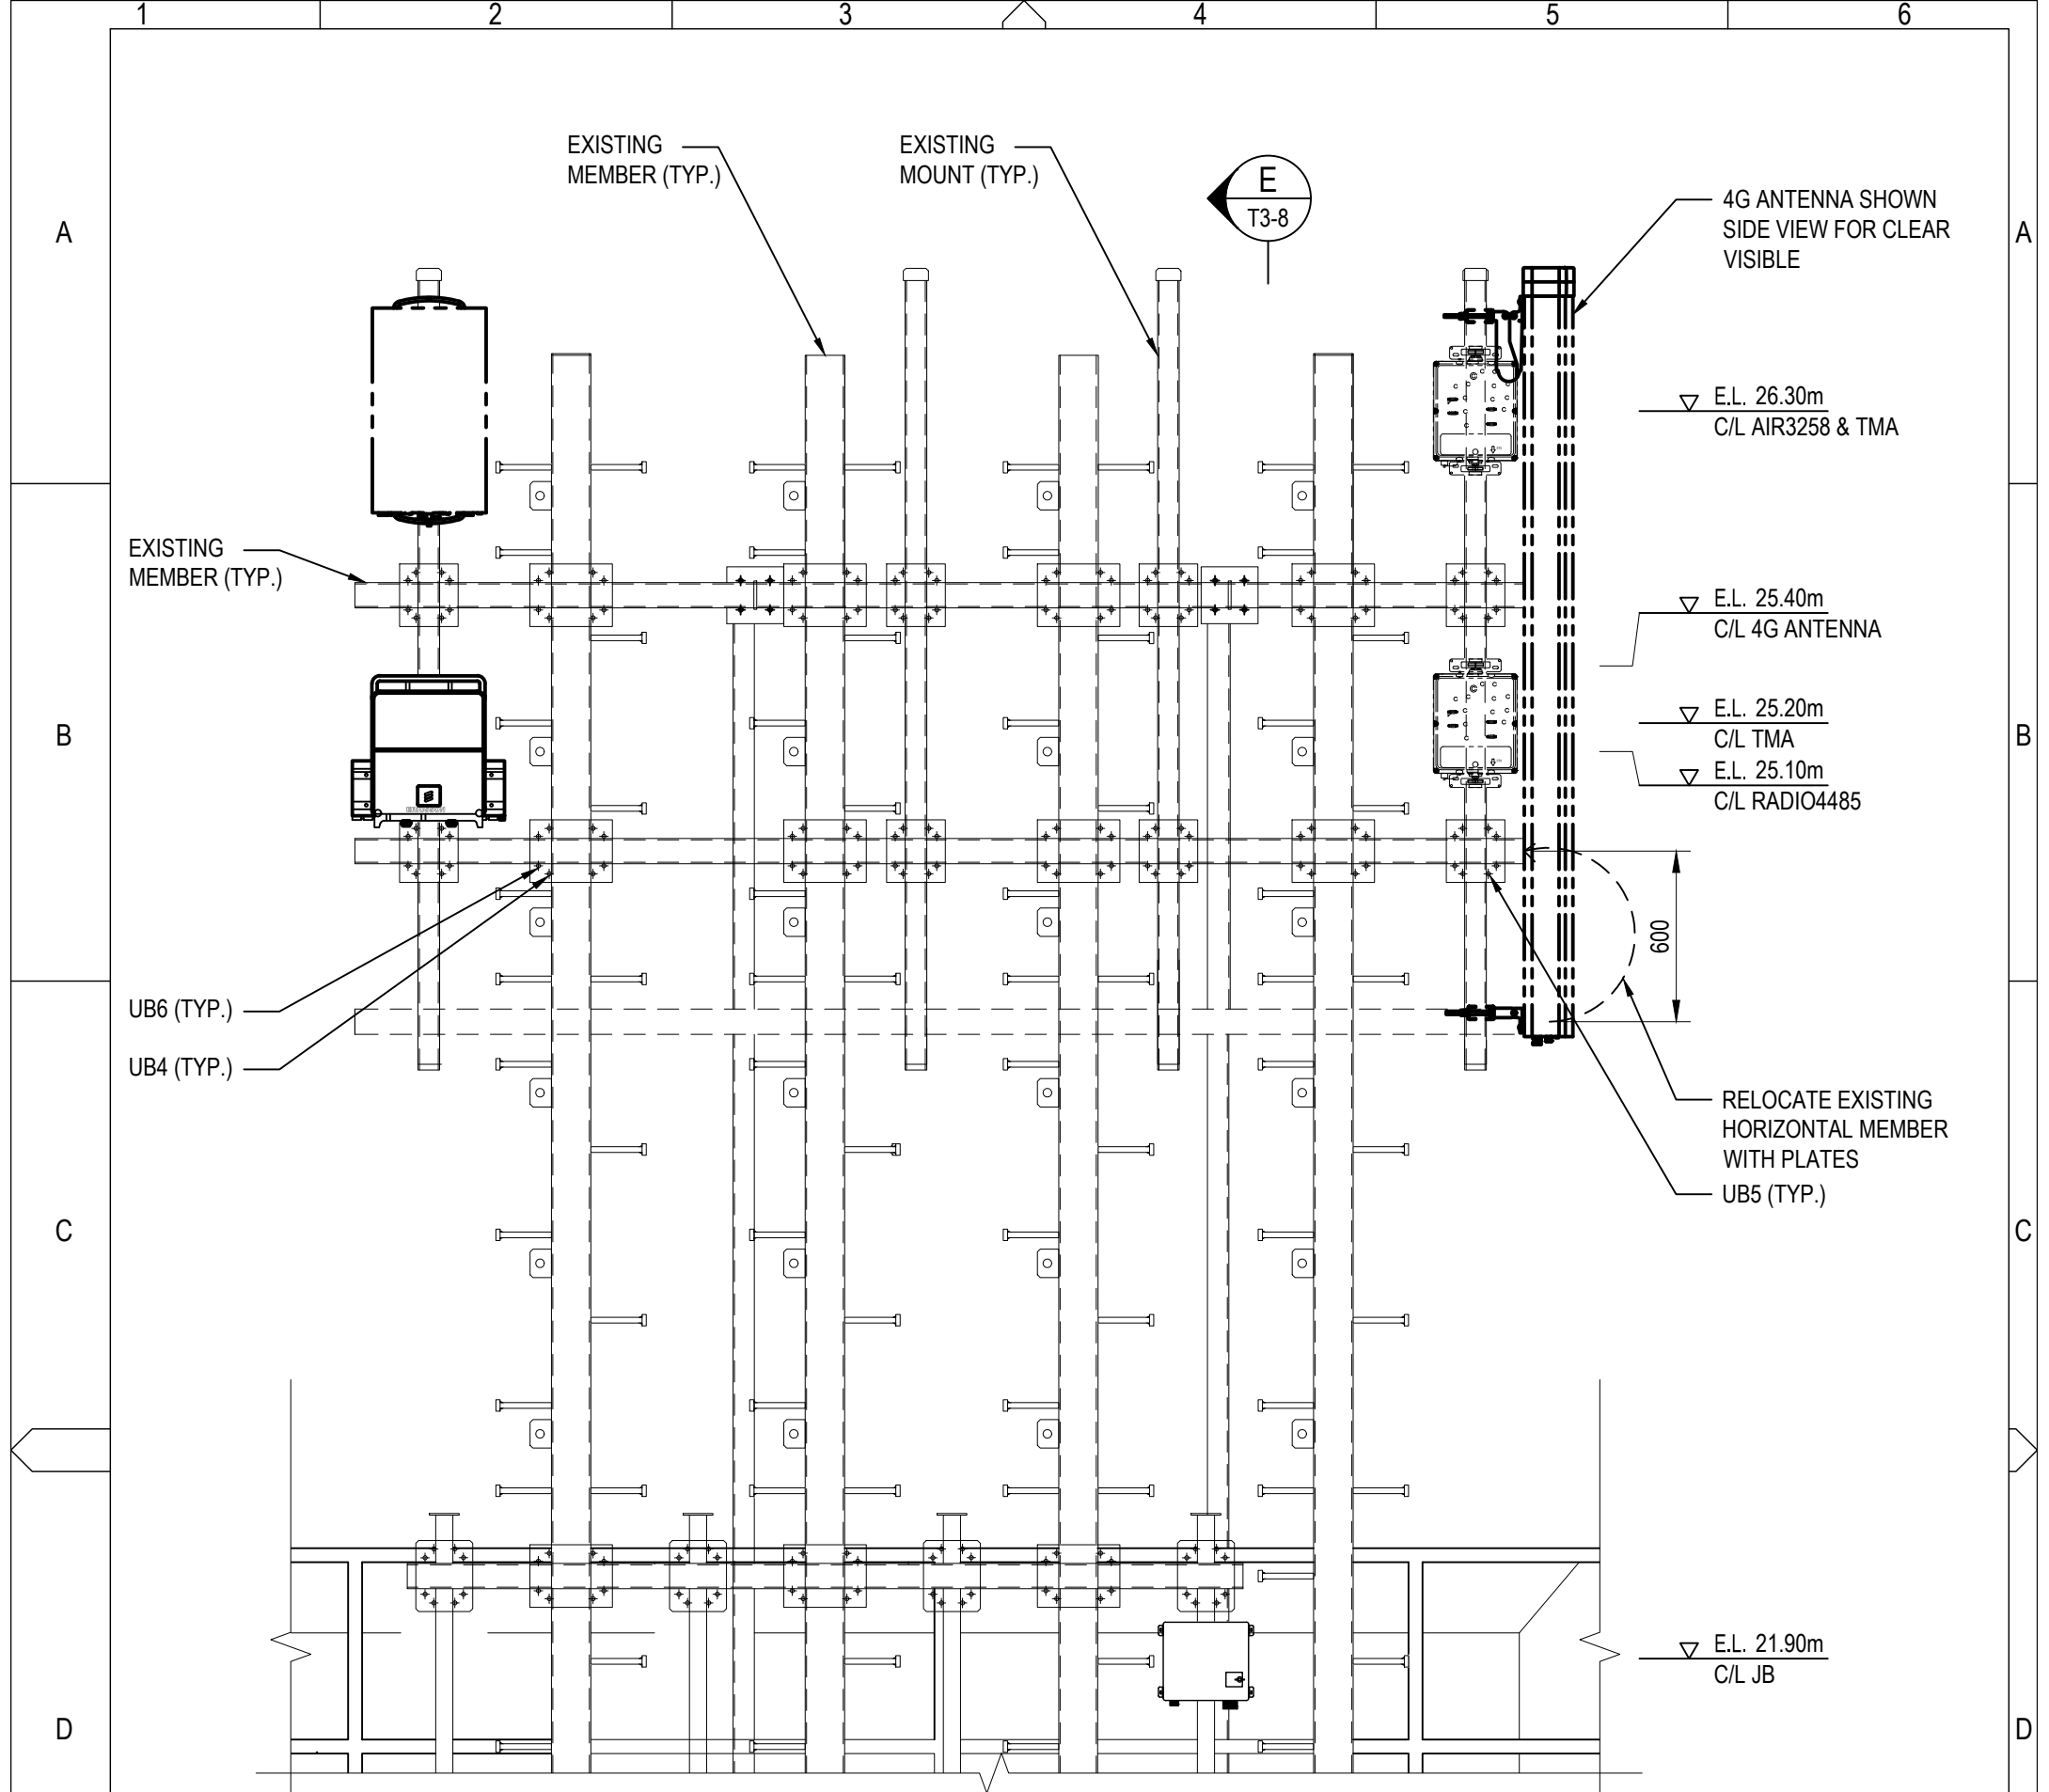

SECTOR - 1 ELEVATION  
SCALE 1:25

NOTE FOR MANUFACTURER & INSTALLER:  
TRIAL ASSEMBLE PRIOR TO GALVANISING AND DELIVERY  
TO SITE TO ENSURE CORRECT FIT AND NUMBER OF PARTS

UNAPPROVED  
DRAWING

COMPLIANCE BOX

COMPLETED AS PER DESIGN

ALTERATIONS IN RED

NAME (PRINT)

SIGNATURE

DATE

FOR CONSTRUCTION

DO NOT  
SCALE  
DIMS  
IN

CYIENT

Level-14, 3 Parramatta Square, 153 Macquarie St,  
Parramatta, NSW 2150, Australia  
T +61 2 8896 6160 | www.cyient.com

| ORDER      | DRWN | CHKD | AMENDMENT                                     | EXAM | APPD | DATE     | ISS |
|------------|------|------|-----------------------------------------------|------|------|----------|-----|
| NA25797.01 | DSS  | GNK  | FOR CONSTRUCTION - 80005689WO540CYI - LTE2100 | MB   | MB   | 21.05.26 | 1   |

© Telstra Limited ACN 086 174 781 All rights reserved.




MOBILE NETWORK SITE 40893  
CAMPERDOWN RYDGES MISSENDEN RD  
ANTENNA MOUNTING DETAILS - SHEET 3 OF 9  
9 MISSENDEN RD, CAMPERDOWN, NSW 2050

DWG NO. N26167

SHT NO. T3-6



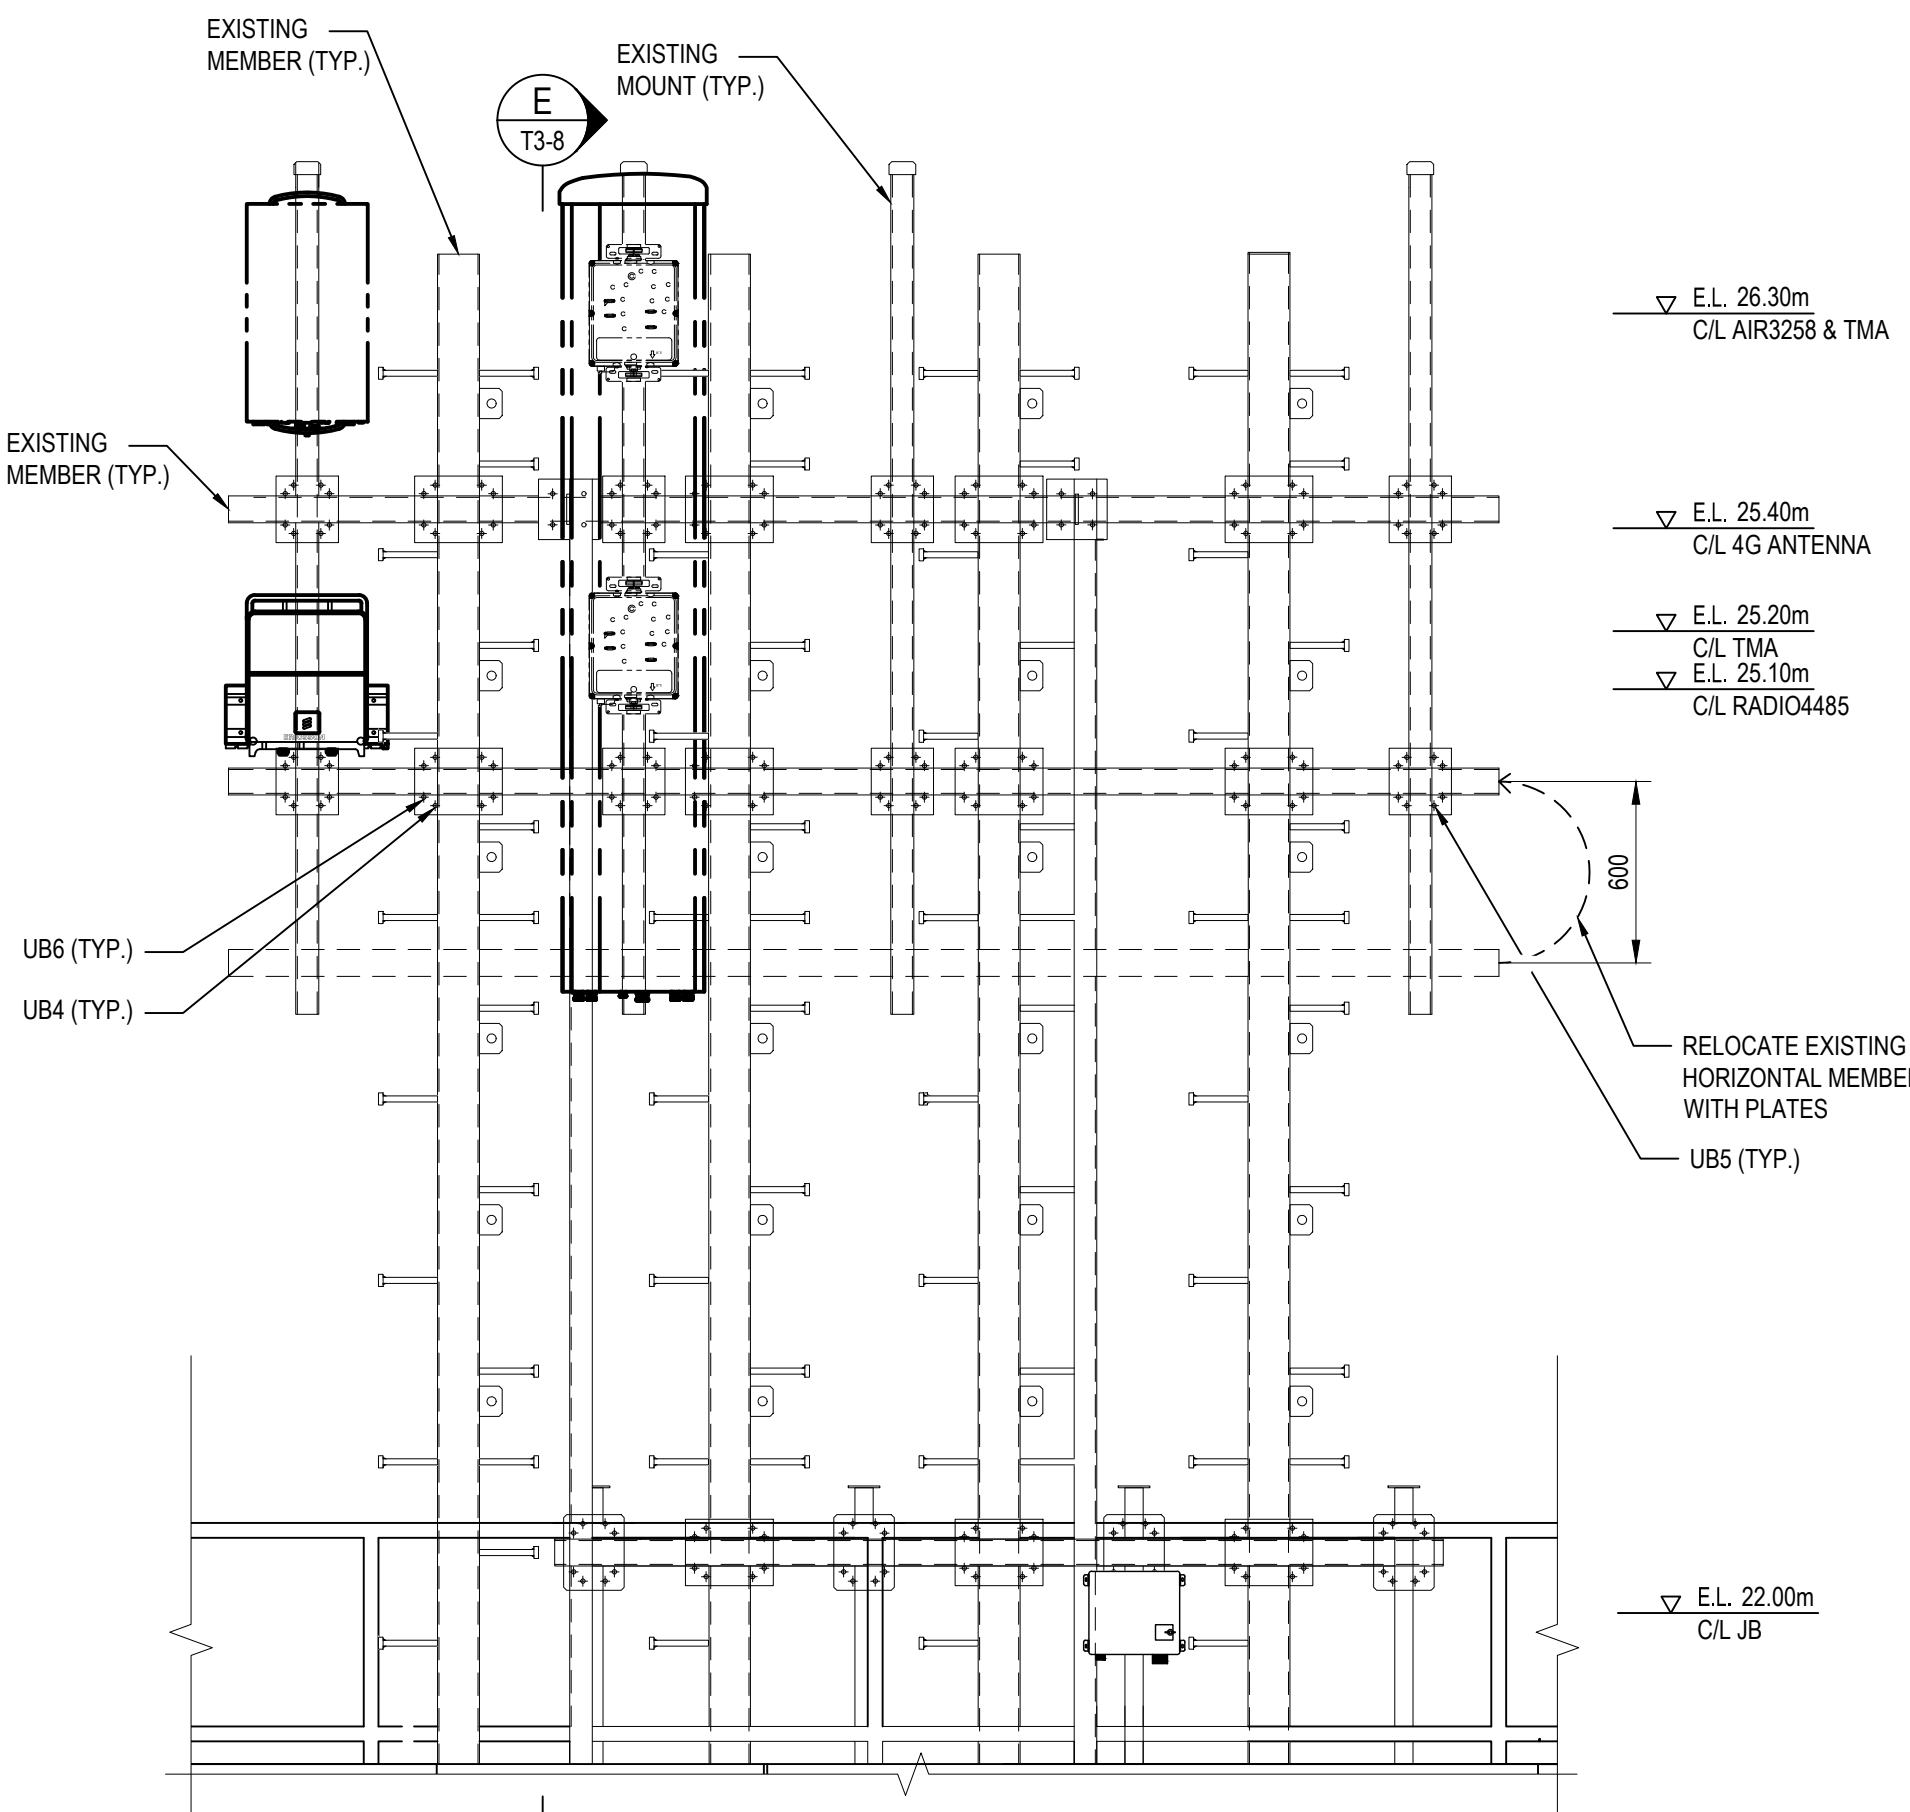

SECTOR - 3 ELEVATION  
SCALE 1:25

NOTE FOR MANUFACTURER & INSTALLER:  
TRIAL ASSEMBLE PRIOR TO GALVANISING AND DELIVERY  
TO SITE TO ENSURE CORRECT FIT AND NUMBER OF PARTS

UNAPPROVED  
DRAWING

|                         |                          |
|-------------------------|--------------------------|
| <b>COMPLIANCE BOX</b>   |                          |
| COMPLETED AS PER DESIGN | <input type="checkbox"/> |
| ALTERATIONS IN RED      | <input type="checkbox"/> |
| NAME (PRINT)            |                          |
| SIGNATURE               | DATE                     |

FOR CONSTRUCTION

**CYIENT**  
Level-14, 3 Parramatta Square, 153 Macquarie St,  
Parramatta, NSW 2150, Australia  
T +61 2 8896 6160 | www.cyient.com


| ORDER      | DRWN | CHKD | AMENDMENT                                     | EXAM | APPD | DATE     | ISS |
|------------|------|------|-----------------------------------------------|------|------|----------|-----|
| NA25797.01 | DSS  | GNK  | FOR CONSTRUCTION - 80005689WO540CYI - LTE2100 | MB   | MB   | 21.05.26 | 1   |

© Telstra Limited ACN 086 174 781 All rights reserved.



MOBILE NETWORK SITE 40893  
CAMPERDOWN RYDGES MISSENDEN RD  
ANTENNA MOUNTING DETAILS - SHEET 4 OF 9  
9 MISSENDEN RD, CAMPERDOWN, NSW 2050

|         |        |         |      |
|---------|--------|---------|------|
| DWG NO. | N26167 | SHT NO. | T3-7 |
|---------|--------|---------|------|

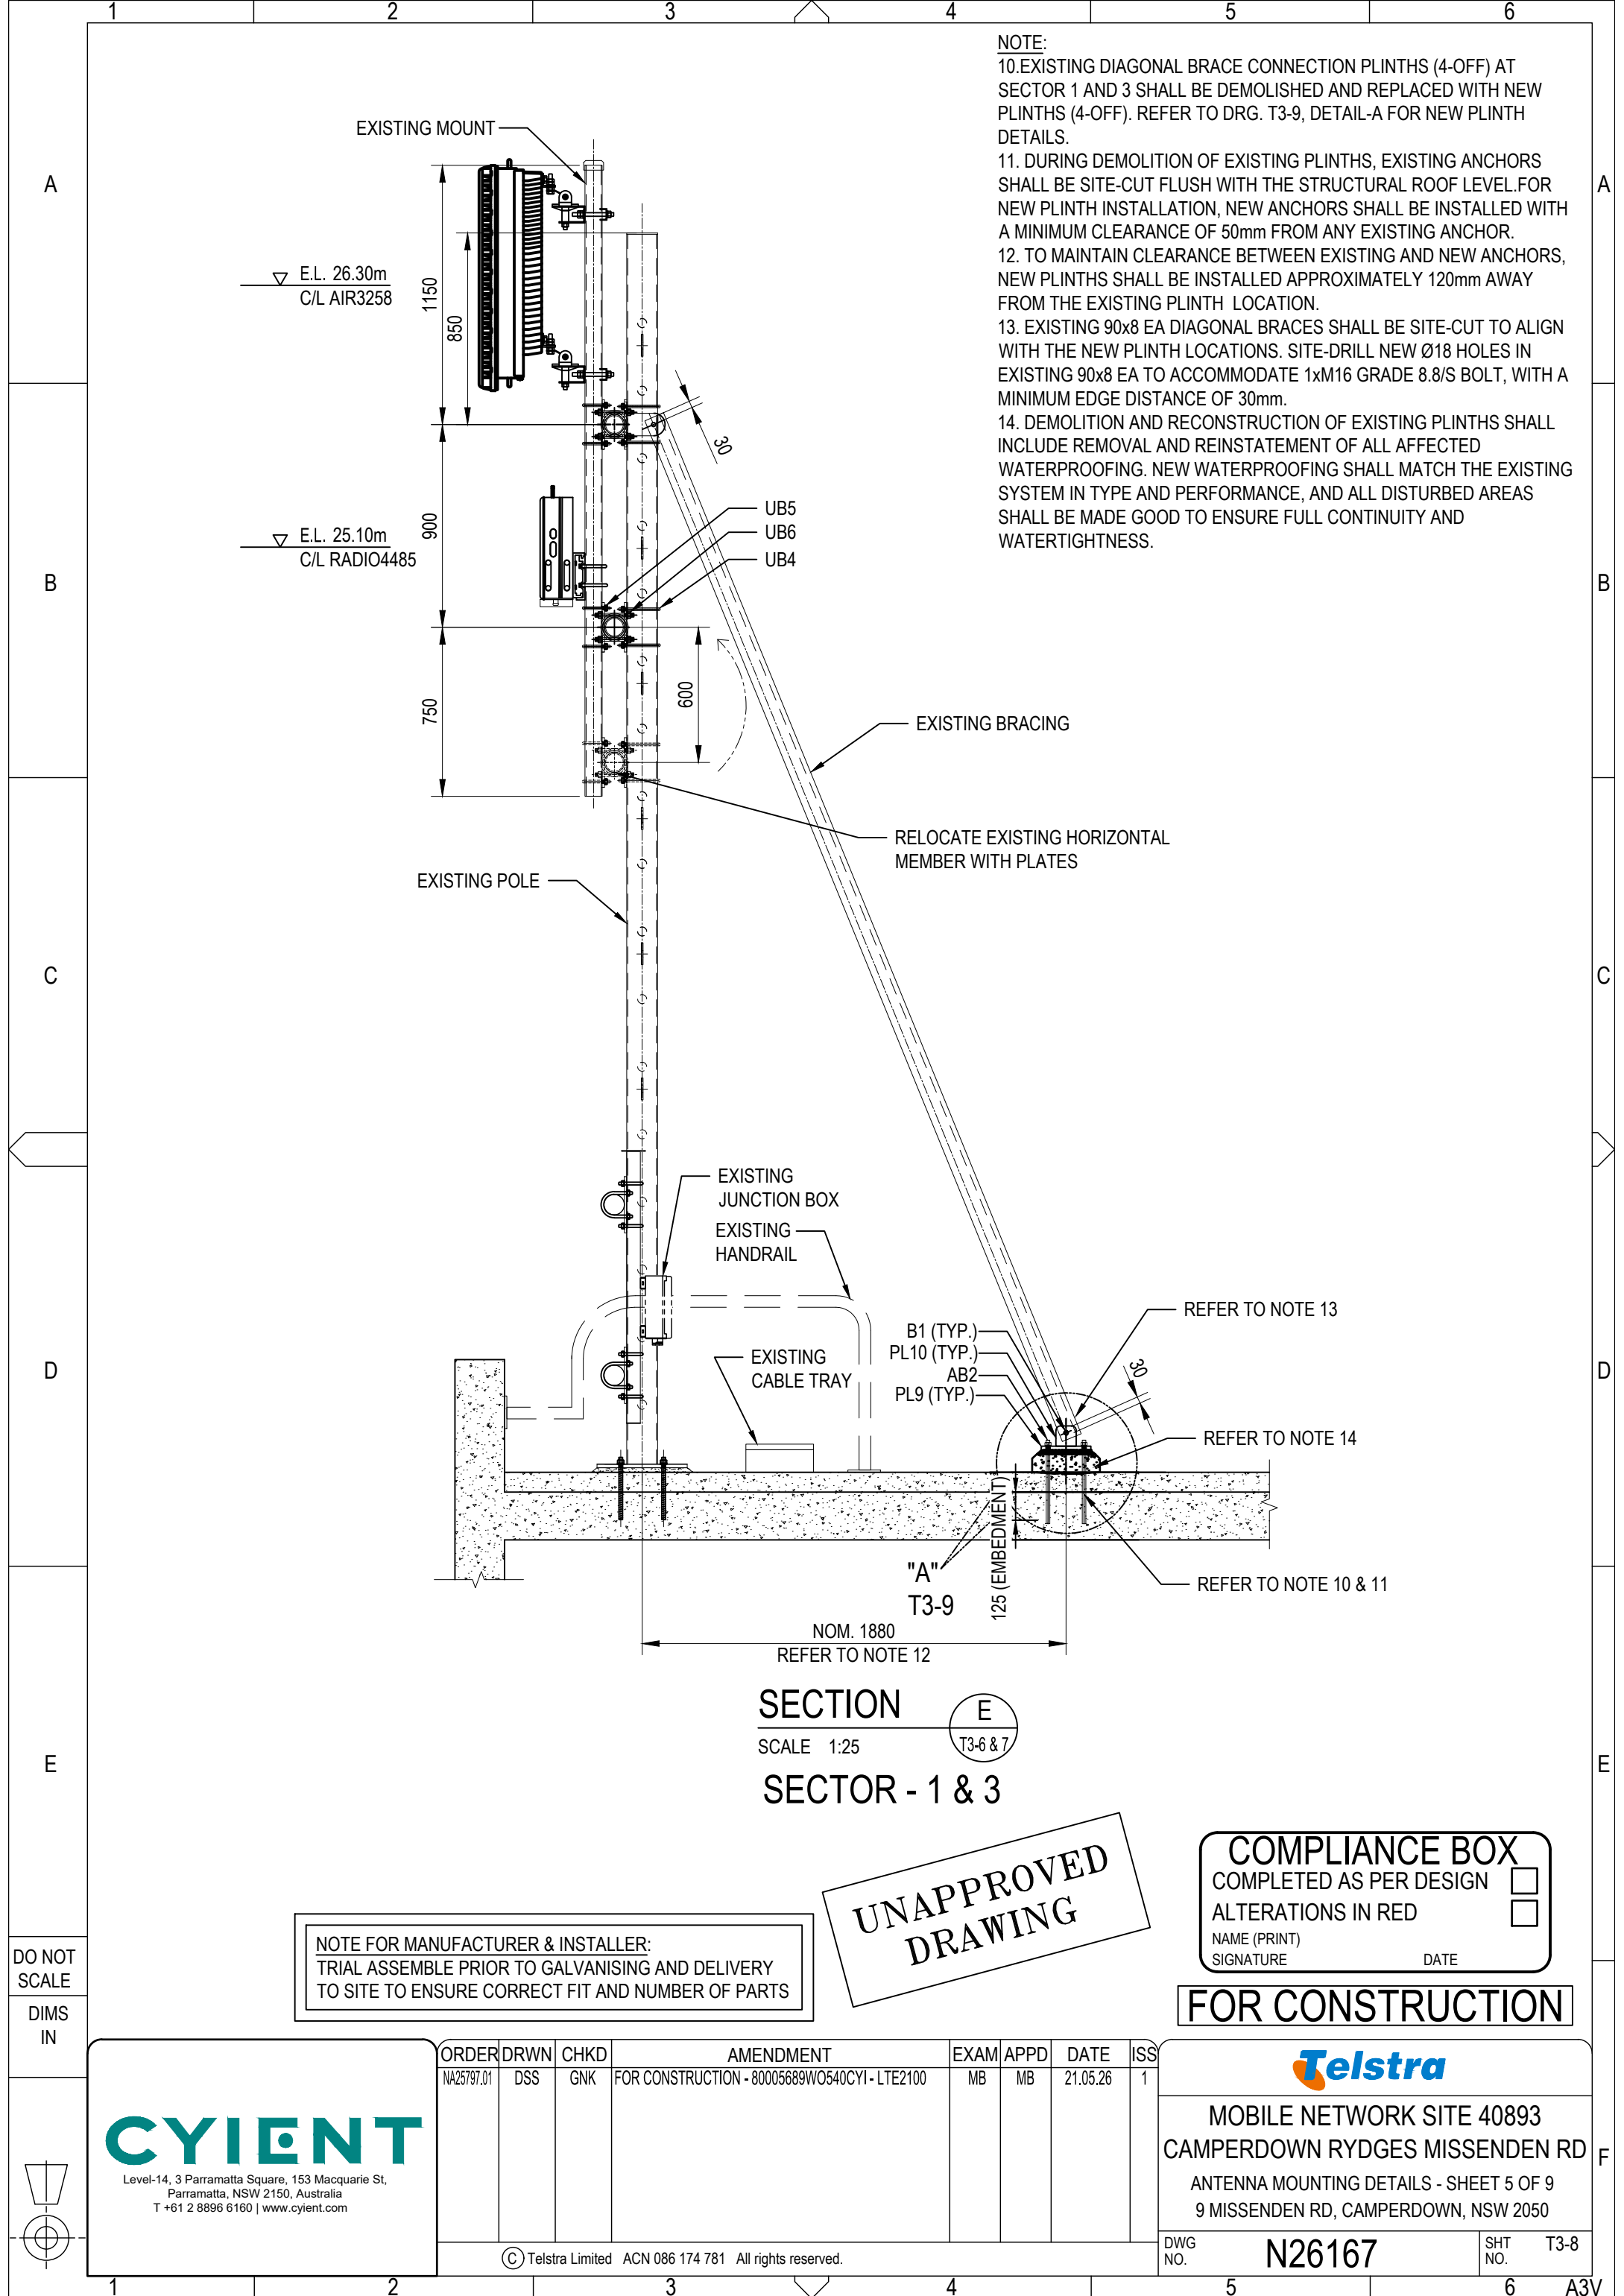

NOTE:  
10. EXISTING DIAGONAL BRACE CONNECTION PLINTHS (4-OFF) AT SECTOR 1 AND 3 SHALL BE DEMOLISHED AND REPLACED WITH NEW PLINTHS (4-OFF). REFER TO DRG. T3-9, DETAIL-A FOR NEW PLINTH DETAILS.  
11. DURING DEMOLITION OF EXISTING PLINTHS, EXISTING ANCHORS SHALL BE SITE-CUT FLUSH WITH THE STRUCTURAL ROOF LEVEL. FOR NEW PLINTH INSTALLATION, NEW ANCHORS SHALL BE INSTALLED WITH A MINIMUM CLEARANCE OF 50mm FROM ANY EXISTING ANCHOR.  
12. TO MAINTAIN CLEARANCE BETWEEN EXISTING AND NEW ANCHORS, NEW PLINTHS SHALL BE INSTALLED APPROXIMATELY 120mm AWAY FROM THE EXISTING PLINTH LOCATION.  
13. EXISTING 90x8 EA DIAGONAL BRACES SHALL BE SITE-CUT TO ALIGN WITH THE NEW PLINTH LOCATIONS. SITE-DRILL NEW Ø18 HOLES IN EXISTING 90x8 EA TO ACCOMMODATE 1xM16 GRADE 8.8/S BOLT, WITH A MINIMUM EDGE DISTANCE OF 30mm.  
14. DEMOLITION AND RECONSTRUCTION OF EXISTING PLINTHS SHALL INCLUDE REMOVAL AND REINSTATEMENT OF ALL AFFECTED WATERPROOFING. NEW WATERPROOFING SHALL MATCH THE EXISTING SYSTEM IN TYPE AND PERFORMANCE, AND ALL DISTURBED AREAS SHALL BE MADE GOOD TO ENSURE FULL CONTINUITY AND WATERTIGHTNESS.

SECTION E  
SCALE 1:25  
T3-6 & 7  
SECTOR - 1 & 3

UNAPPROVED  
DRAWING

COMPLIANCE BOX  
COMPLETED AS PER DESIGN ☐  
ALTERATIONS IN RED ☐  
NAME (PRINT) \_\_\_\_\_  
SIGNATURE \_\_\_\_\_ DATE \_\_\_\_\_

FOR CONSTRUCTION

NOTE FOR MANUFACTURER & INSTALLER:  
TRIAL ASSEMBLE PRIOR TO GALVANISING AND DELIVERY  
TO SITE TO ENSURE CORRECT FIT AND NUMBER OF PARTS

**CYIENT**  
Level-14, 3 Parramatta Square, 153 Macquarie St,  
Parramatta, NSW 2150, Australia  
T +61 2 8896 6160 | www.cyient.com

| ORDER      | DRWN | CHKD | AMENDMENT                                     | EXAM | APPD | DATE     | ISS |
|------------|------|------|-----------------------------------------------|------|------|----------|-----|
| NA25797.01 | DSS  | GNK  | FOR CONSTRUCTION - 80005689W0540CYI - LTE2100 | MB   | MB   | 21.05.26 | 1   |

© Telstra Limited ACN 086 174 781 All rights reserved.








MOBILE NETWORK SITE 40893  
CAMPERDOWN RYDGES MISSENDEN RD  
ANTENNA MOUNTING DETAILS - SHEET 5 OF 9  
9 MISSENDEN RD, CAMPERDOWN, NSW 2050

DWG NO. N26167 SHT NO. T3-8





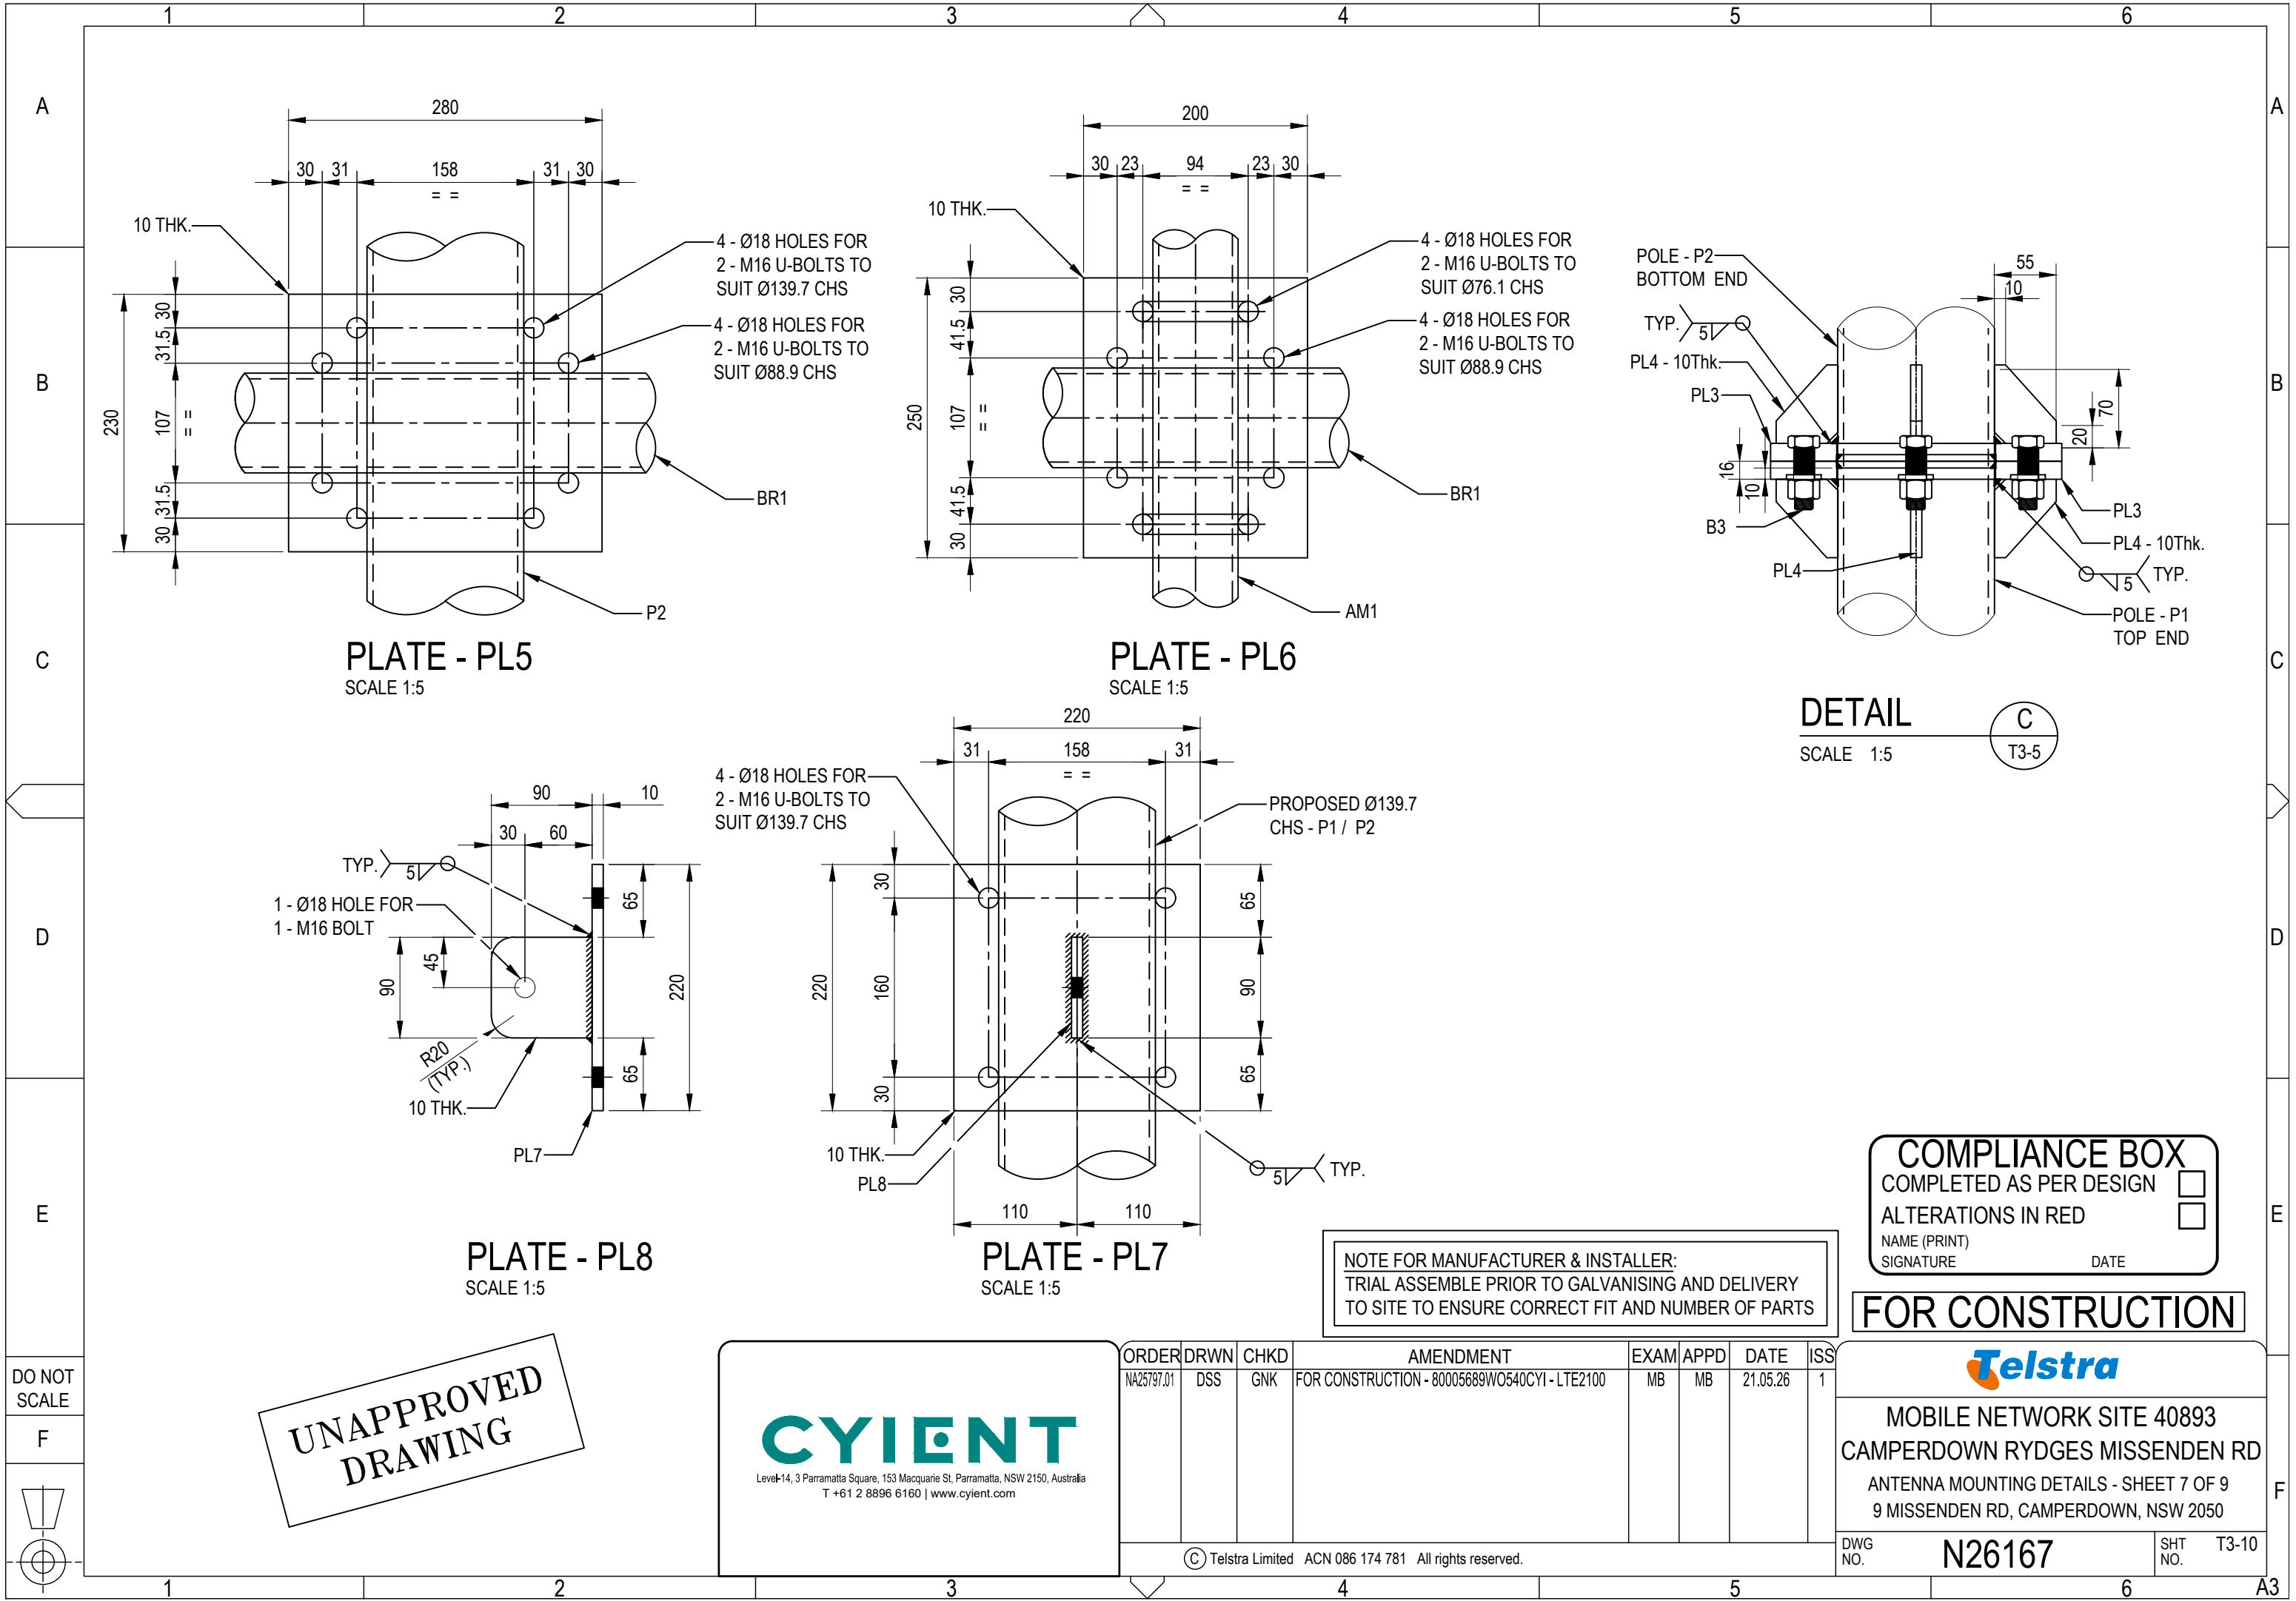

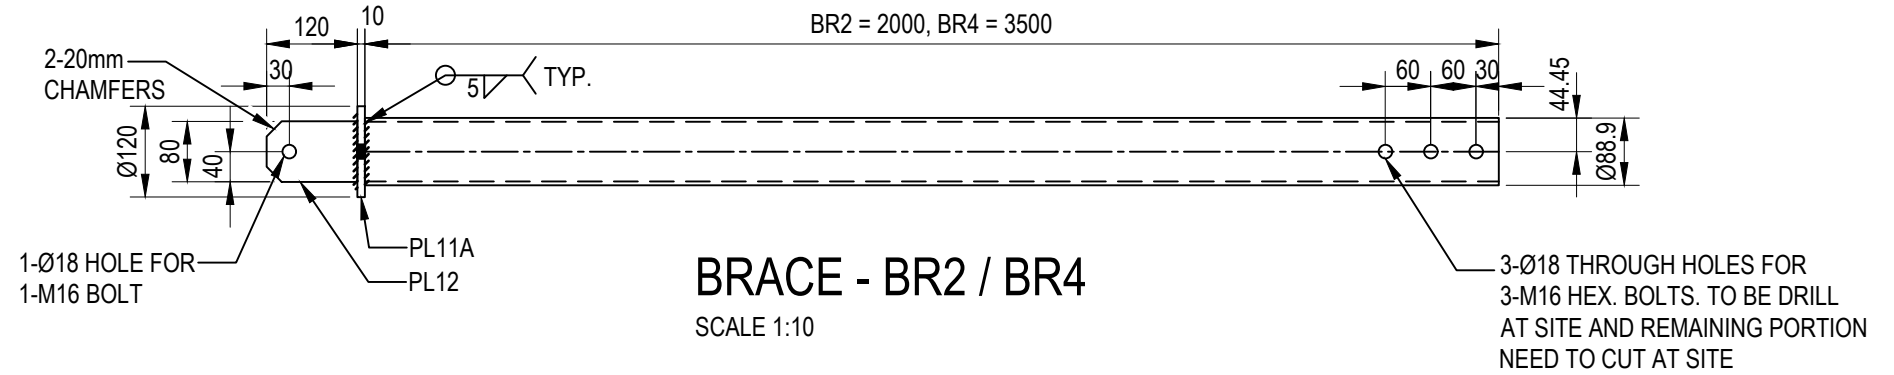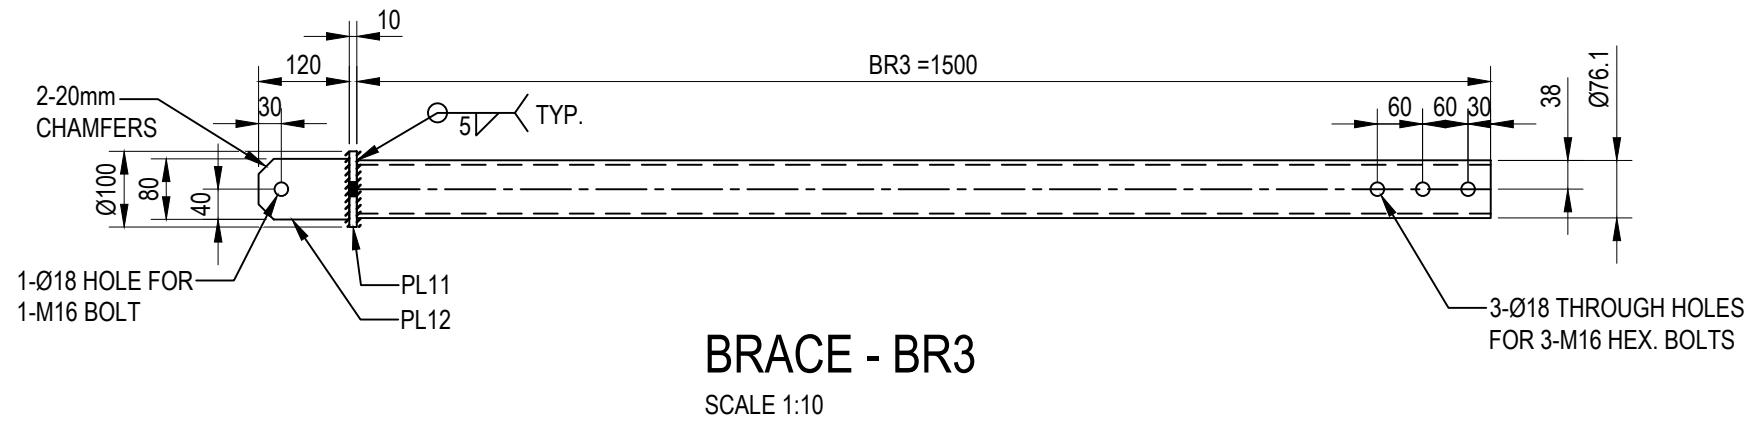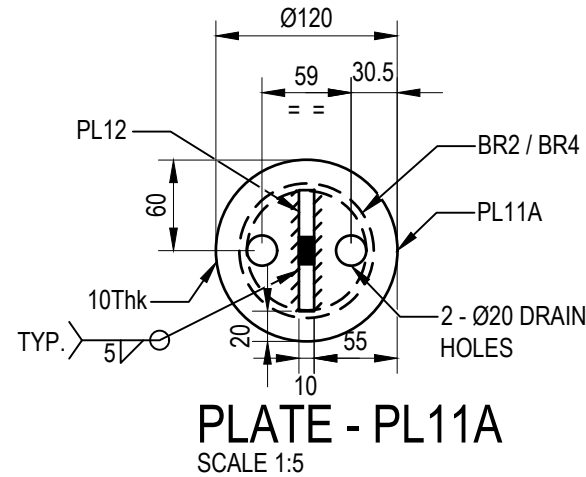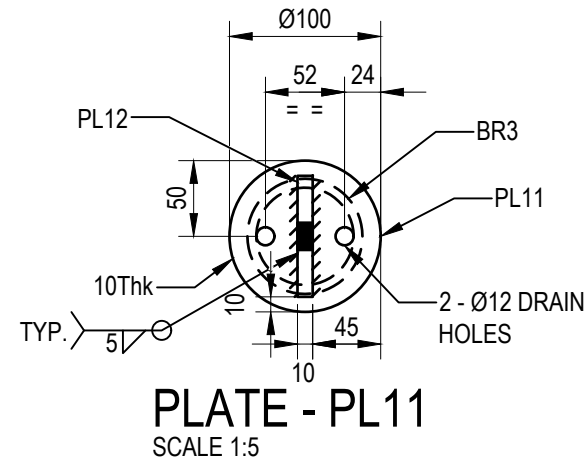

NOTE: THROUGH HOLES TO BE DRILLED AT SITE AFTER TRIMMING THE EXTRA END LENGTH FOR BR2 & BR4

**COMPLIANCE BOX**  
COMPLETED AS PER DESIGN ☐  
ALTERATIONS IN RED ☐  
NAME (PRINT) \_\_\_\_\_  
SIGNATURE \_\_\_\_\_ DATE \_\_\_\_\_

NOTE FOR MANUFACTURER & INSTALLER:  
TRIAL ASSEMBLE PRIOR TO GALVANISING AND DELIVERY TO SITE TO ENSURE CORRECT FIT AND NUMBER OF PARTS

**FOR CONSTRUCTION**

**UNAPPROVED  
DRAWING**

**CYIENT**  
Level 14, 3 Parramatta Square, 153 Macquarie St, Parramatta, NSW 2150, Australia  
T +61 2 8896 6160 | www.cyient.com


| ORDER      | DRWN | CHKD | AMENDMENT                                     | EXAM | APPD | DATE     | ISS |
|------------|------|------|-----------------------------------------------|------|------|----------|-----|
| NA25797.01 | DSS  | GNK  | FOR CONSTRUCTION - 80005689WQ540CYI - LTE2100 | MB   | MB   | 21.05.26 | 1   |


© Telstra Limited ACN 086 174 781 All rights reserved.

**Telstra**  
MOBILE NETWORK SITE 40893  
CAMPERDOWN RYDGES MISSENDEN RD  
ANTENNA MOUNTING DETAILS - SHEET 8 OF 9  
9 MISSENDEN RD, CAMPERDOWN, NSW 2050  
DWG NO. **N26167** SHT NO. T3-11

DO NOT  
SCALE

F

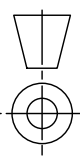

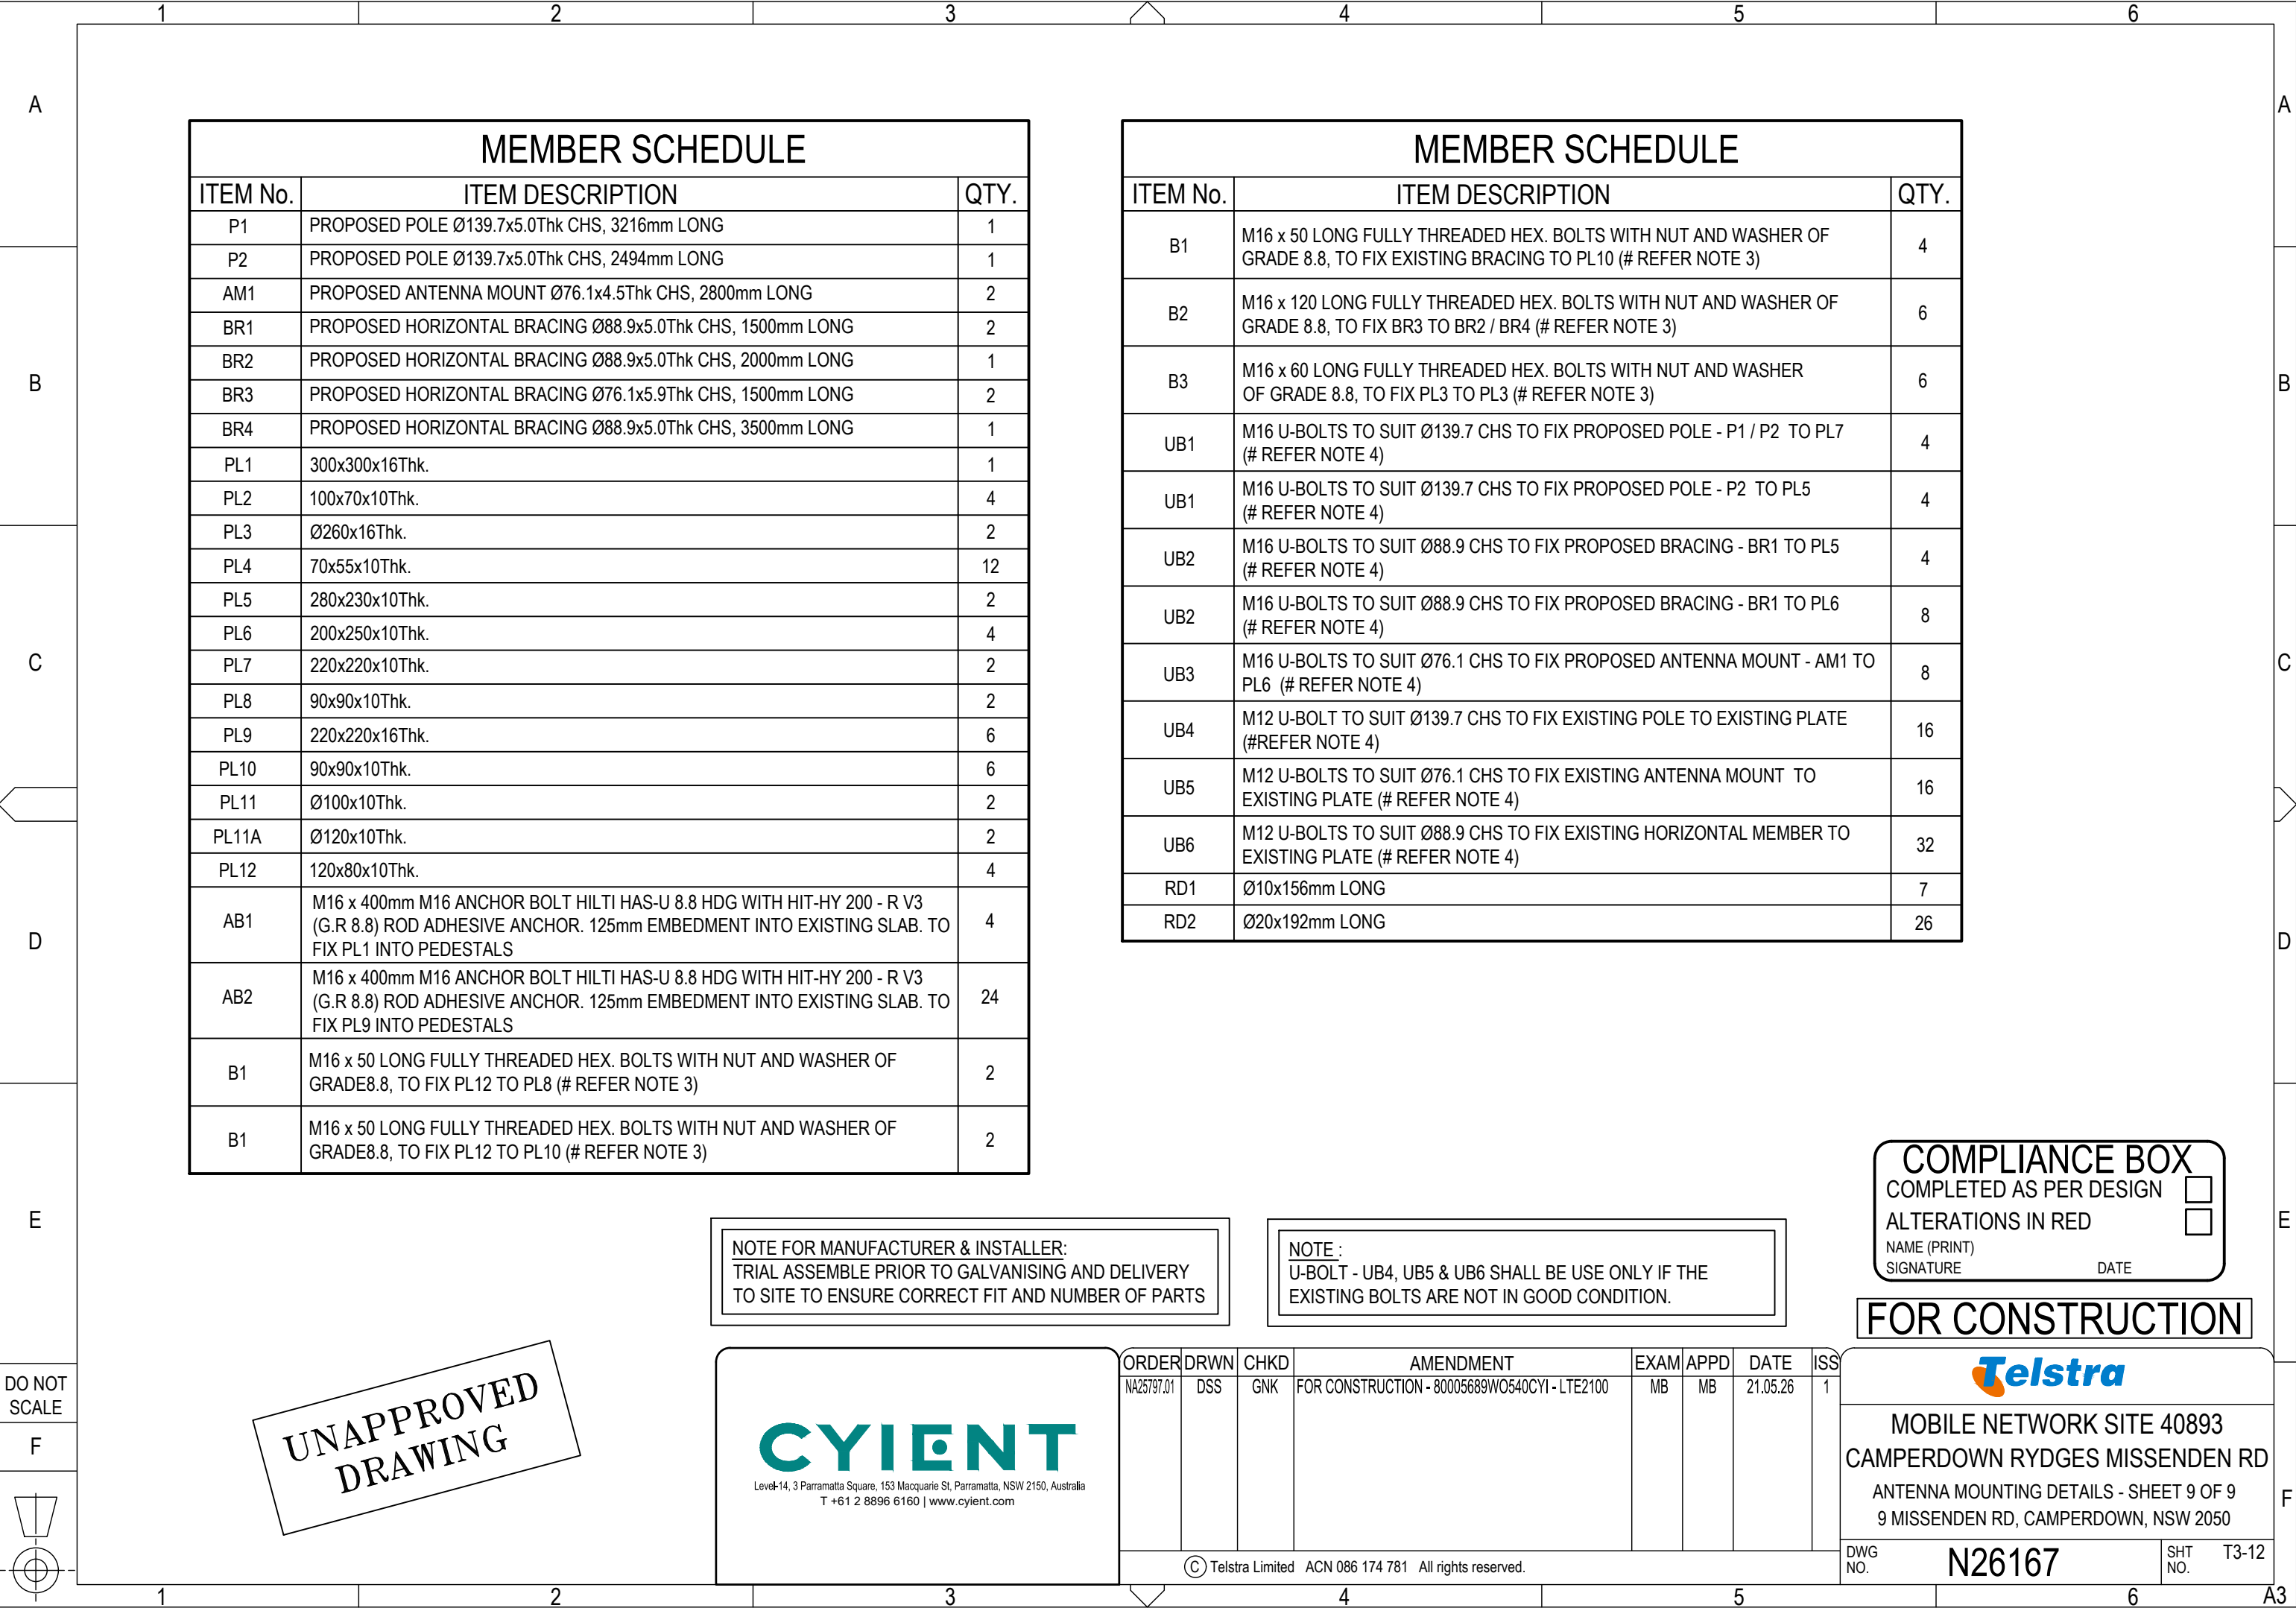

| MEMBER SCHEDULE |   |      |
|-----------------|---|------|
| ITEM No.        | ITEM DESCRIPTION   | QTY. |
| P1              | PROPOSED POLE Ø139.7x5.0Thk CHS, 3216mm LONG   | 1    |
| P2              | PROPOSED POLE Ø139.7x5.0Thk CHS, 2494mm LONG   | 1    |
| AM1             | PROPOSED ANTENNA MOUNT Ø76.1x4.5Thk CHS, 2800mm LONG   | 2    |
| BR1             | PROPOSED HORIZONTAL BRACING Ø88.9x5.0Thk CHS, 1500mm LONG   | 2    |
| BR2             | PROPOSED HORIZONTAL BRACING Ø88.9x5.0Thk CHS, 2000mm LONG   | 1    |
| BR3             | PROPOSED HORIZONTAL BRACING Ø76.1x5.9Thk CHS, 1500mm LONG   | 2    |
| BR4             | PROPOSED HORIZONTAL BRACING Ø88.9x5.0Thk CHS, 3500mm LONG   | 1    |
| PL1             | 300x300x16Thk.   | 1    |
| PL2             | 100x70x10Thk.   | 4    |
| PL3             | Ø260x16Thk.   | 2    |
| PL4             | 70x55x10Thk.   | 12   |
| PL5             | 280x230x10Thk.   | 2    |
| PL6             | 200x250x10Thk.   | 4    |
| PL7             | 220x220x10Thk.   | 2    |
| PL8             | 90x90x10Thk.   | 2    |
| PL9             | 220x220x16Thk.   | 6    |
| PL10            | 90x90x10Thk.   | 6    |
| PL11            | Ø100x10Thk.   | 2    |
| PL11A           | Ø120x10Thk.   | 2    |
| PL12            | 120x80x10Thk.   | 4    |
| AB1             | M16 x 400mm M16 ANCHOR BOLT HILTI HAS-U 8.8 HDG WITH HIT-HY 200 - R V3 (G.R 8.8) ROD ADHESIVE ANCHOR. 125mm EMBEDMENT INTO EXISTING SLAB. TO FIX PL1 INTO PEDESTALS | 4    |
| AB2             | M16 x 400mm M16 ANCHOR BOLT HILTI HAS-U 8.8 HDG WITH HIT-HY 200 - R V3 (G.R 8.8) ROD ADHESIVE ANCHOR. 125mm EMBEDMENT INTO EXISTING SLAB. TO FIX PL9 INTO PEDESTALS | 24   |
| B1              | M16 x 50 LONG FULLY THREADED HEX. BOLTS WITH NUT AND WASHER OF GRADE8.8, TO FIX PL12 TO PL8 (# REFER NOTE 3)                                                        | 2    |
| B1              | M16 x 50 LONG FULLY THREADED HEX. BOLTS WITH NUT AND WASHER OF GRADE8.8, TO FIX PL12 TO PL10 (# REFER NOTE 3)                                                       | 2    |

| MEMBER SCHEDULE |   |      |
|-----------------|---|------|
| ITEM No.        | ITEM DESCRIPTION   | QTY. |
| B1              | M16 x 50 LONG FULLY THREADED HEX. BOLTS WITH NUT AND WASHER OF GRADE 8.8, TO FIX EXISTING BRACING TO PL10 (# REFER NOTE 3) | 4    |
| B2              | M16 x 120 LONG FULLY THREADED HEX. BOLTS WITH NUT AND WASHER OF GRADE 8.8, TO FIX BR3 TO BR2 / BR4 (# REFER NOTE 3)        | 6    |
| B3              | M16 x 60 LONG FULLY THREADED HEX. BOLTS WITH NUT AND WASHER OF GRADE 8.8, TO FIX PL3 TO PL3 (# REFER NOTE 3)               | 6    |
| UB1             | M16 U-BOLTS TO SUIT Ø139.7 CHS TO FIX PROPOSED POLE - P1 / P2 TO PL7 (# REFER NOTE 4)                                      | 4    |
| UB1             | M16 U-BOLTS TO SUIT Ø139.7 CHS TO FIX PROPOSED POLE - P2 TO PL5 (# REFER NOTE 4)                                           | 4    |
| UB2             | M16 U-BOLTS TO SUIT Ø88.9 CHS TO FIX PROPOSED BRACING - BR1 TO PL5 (# REFER NOTE 4)                                        | 4    |
| UB2             | M16 U-BOLTS TO SUIT Ø88.9 CHS TO FIX PROPOSED BRACING - BR1 TO PL6 (# REFER NOTE 4)                                        | 8    |
| UB3             | M16 U-BOLTS TO SUIT Ø76.1 CHS TO FIX PROPOSED ANTENNA MOUNT - AM1 TO PL6 (# REFER NOTE 4)                                  | 8    |
| UB4             | M12 U-BOLT TO SUIT Ø139.7 CHS TO FIX EXISTING POLE TO EXISTING PLATE (#REFER NOTE 4)                                       | 16   |
| UB5             | M12 U-BOLTS TO SUIT Ø76.1 CHS TO FIX EXISTING ANTENNA MOUNT TO EXISTING PLATE (# REFER NOTE 4)                             | 16   |
| UB6             | M12 U-BOLTS TO SUIT Ø88.9 CHS TO FIX EXISTING HORIZONTAL MEMBER TO EXISTING PLATE (# REFER NOTE 4)                         | 32   |
| RD1             | Ø10x156mm LONG   | 7    |
| RD2             | Ø20x192mm LONG   | 26   |

NOTE FOR MANUFACTURER & INSTALLER:  
TRIAL ASSEMBLE PRIOR TO GALVANISING AND DELIVERY  
TO SITE TO ENSURE CORRECT FIT AND NUMBER OF PARTS

NOTE :  
U-BOLT - UB4, UB5 & UB6 SHALL BE USE ONLY IF THE  
EXISTING BOLTS ARE NOT IN GOOD CONDITION.

COMPLIANCE BOX

COMPLETED AS PER DESIGN

ALTERATIONS IN RED

NAME (PRINT)

SIGNATURE

DATE

FOR CONSTRUCTION

UNAPPROVED  
DRAWING

CYIENT

Level 14, 3 Parramatta Square, 153 Macquarie St, Parramatta, NSW 2150, Australia  
T +61 2 8896 6160 | www.cyient.com

| ORDER      | DRWN | CHKD | AMENDMENT                                     | EXAM | APPD | DATE     | ISS |
|------------|------|------|-----------------------------------------------|------|------|----------|-----|
| NA25797.01 | DSS  | GNK  | FOR CONSTRUCTION - 80005689WO540CYI - LTE2100 | MB   | MB   | 21.05.26 | 1   |

© Telstra Limited ACN 086 174 781 All rights reserved.



MOBILE NETWORK SITE 40893  
CAMPERDOWN RYDGES MISSENDEN RD  
ANTENNA MOUNTING DETAILS - SHEET 9 OF 9  
9 MISSENDEN RD, CAMPERDOWN, NSW 2050


DWG  
NO.

N26167

SHT  
NO.


T3-12



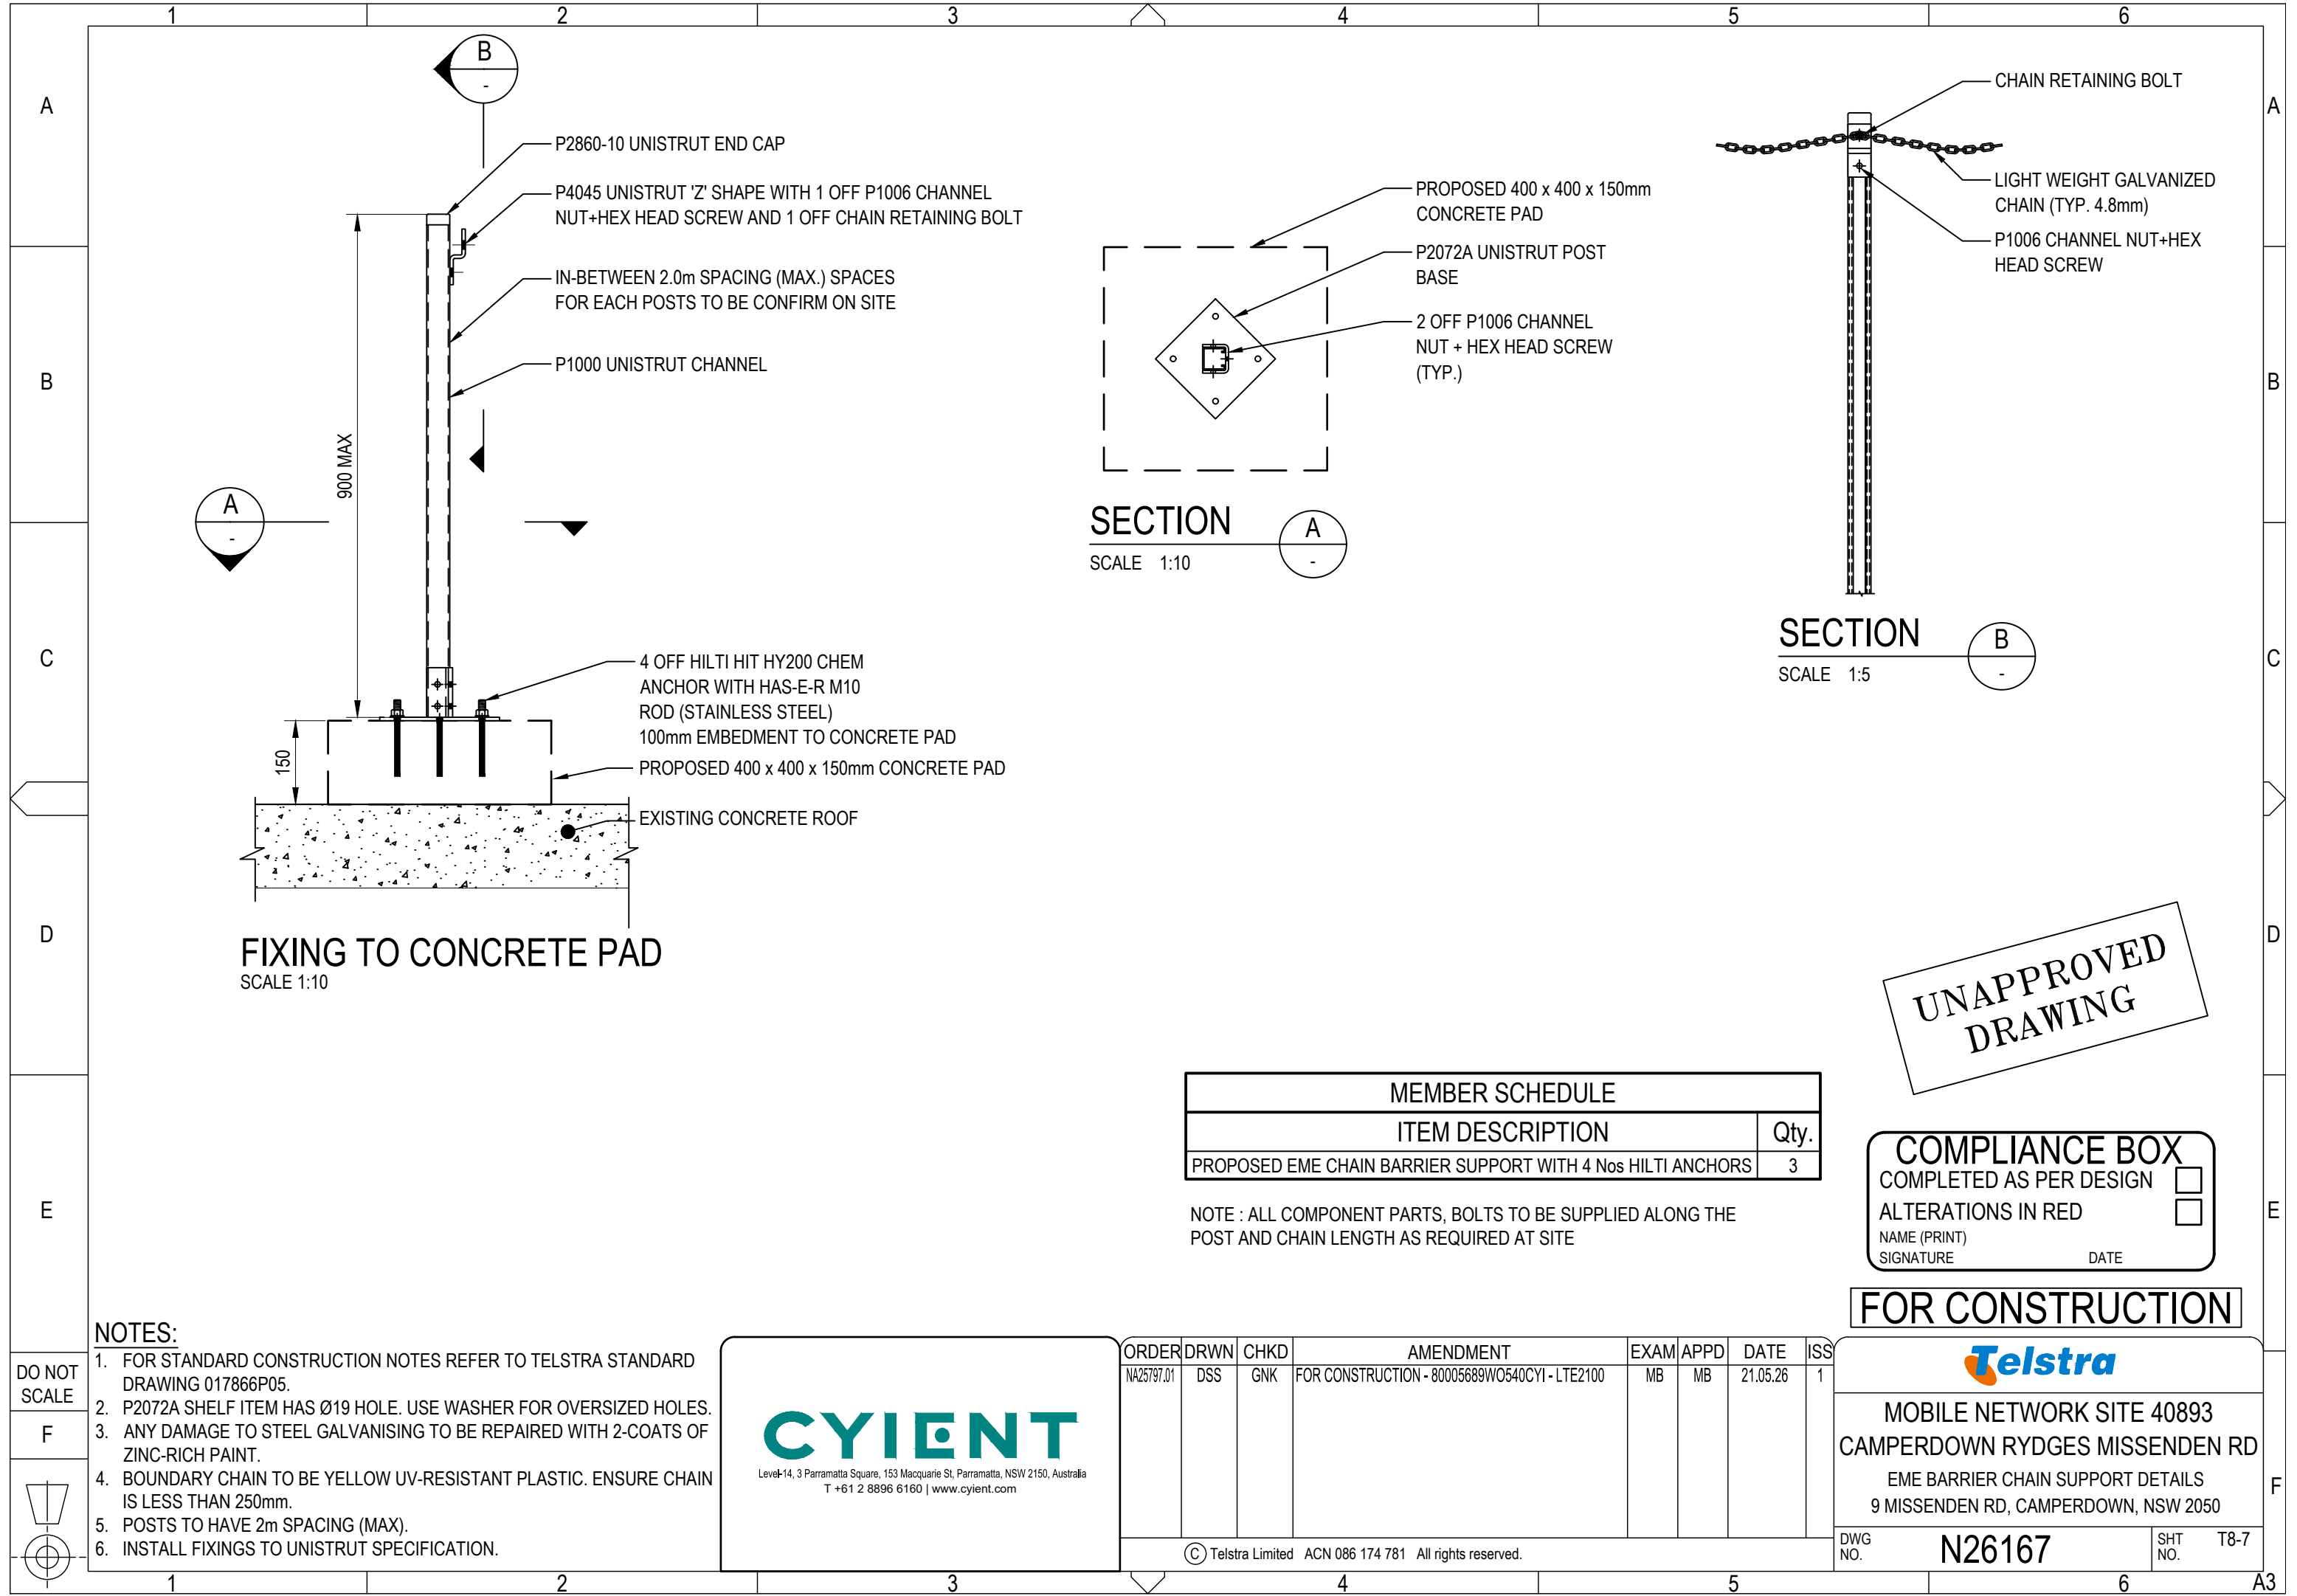

DO NOT  
SCALE

F

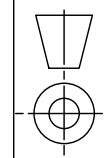

- NOTES:
- FOR STANDARD CONSTRUCTION NOTES REFER TO TELSTRA STANDARD DRAWING 017866P05.
  - P2072A SHELF ITEM HAS Ø19 HOLE. USE WASHER FOR OVERSIZED HOLES.
  - ANY DAMAGE TO STEEL GALVANISING TO BE REPAIRED WITH 2-COATS OF ZINC-RICH PAINT.
  - BOUNDARY CHAIN TO BE YELLOW UV-RESISTANT PLASTIC. ENSURE CHAIN IS LESS THAN 250mm.
  - POSTS TO HAVE 2m SPACING (MAX).
  - INSTALL FIXINGS TO UNISTRUT SPECIFICATION.

**CYIENT**  
Level 14, 3 Parramatta Square, 153 Macquarie St, Parramatta, NSW 2150, Australia  
T +61 2 8896 6160 | www.cyient.com

| ORDER                                                  | DRWN | CHKD | AMENDMENT                                     | EXAM | APPD | DATE     | ISS |
|--------------------------------------------------------|------|------|-----------------------------------------------|------|------|----------|-----|
| NA25797.01                                             | DSS  | GNK  | FOR CONSTRUCTION - 80005689W0540CYI - LTE2100 | MB   | MB   | 21.05.26 | 1   |
| © Telstra Limited ACN 086 174 781 All rights reserved. |      |      |                                               |      |      |          |     |

|                         |                          |
|-------------------------|--------------------------|
| <b>COMPLIANCE BOX</b>   |                          |
| COMPLETED AS PER DESIGN | <input type="checkbox"/> |
| ALTERATIONS IN RED      | <input type="checkbox"/> |
| NAME (PRINT)            |                          |
| SIGNATURE               | DATE                     |

FOR CONSTRUCTION

|   |        |
|---|--------|
| <b>Telstra</b>   |        |
| MOBILE NETWORK SITE 40893<br>CAMPERDOWN RYDGES MISSENDEN RD<br>EME BARRIER CHAIN SUPPORT DETAILS<br>9 MISSENDEN RD, CAMPERDOWN, NSW 2050 |        |
| DWG NO.   | N26167 |
| SHT NO.   | T8-7   |